
**MINISTERSTVO DOPRAVY**

# VZOROVÉ LISTY

STAVEB POZEMNÍCH KOMUNIKACÍ

# VL 6.2 – VODOROVNÉ DOPRAVNÍ ZNAČKY

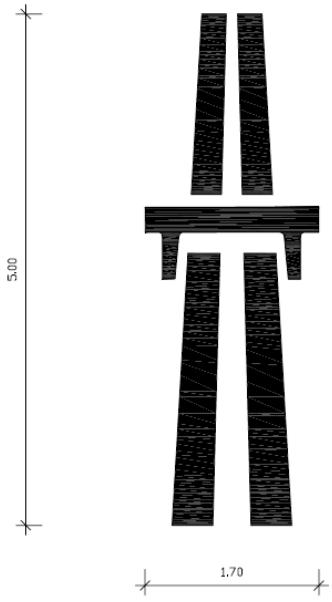


**únor 2017**







Schváleno Ministerstvem dopravy č. j. 43/2017-120-TN/1 ze dne 9. února 2017
s **účinností od 15. února 2017**.

Tento dokument se shoduje se schválenou verzí.

Současně se ruší a nahrazují v celém rozsahu vzorové listy VL 6.2 – Vodorovné dopravní značky schválené Ministerstvem dopravy pod č. j. 354/2004-O120-STSP/2 s účinností od 1. července 2004.

**Distribuce pouze v elektronické podobě na webu pjpk.cz.**

**VZOROVÉ LISTY STAVEB POZEMNÍCH KOMUNIKACÍ**

CELKOVÝ PŘEHLED


VL 1 VOZOVKY A KRAJNICE

VL 2.1 SILNIČNÍ TĚLESO

VL 2.2 ODVODNĚNÍ

VL 3 KŘIŽOVATKY

VL 4 MOSTY

VL 5 TUNELY

VL 6.1 SVISLÉ DOPRAVNÍ ZNAČKY

**VL 6.2 VODOROVNÉ DOPRAVNÍ ZNAČKY**

**TECHNICKÁ ZPRÁVA**

**SEZNAM VZOROVÝCH LISTŮ**

**ŠIPKY**

**PÍSMO**

**SYMBOLY**

VL 6.3 DOPRAVNÍ ZAŘÍZENÍ

VL 6.4 PROMĚNNÉ DOPRAVNÍ ZNAČENÍ

VL 7 VYBRANÉ PRVKY MÍSTNÍCH KOMUNIKACÍ PRO ZKLIDŇOVÁNÍ DOPRAVY

VL 0 VZOROVÉ LISTY OPRAV MOSTNÍCH OBJEKTŮ

# Technická zpráva

## Obsah technické zprávy

1. PŘEDMĚT A ÚČEL VZOROVÝCH LISTŮ ..... 4

2. OZNAČENÍ VZOROVÝCH LISTŮ ..... 4

3. TEXTOVÁ ČÁST ..... 5

3.1. VŠEOBECNĚ ..... 5

3.2. BAREVNÉ PROVEDENÍ ..... 5

3.3. ODCHYLKY ROZMĚRŮ ..... 5

4. GRAFICKÁ ČÁST ..... 6

# 1. PŘEDMĚT A ÚČEL VZOROVÝCH LISTŮ

Vzorové listy (VL) upravují provedení vodorovných dopravních značek. Rozpracovávají ustanovení příslušných předpisů včetně mezinárodních do potřebných detailů, a tím vytvářejí předpoklady pro jednotné provedení jednotlivých vodorovných dopravních značek. Využití vzorových listů při vyznačování (případně ve výrobě) vodorovných dopravních značek sleduje zájem zvýšení kvality dopravního značení.

Vzorové listy věcně navazují na:

(1) zákon č. 361/2000 Sb., o provozu na pozemních komunikacích a o změnách některých zákonů (zákon o silničním provozu), ve znění pozdějších předpisů,

(2) vyhlášku č. 294/2015 Sb., kterou se provádějí pravidla provozu na pozemních komunikacích, ve znění pozdějších předpisů,

(3) (737010) ČSN EN 1436 + A1 Vodorovné dopravní značení – Požadavky na dopravní značení.

Význam jednotlivých vodorovných dopravních značek a podmínky pro jejich užití a umístění upravují:

(1) vyhláška č. 294/2015 Sb., kterou se provádějí pravidla provozu na pozemních komunikacích, ve znění pozdějších předpisů (dále jen „vyhláška“),

(2) TP 65 Zásady pro dopravní značení na pozemních komunikacích,

(3) TP 66 Zásady pro označování pracovních míst na pozemních komunikacích,

(4) TP 70 Zásady pro provádění a zkoušení vodorovného dopravního značení,

(5) TP 100 Zásady pro orientační dopravní značení na pozemních komunikacích,

(6) TP 133 Zásady pro vodorovné dopravní značení na pozemních komunikacích.

# 2. OZNAČENÍ VZOROVÝCH LISTŮ

Dosud užívaný systém značení VL byl pro lepší přehlednost změněn. Označení skupin a podskupin bylo nahrazeno číslem vodorovné dopravní značky.

Členění vzorových listů:

Pro označení vzorových listů byla určena zkratka VL a dále třídění, které má následují formu a obsah:

**VL X**

**X XXX – XX**

**XX.XX**

| | |
|---|---|
| **X** | označuje VL podle základního obsahu |
| **X XXX – XX** | označuje číslo vodorovné dopravní značky a pořadí vzorového listu této značky |

**XX.XX** první dvě číslice označují měsíc, další dvě číslice označují rok poslední aktualizace VL

Kompletní jednoznačné označení zní například: VL 6.2 V 15 – 1 02.17

VL 6.2 V 15 – 2 02.17

VL jsou zpracovány ve formě otevřeného souboru, který je možno průběžně upravovat nebo doplňovat.

Obsahem textové části jsou základní zásady geometrického provedení vodorovných dopravních značek (dále jen „dopravních značek“). Obsahem obrazové části jsou výkresy jednotlivých dopravních značek, včetně vybraných variant. Rozdělení dopravních značek do skupin vychází z členění podle vyhlášky.

Všechny rozměry jsou uvedeny v m.

# 3. TEXTOVÁ ČÁST

## 3.1. VŠEOBECNĚ

Základní tvary dopravních značek stanovuje vyhláška. Funkční požadavky se týkají denní a noční viditelnosti, drsnosti a trvanlivosti. Stanovují je (737010) ČSN EN 1436 + A1 a TP 70. Rozměry dopravních značek upravují tyto VL.

## 3.2. BAREVNÉ PROVEDENÍ

Vodorovné dopravní značení se provádí v barvě bílé, žluté nebo modré. Základní barevné provedení dopravních značek stanovuje vyhláška.

Pro přechodné vodorovné značky vyjadřující čáry nebo šipky nebo označující přechody pro chodce nebo jízdní pruhy pro cyklisty se užívá barva žlutá nebo oranžová. Pro symboly svislých dopravních značek se užívá barva bílá nebo se užívají barvy odpovídající barevnému provedení příslušné svislé dopravní značky.

## 3.3. ODCHYLKY ROZMĚRŮ

Proti rozměrům vodorovných dopravních značek a symbolů uvedených v těchto vzorových listech jsou přijatelné tyto mezní odchylky z jejich rozměrů:

- u podélných čar v podélném směru $\pm$ 50 mm, v šířce čáry $\pm$ 10 mm,
- u příčných čar + 50 mm ve všech směrech,
- u vzdáleností jednotlivých čar značky „Přechod pro chodce“, „Přejezd pro cyklisty“, „Šikmé rovnoběžné čáry“ a „Křivky“ v odůvodněných případech (např. spára, kolejnice) $\pm$ 50 mm,
- u šipek, písma a ostatních značek a symbolů – 1 cm a + 2 cm v příčném i podélném směru,
- osa podélných čar může být plynule odchýlená nejvíce ± 25 mm od stanovené osy značení nejvýše jednou na 100 m délky značení.


# 4. GRAFICKÁ ČÁST

| ŠIPKY | | Datum |
|---|---|---|
| **6.2 V 9a – 1** | Směrové šipky | 02.2017 |
| **6.2 V 9a – 2** | Směrové šipky | 02.2017 |
| **6.2 V 9a – 3** | Směrové šipky | 02.2017 |
| **6.2 V 9a – 4** | Směrové šipky | 02.2017 |
| **6.2 V 9a – 5** | Směrové šipky | 02.2017 |
| **6.2 V 9a – 6** | Směrové šipky | 02.2017 |
| **6.2 V 9a – 7** | Směrové šipky | 02.2017 |
| **6.2 V 9a – 8** | Směrové šipky | 02.2017 |
| **6.2 V 9a – 9** | Směrové šipky (pro cyklisty) | 02.2017 |
| **6.2 V 9a – 10** | Směrové šipky (pro cyklisty) | 02.2017 |
| **6.2 V 9a – 11** | Směrové šipky (pro cyklisty) | 02.2017 |
| **6.2 V 9a – 12** | Směrové šipky (pro cyklisty) | 02.2017 |
| **6.2 V 9a – 13** | Směrové šipky | 02.2017 |
| **6.2 V 9a – 14** | Směrové šipky | 02.2017 |
| **6.2 V 9a – 15** | Směrové šipky | 02.2017 |
| **6.2 V 9a – 16** | Směrové šipky | 02.2017 |
| **6.2 V 9a – 17** | Směrové šipky | 02.2017 |
| **6.2 V 9a – 18** | Směrové šipky | 02.2017 |
| **6.2 V 9b** | Předběžné šipky | 02.2017 |
| **6.2 V 9c – 1** | Předběžné šipky | 02.2017 |
| **6.2 V 9c – 2** | Předběžné šipky | 02.2017 |


| PÍSMO | | Datum |
|---|---|---|
| **6.2 V 15 – 1** | Písmena | 02.2017 |
| **6.2 V 15 – 2** | Písmena | 02.2017 |
| **6.2 V 15 – 3** | Písmena | 02.2017 |
| **6.2 V 15 – 4** | Písmena | 02.2017 |
| **6.2 V 15 – 5** | Písmena | 02.2017 |
| **6.2 V 15 – 6** | Písmena | 02.2017 |
| **6.2 V 15 – 7** | Písmena | 02.2017 |
| **6.2 V 15 – 8** | Písmena | 02.2017 |
| **6.2 V 15 – 9** | Písmena | 02.2017 |
| **6.2 V 15 – 10** | Číslice | 02.2017 |
| **6.2 V 15 – 11** | Číslice | 02.2017 |
| **6.2 V 15 – 12** | Číslice | 02.2017 |
| **6.2 V 15 – 13** | Číslice | 02.2017 |

| SYMBOLY | | Datum |
|---|---|---|
| **6.2 V 15 – 14** | Nápis na vozovce – Symbol značky č. A 1a Zatáčka vpravo | 02.2017 |
| **6.2 V 15 – 15** | Nápis na vozovce – Symbol značky č. A 1b Zatáčka vlevo | 02.2017 |
| **6.2 V 15 – 16** | Nápis na vozovce – Symbol značky č. A 3 Křižovatka | 02.2017 |
| **6.2 V 15 – 17** | Nápis na vozovce – Symbol značky č. A 4 Křižovatka s kruhovým objezdem | 02.2017 |
| **6.2 V 15 – 18** | Nápis na vozovce – Symbol značky č. A 11 Přechod pro chodce | 02.2017 |
| **6.2 V 15 – 19** | Nápis na vozovce – Symbol značky č. A 12a Chodci | 02.2017 |
| **6.2 V 15 – 20** | Nápis na vozovce – Symbol značky č. A 12b Děti | 02.2017 |
| **6.2 V 15 – 21** | Nápis na vozovce – Symbol značky č. A 19 Cyklisté | 02.2017 |
| **6.2 V 15 – 22** | Nápis na vozovce – Symbol značky č. A 22 Jiné nebezpečí | 02.2017 |

| | | |
|---|---|---|
| **6.2 V 15 – 23** | Nápis na vozovce – Symbol značky č. A 25 Tramvaj | 02.2017 |
| **6.2 V 15 – 24** | Nápis na vozovce – Symbol značky č. A 32 a Výstražný kříž pro železniční přejezd jednokolejný | 02.2017 |
| **6.2 V 15 – 25** | Nápis na vozovce – Symbol značky č. P 4 Dej přednost v jízdě! | 02.2017 |
| **6.2 V 15 – 26** | Nápis na vozovce – Symbol značky č. P 4 Dej přednost v jízdě! | 02.2017 |
| **6.2 V 15 – 27** | Nápis na vozovce – Symbol značky č. P 6 Stůj, dej přednost v jízdě! | 02.2017 |
| **6.2 V 15 – 28** | Nápis na vozovce – Symbol značky č. P 6 Stůj, dej přednost v jízdě! | 02.2017 |
| **6.2 V 15 – 29** | Nápis na vozovce – Symbol značky č. B 20a Nejvyšší dovolená rychlost | 02.2017 |
| **6.2 V 15 – 30** | Nápis na vozovce – Symbol značky č. IZ 1a Dálnice | 02.2017 |
| **6.2 V 15 – 31** | Nápis na vozovce – Symbol značky č. IZ 2a Silnice pro motorová vozidla | 02.2017 |
| **6.2 V 15 – 32** | Nápis na vozovce – Symbol značky č. IS 16b Číslo silnice | 02.2017 |
| **6.2 V 15 – 33** | Nápis na vozovce – Symbol značky č. IS 16b Číslo silnice | 02.2017 |
| **6.2 V 15 – 34** | Nápis na vozovce – Symbol značky č. IS 16b Číslo silnice | 02.2017 |
| **6.2 V 15 – 35** | Nápis na vozovce – Symbol značky č. IS 17 Číslo silnice pro mezinárodní provoz | 02.2017 |
| **6.2 V 15 – 36** | Nápis na vozovce – Symbol značky č. IS 17 Číslo silnice pro mezinárodní provoz | 02.2017 |
| **6.2 V 15 – 37** | Nápis na vozovce – BUS, TRAM | 02.2017 |
| **6.2 V 15 – 38** | Nápis na vozovce – Symbol ze značky č. V 14 | 02.2017 |
| **6.2 V 15 – 39** | Nápis na vozovce – Symbol ze značky č. V 10f | 02.2017 |
| **6.2 V 15 – 40** | Nápis na vozovce – Symbol dobíjející stanice elektromobilů | 02.2017 |
| **6.2 V 15 – 41** | Nápis na vozovce – Symbol značky č. B 20a Nejvyšší dovolená rychlost | 02.2017 |
| **6.2 V 16** | Bezpečný odstup | 02.2017 |
| **6.2 V 17** | Trojúhelníky | 02.2017 |
| **6.2 V 18 – 1** | Optická psychologická brzda | 02.2017 |
| **6.2 V 18 – 2** | Optická psychologická brzda (Trychtýřová brzda) | 02.2017 |
| **6.2 V 20** | Piktogramový koridor pro cyklisty | 02.2017 |

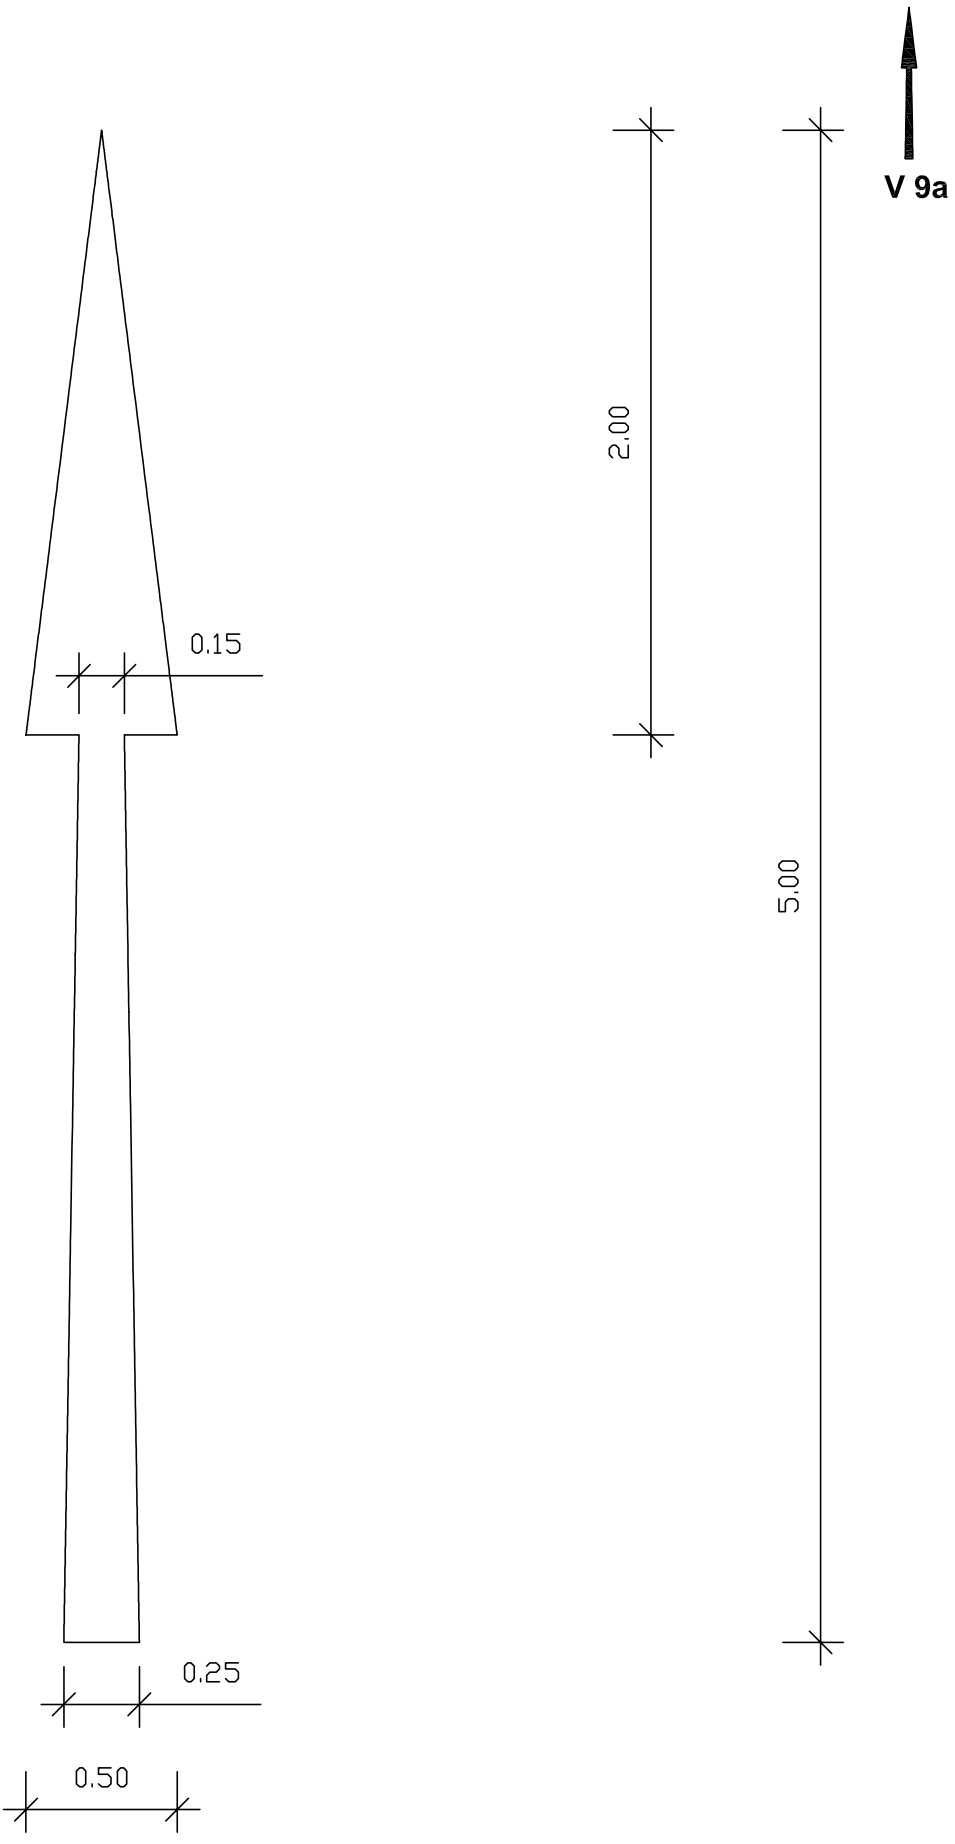



| | | | |
|---|---|---|---|
| **6** **VYBAVENÍ POZEMNÍCH KOMUNIKACÍ**<br>**6.2** **VODOROVNÉ DOPRAVNÍ ZNAČKY**<br>**Šipky**<br>**V 9a Směrové šipky** | **MINISTERSTVO DOPRAVY**<br>**ODBOR POZEMNÍCH KOMUNIKACÍ**<br>**VZOROVÉ LISTY** | **VL 6**<br>**V 9a - 1**<br>**02.17** |

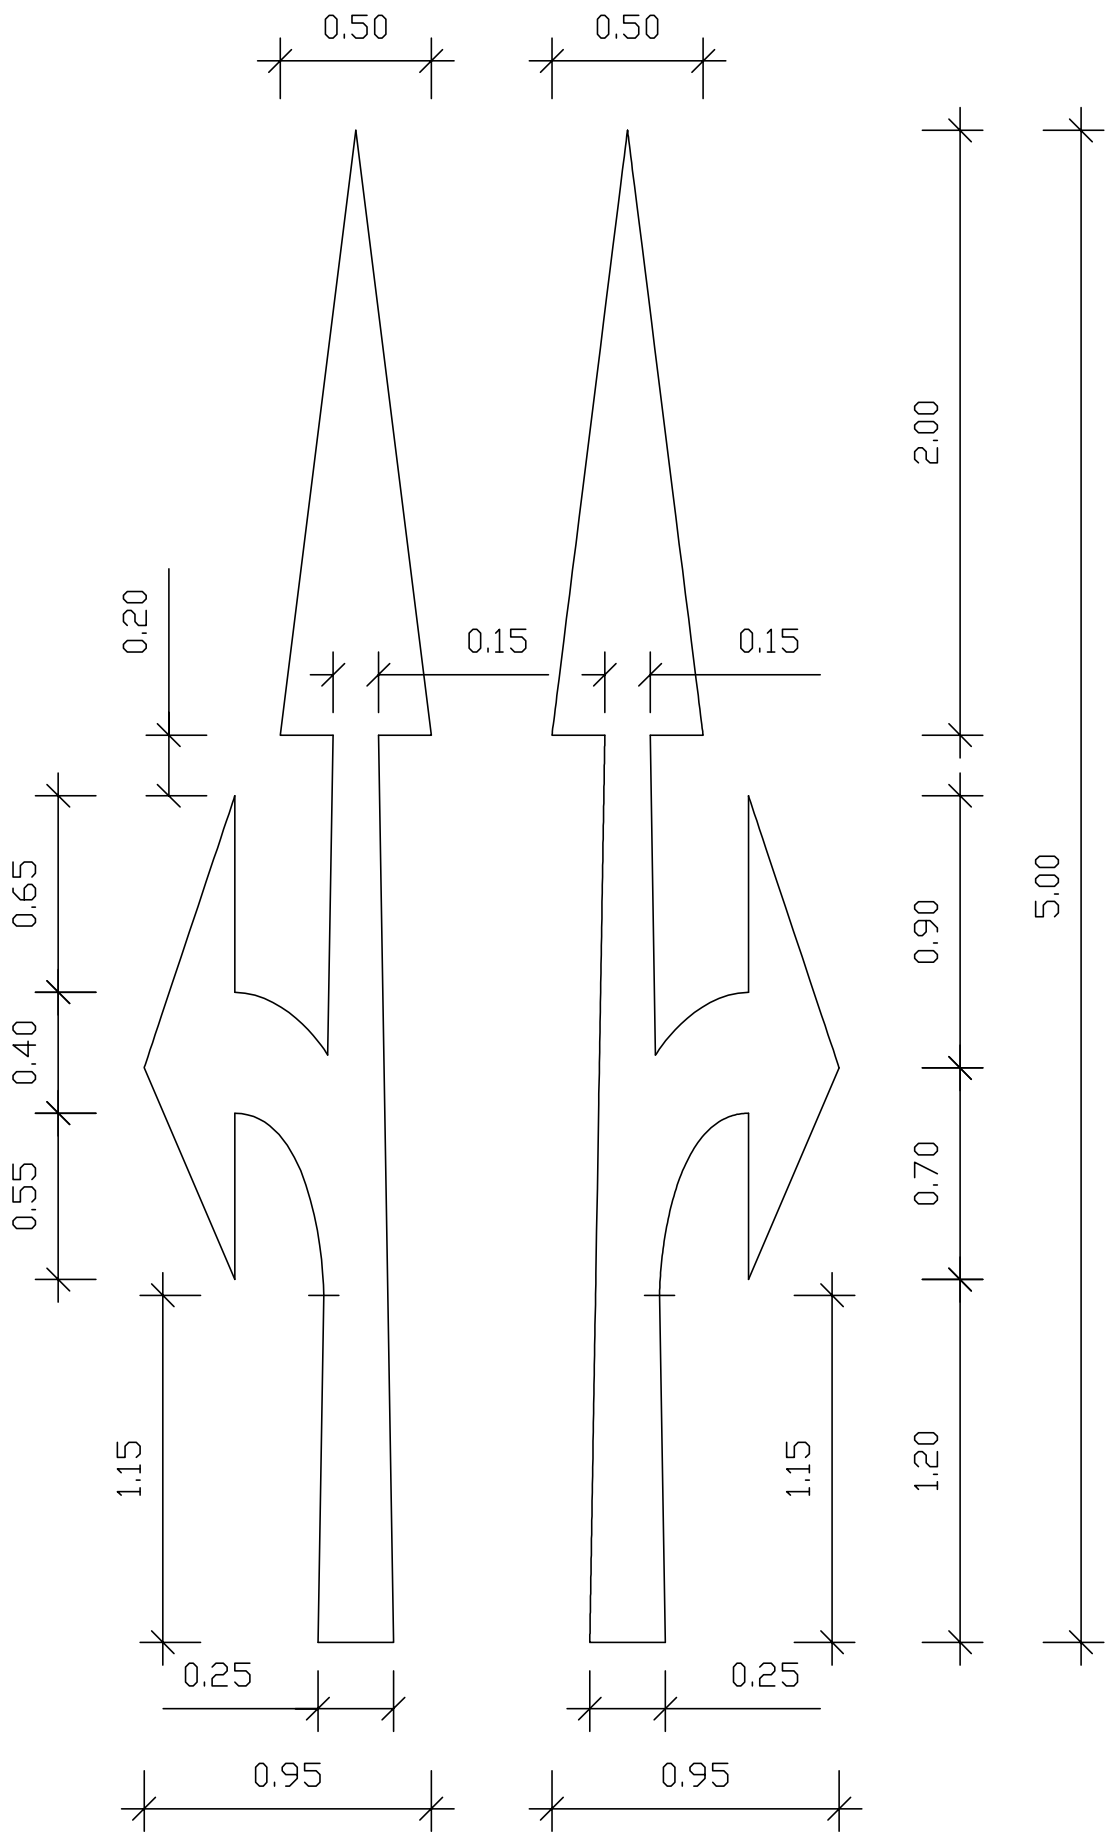




**V 9a**


| | | | |
|---|---|---|---|
| **6** **VYBAVENÍ POZEMNÍCH KOMUNIKACÍ**<br>**6.2** **VODOROVNÉ DOPRAVNÍ ZNAČKY**<br>**Šipky**<br>**V 9a Směrové šipky** | **MINISTERSTVO DOPRAVY**<br>**ODBOR POZEMNÍCH KOMUNIKACÍ**<br>**VZOROVÉ LISTY** | **VL 6**<br>**V 9a - 2**<br>**02.17** |

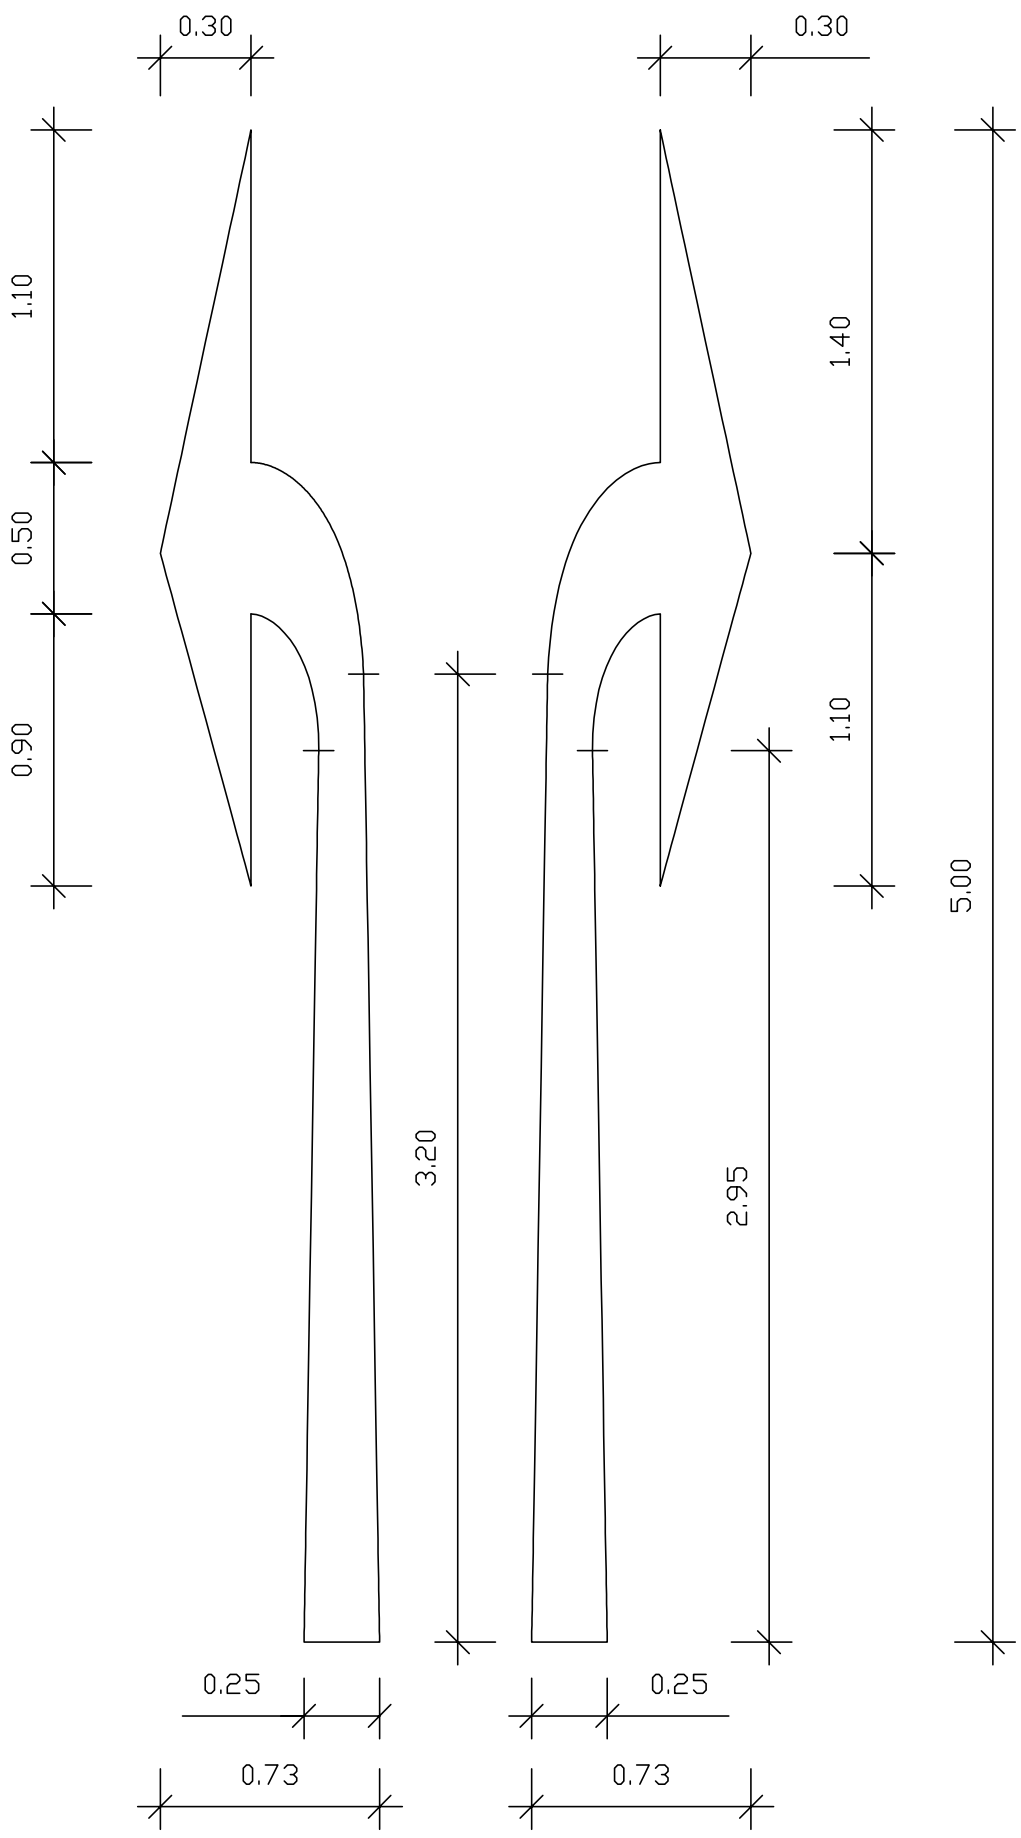




**V 9a**


| | | | |
|---|---|---|---|
| **6** **VYBAVENÍ POZEMNÍCH KOMUNIKACÍ**<br>**6.2** **VODOROVNÉ DOPRAVNÍ ZNAČKY**<br>**Šipky**<br>**V 9a Směrové šipky** | **MINISTERSTVO DOPRAVY**<br>**ODBOR POZEMNÍCH KOMUNIKACÍ**<br>**VZOROVÉ LISTY** | **VL 6**<br>**V 9a - 3**<br>**02.17** |

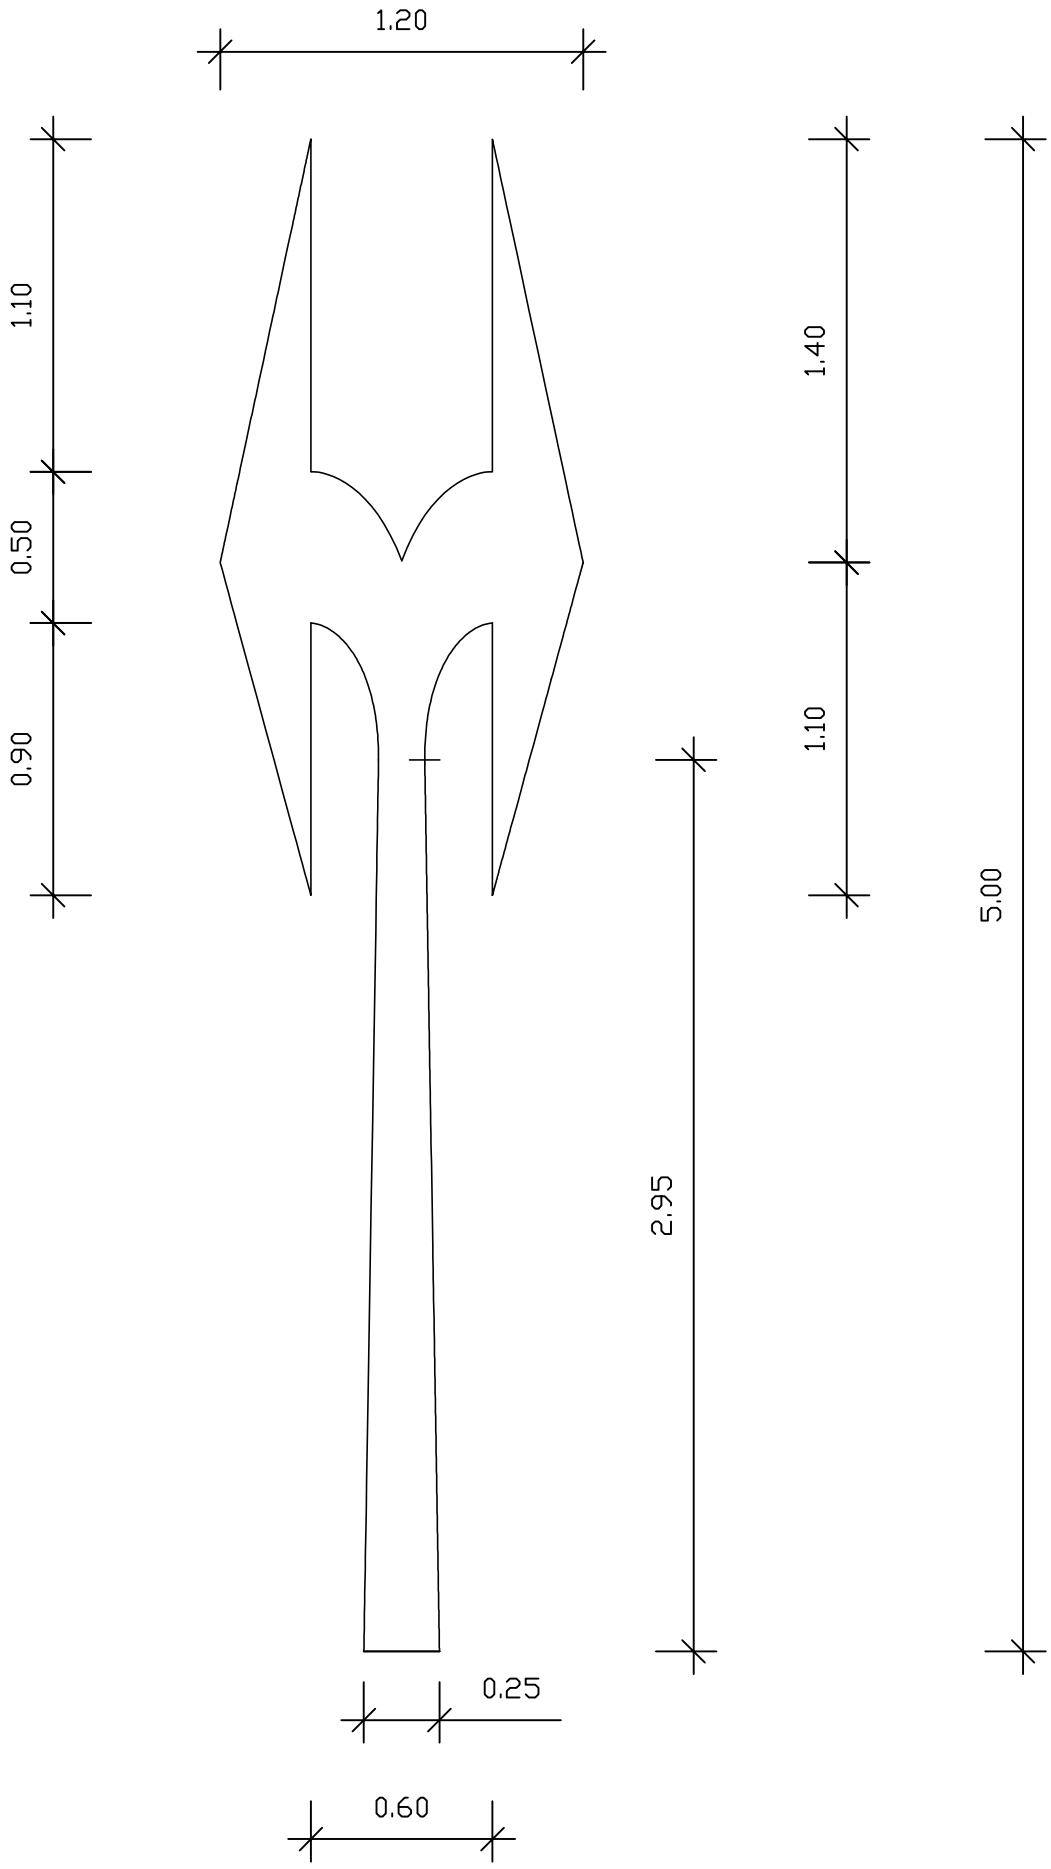





**V 9a**

| | | | |
|---|---|---|---|
| **6** **VYBAVENÍ POZEMNÍCH KOMUNIKACÍ**<br>**6.2** **VODOROVNÉ DOPRAVNÍ ZNAČKY**<br>**Šipky**<br>**V 9a Směrové šipky** | **MINISTERSTVO DOPRAVY**<br>**ODBOR POZEMNÍCH KOMUNIKACÍ**<br>**VZOROVÉ LISTY** | **VL 6**<br>**V 9a - 4**<br>**02.17** |

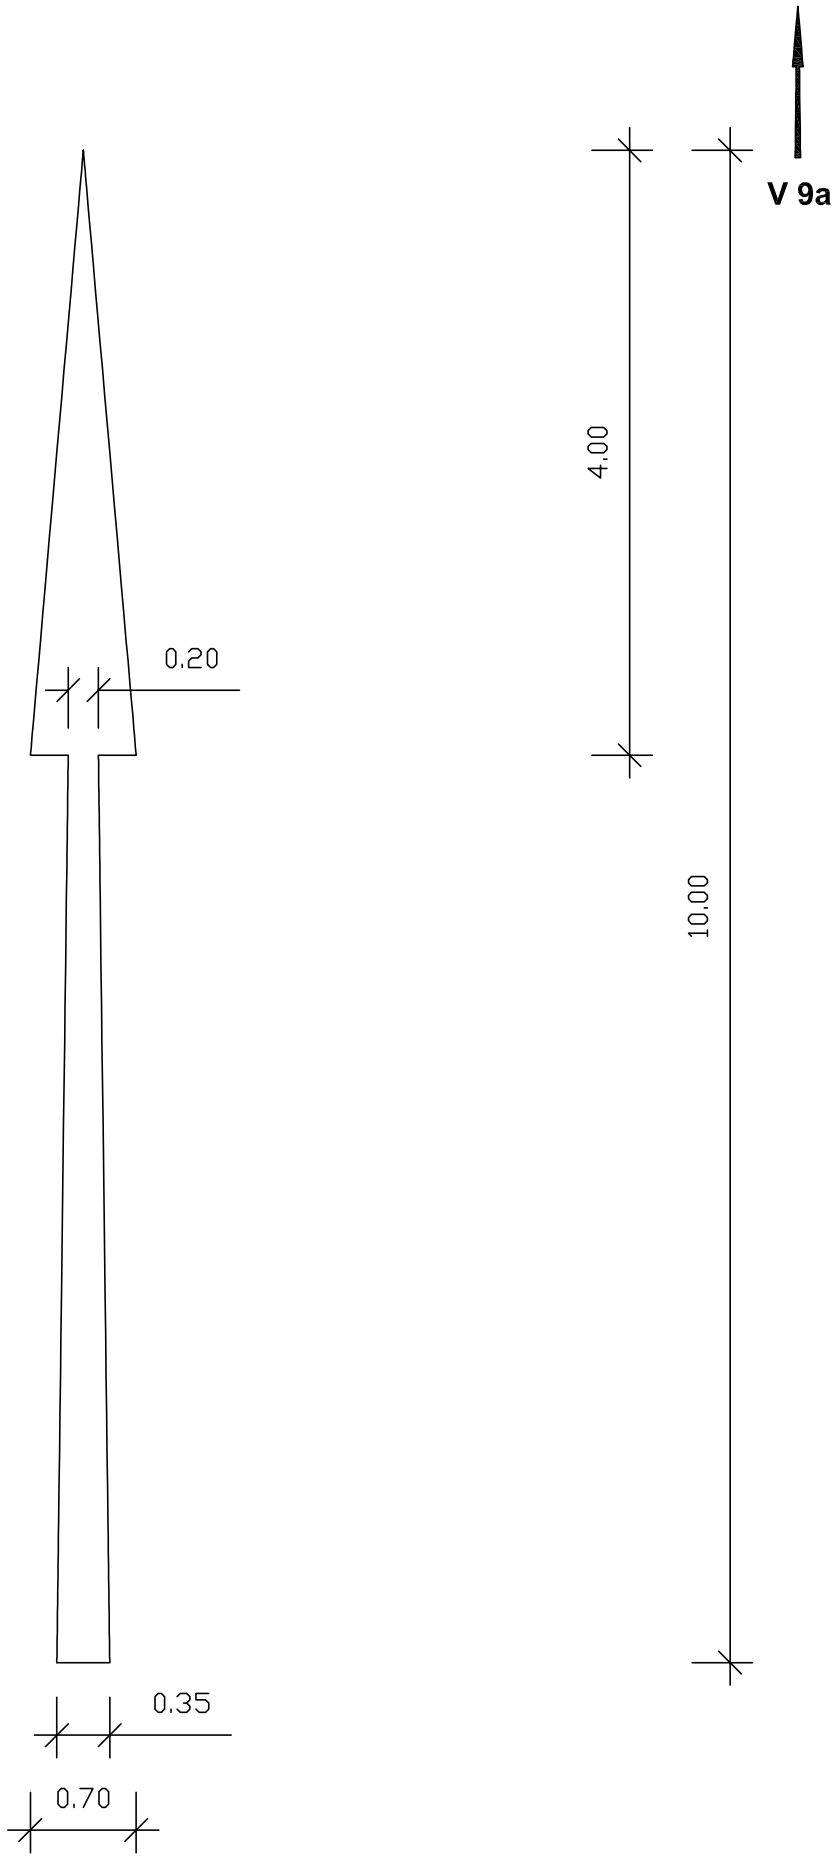



| | | | |
|---|---|---|---|
| **6** **VYBAVENÍ POZEMNÍCH KOMUNIKACÍ**<br>**6.2** **VODOROVNÉ DOPRAVNÍ ZNAČKY**<br>**Šipky**<br>**V 9a** **Směrové šipky** | **MINISTERSTVO DOPRAVY**<br>**ODBOR POZEMNÍCH KOMUNIKACÍ**<br>**VZOROVÉ LISTY** | **VL 6**<br>**V 9a - 5**<br>**02.17** |

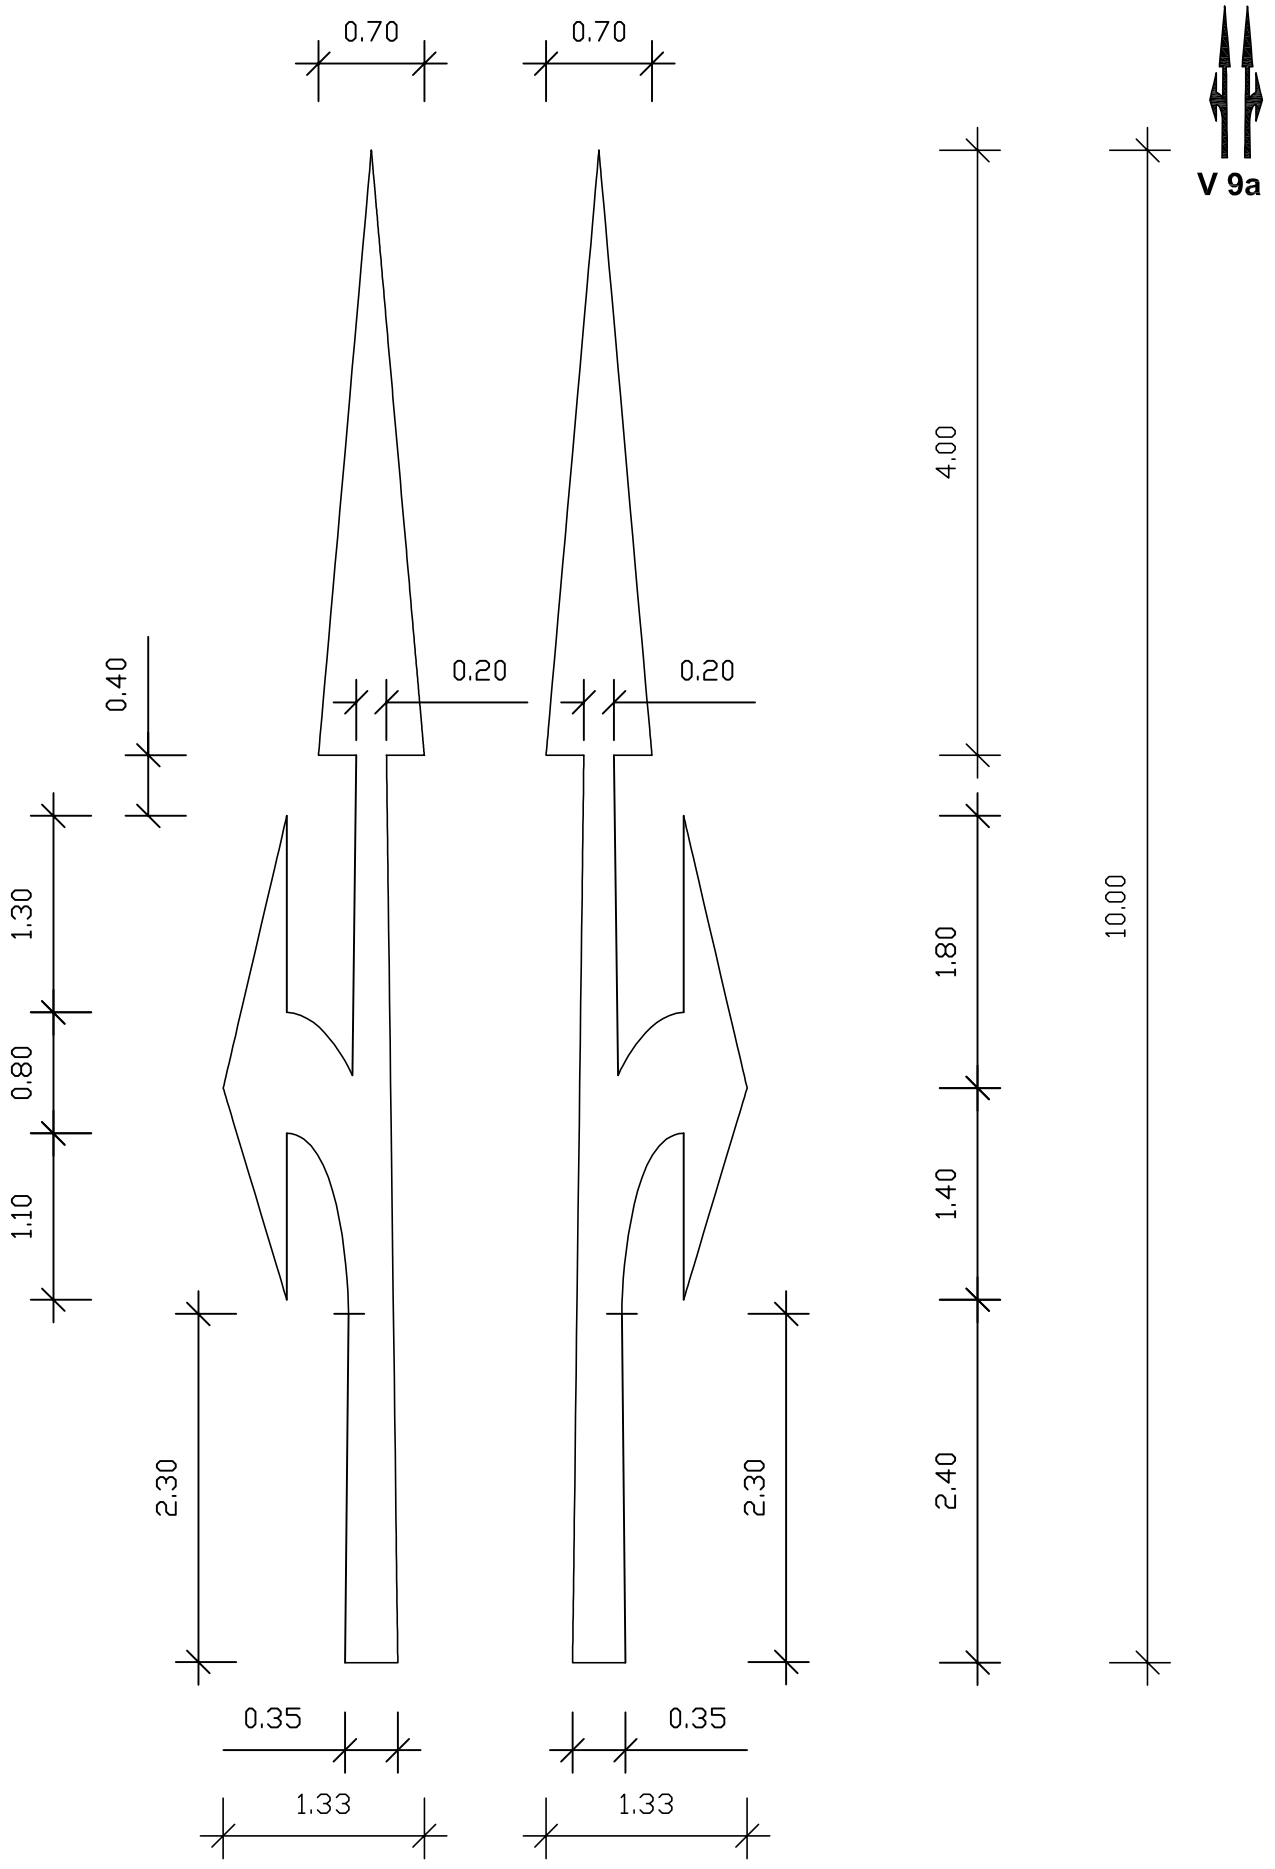



V 9a

| | | | |
|---|---|---|---|
| **6** **VYBAVENÍ POZEMNÍCH KOMUNIKACÍ**<br>**6.2** **VODOROVNÉ DOPRAVNÍ ZNAČKY**<br>**Šipky**<br>**V 9a Směrové šipky** | **MINISTERSTVO DOPRAVY**<br>**ODBOR POZEMNÍCH KOMUNIKACÍ**<br>**VZOROVÉ LISTY** | **VL 6**<br>**V 9a - 6**<br>**02.17** |

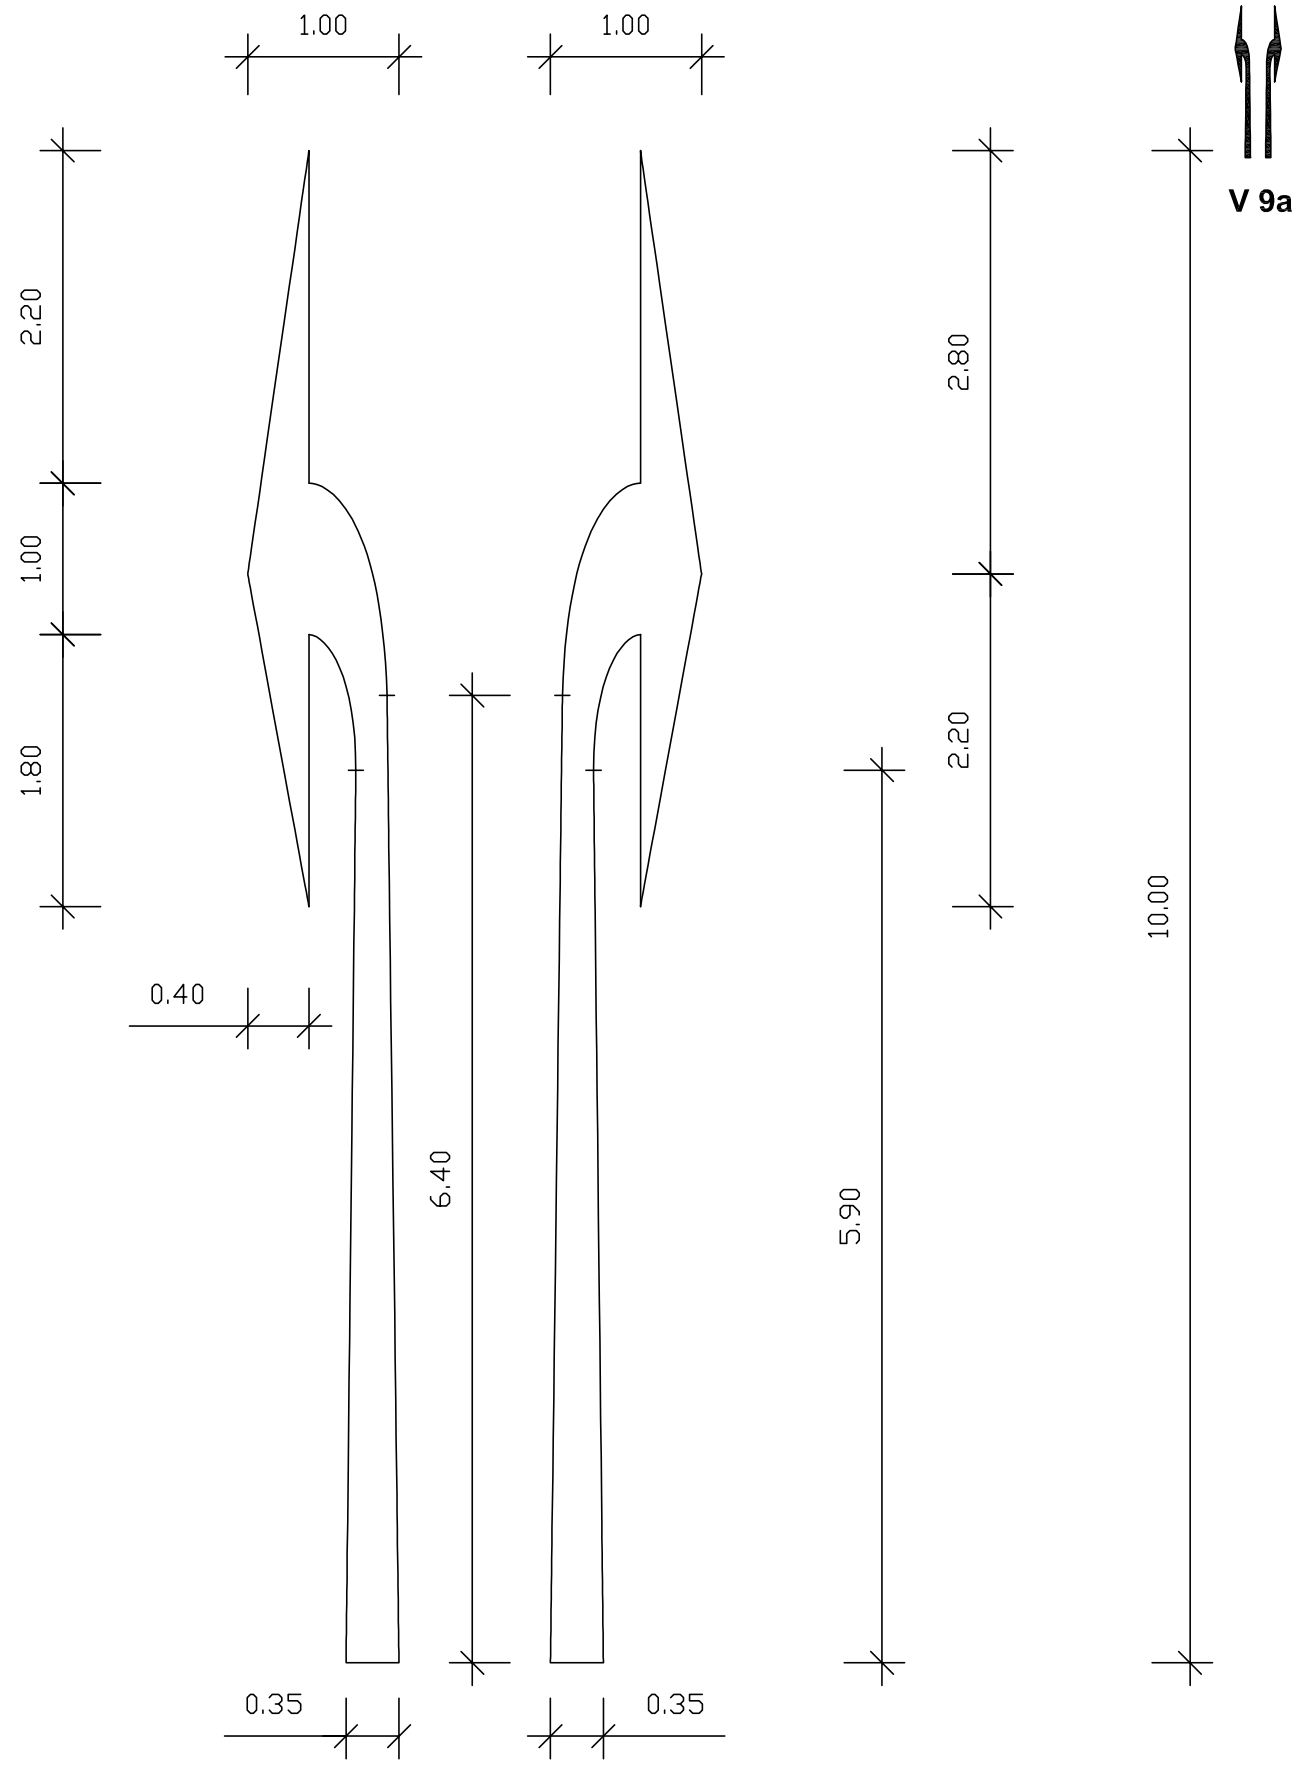


| | | | |
|---|---|---|---|
| **6** **VYBAVENÍ POZEMNÍCH KOMUNIKACÍ**<br>**6.2** **VODOROVNÉ DOPRAVNÍ ZNAČKY**<br>**Šipky**<br>**V 9a Směrové šipky** | **MINISTERSTVO DOPRAVY**<br>**ODBOR POZEMNÍCH KOMUNIKACÍ**<br>**VZOROVÉ LISTY** | **VL 6**<br>**V 9a - 7**<br>**02.17** |

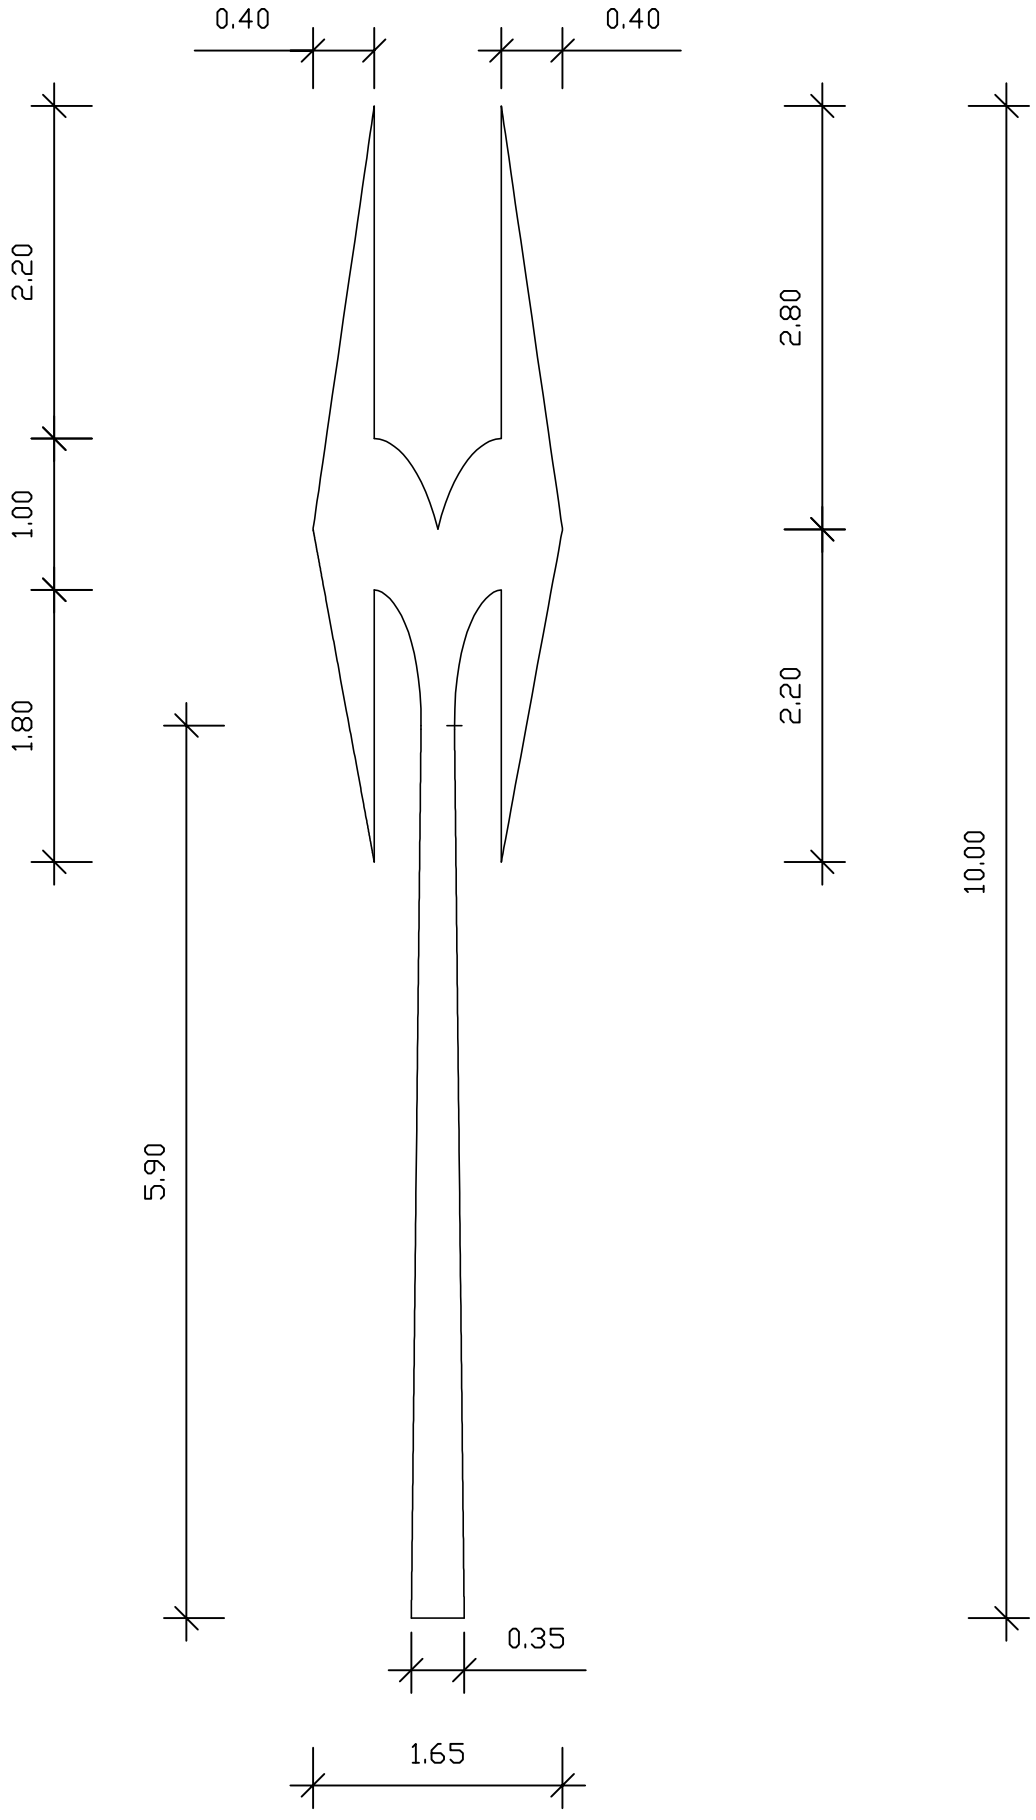





**V 9a**

| | | | |
|---|---|---|---|
| **6** **6.2** **V 9a** | **VYBAVENÍ POZEMNÍCH KOMUNIKACÍ** **VODOROVNÉ DOPRAVNÍ ZNAČKY** **Šipky** **Směrové šipky** | **MINISTERSTVO DOPRAVY** **ODBOR POZEMNÍCH KOMUNIKACÍ** **VZOROVÉ LISTY** | **VL 6** **V 9a - 8** **02.17** |




V 9a

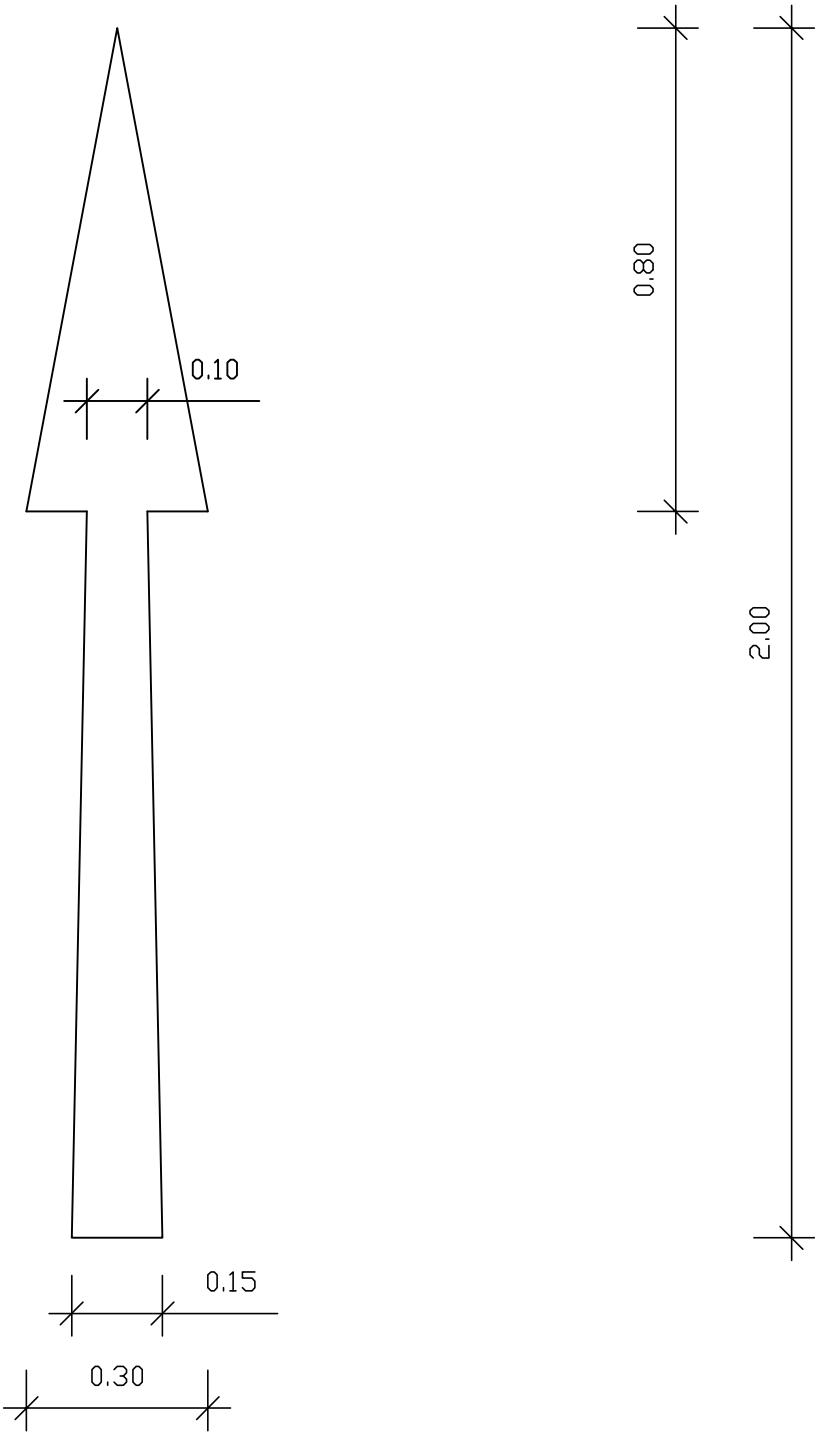



| | | | |
|---|---|---|---|
| 6 VYBAVENÍ POZEMNÍCH KOMUNIKACÍ<br>6.2 VODOROVNÉ DOPRAVNÍ ZNAČKY<br>Šipky<br>V 9a Směrové šipky (pro cyklisty) | MINISTERSTVO DOPRAVY<br>ODBOR POZEMNÍCH KOMUNIKACÍ<br>VZOROVÉ LISTY | VL 6<br>V 9a - 9<br>02.17 |




**V 9a**

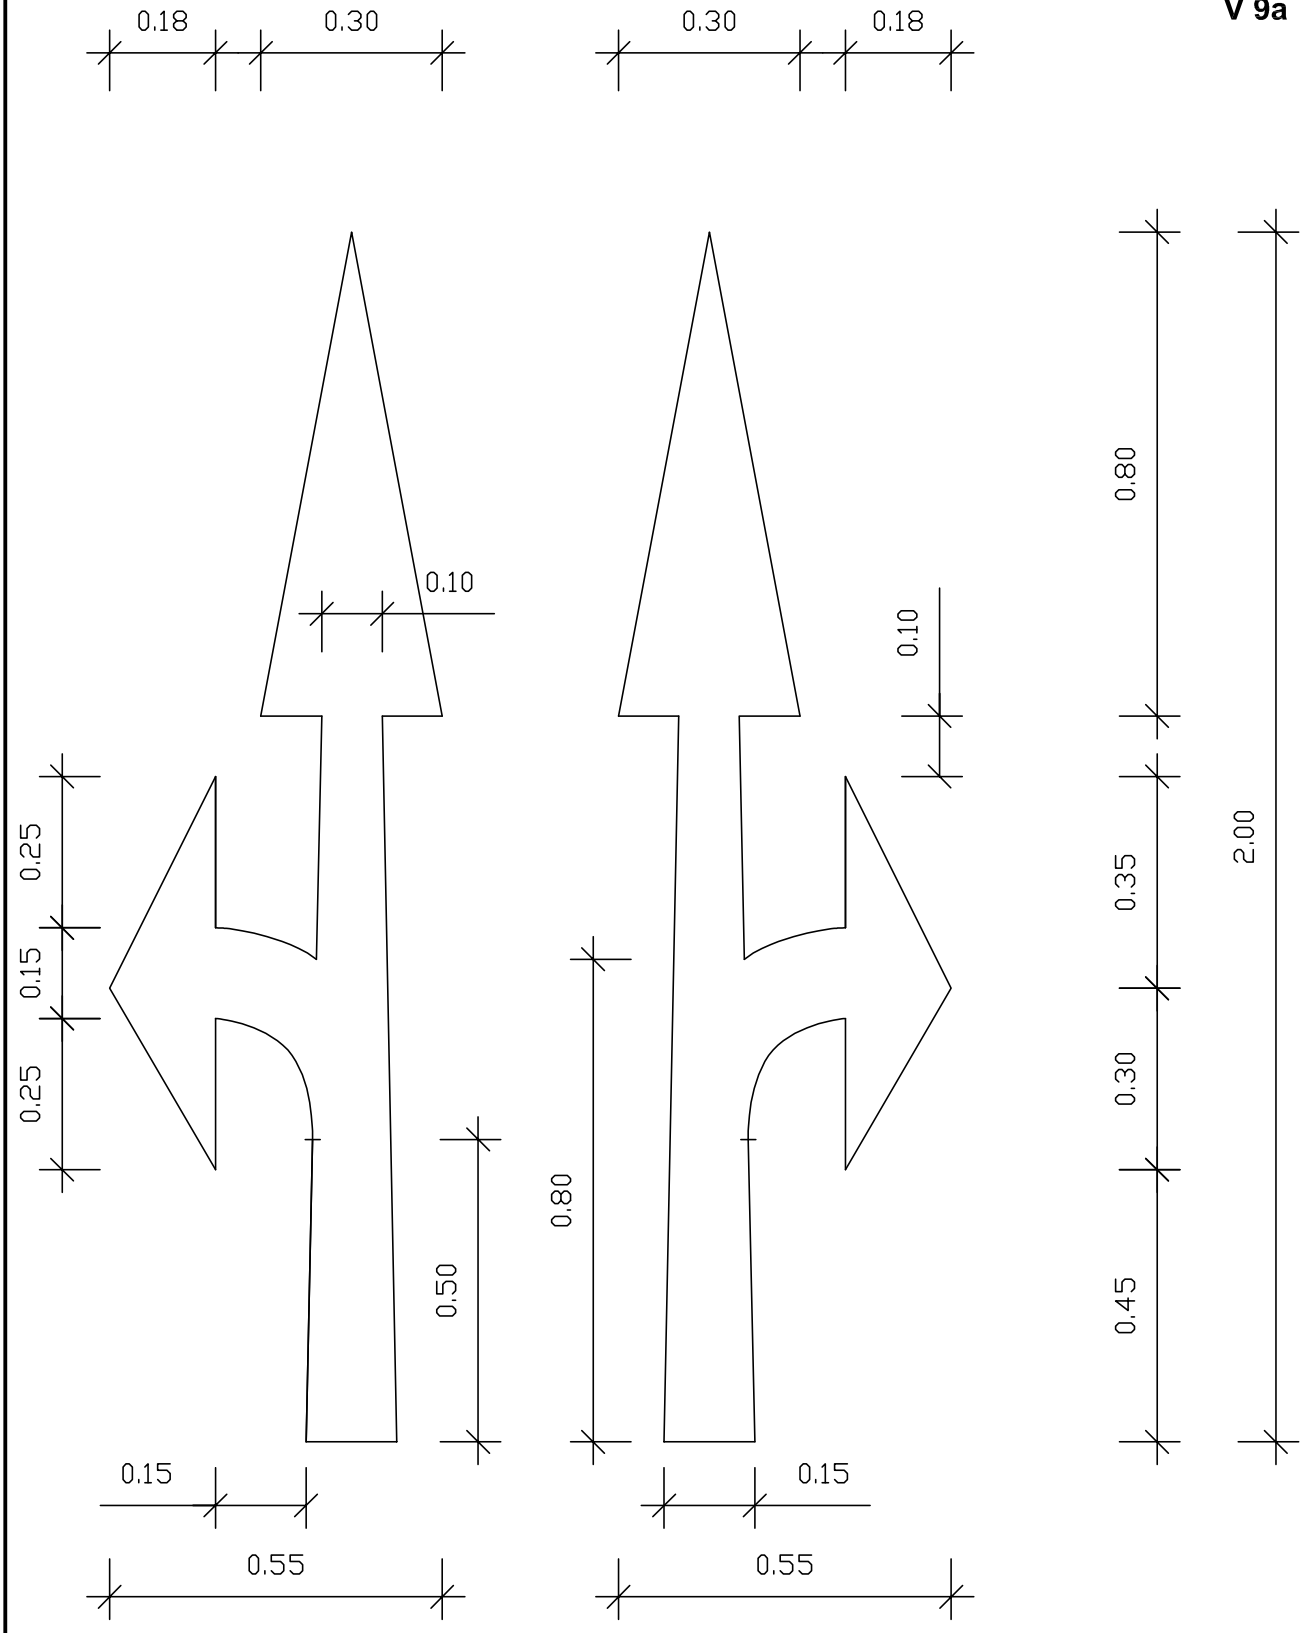


| | | | |
|---|---|---|---|
| **6** **VYBAVENÍ POZEMNÍCH KOMUNIKACÍ**<br>**6.2** **VODOROVNÉ DOPRAVNÍ ZNAČKY**<br>**Šipky**<br>**V 9a Směrové šipky (pro cyklisty)** | **MINISTERSTVO DOPRAVY**<br>**ODBOR POZEMNÍCH KOMUNIKACÍ**<br>**VZOROVÉ LISTY** | **VL 6**<br>**V 9a - 10**<br>02.17 |

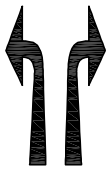


**V 9a**

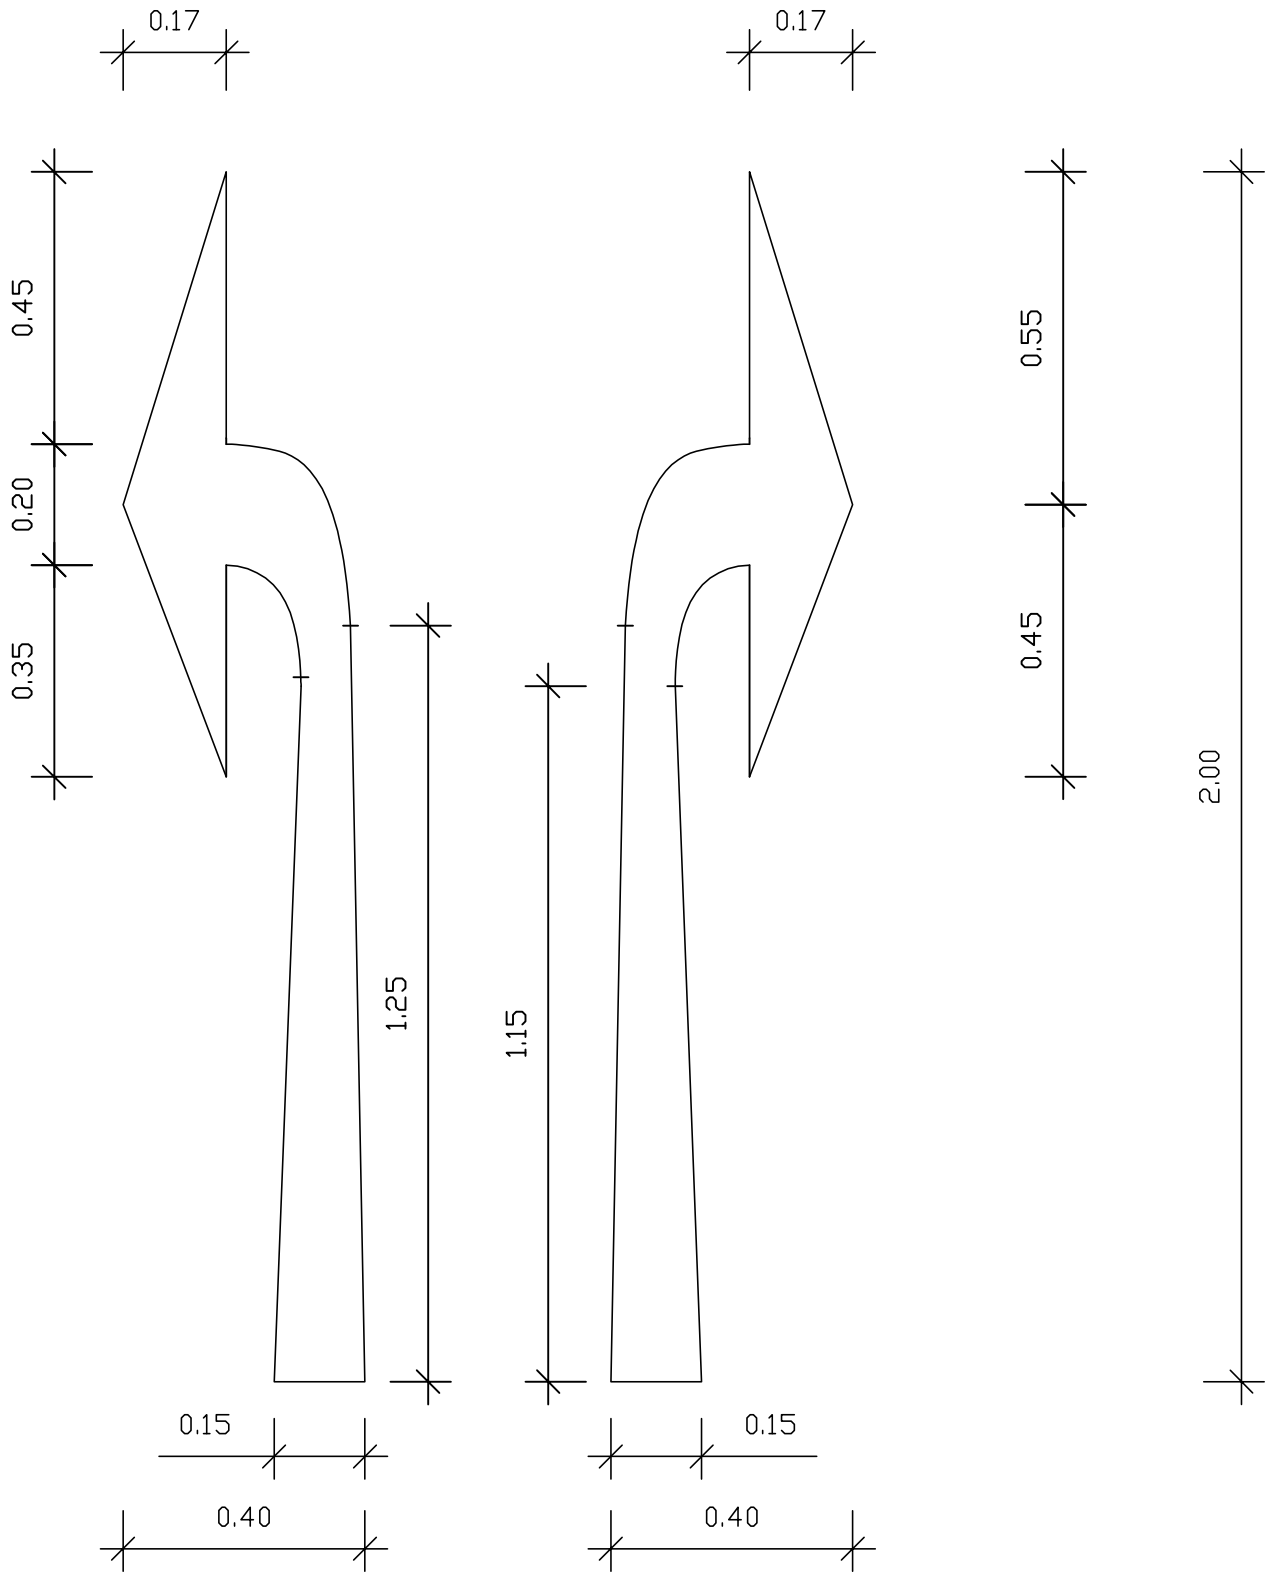



| | | | |
|---|---|---|---|
| **6** **VYBAVENÍ POZEMNÍCH KOMUNIKACÍ**<br>**6.2** **VODOROVNÉ DOPRAVNÍ ZNAČKY**<br>**Šipky**<br>**V 9a Směrové šipky (pro cyklisty)** | **MINISTERSTVO DOPRAVY**<br>**ODBOR POZEMNÍCH KOMUNIKACÍ**<br>**VZOROVÉ LISTY** | **VL 6**<br>**V 9a - 11**<br>02.17 |



**V 9a**

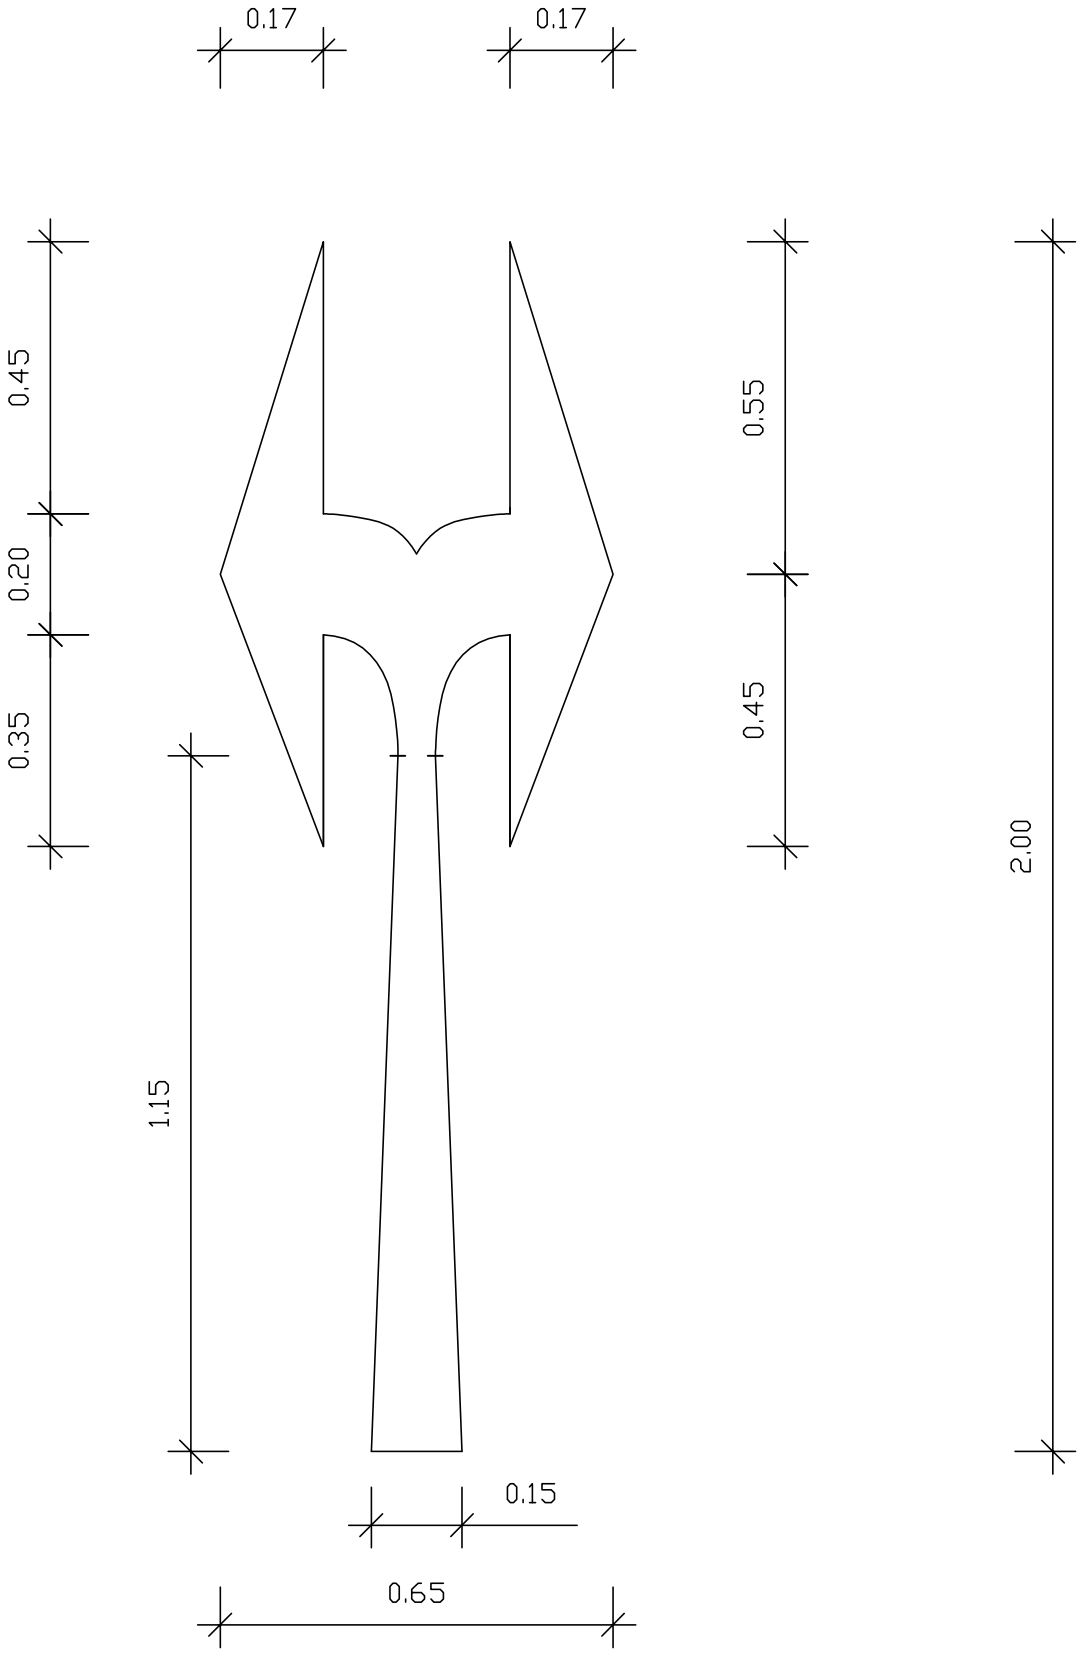



| | | | |
|---|---|---|---|
| **6** **VYBAVENÍ POZEMNÍCH KOMUNIKACÍ**<br>**6.2** **VODOROVNÉ DOPRAVNÍ ZNAČKY**<br>**Šipky**<br>**V 9a Směrové šipky (pro cyklisty)** | **MINISTERSTVO DOPRAVY**<br>**ODBOR POZEMNÍCH KOMUNIKACÍ**<br>**VZOROVÉ LISTY** | **VL 6**<br>**V 9a - 12**<br>02.17 |

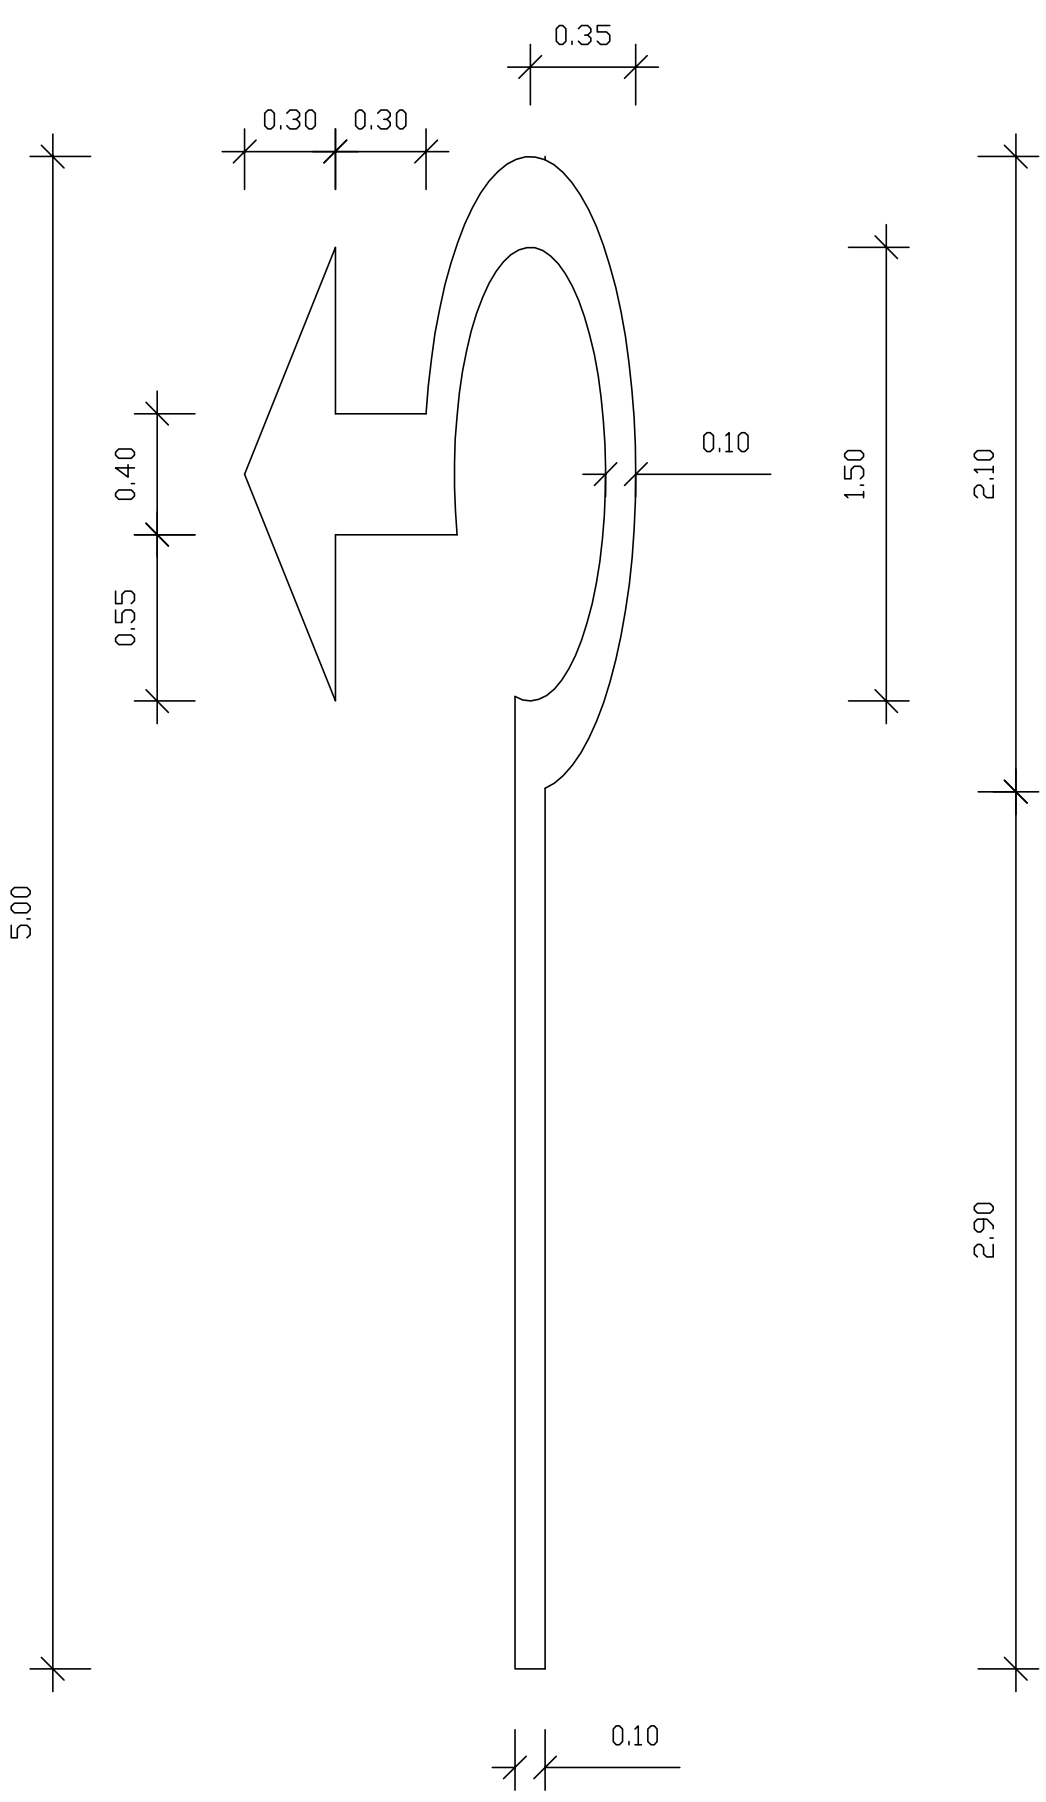





**V 9a**

| | | | |
|---|---|---|---|
| **6** **VYBAVENÍ POZEMNÍCH KOMUNIKACÍ**<br>**6.2** **VODOROVNÉ DOPRAVNÍ ZNAČKY**<br>**Šipky**<br>**V 9a Směrové šipky** | **MINISTERSTVO DOPRAVY**<br>**ODBOR POZEMNÍCH KOMUNIKACÍ**<br>**VZOROVÉ LISTY** | **VL 6**<br>**V 9a - 13**<br>**02.17** |

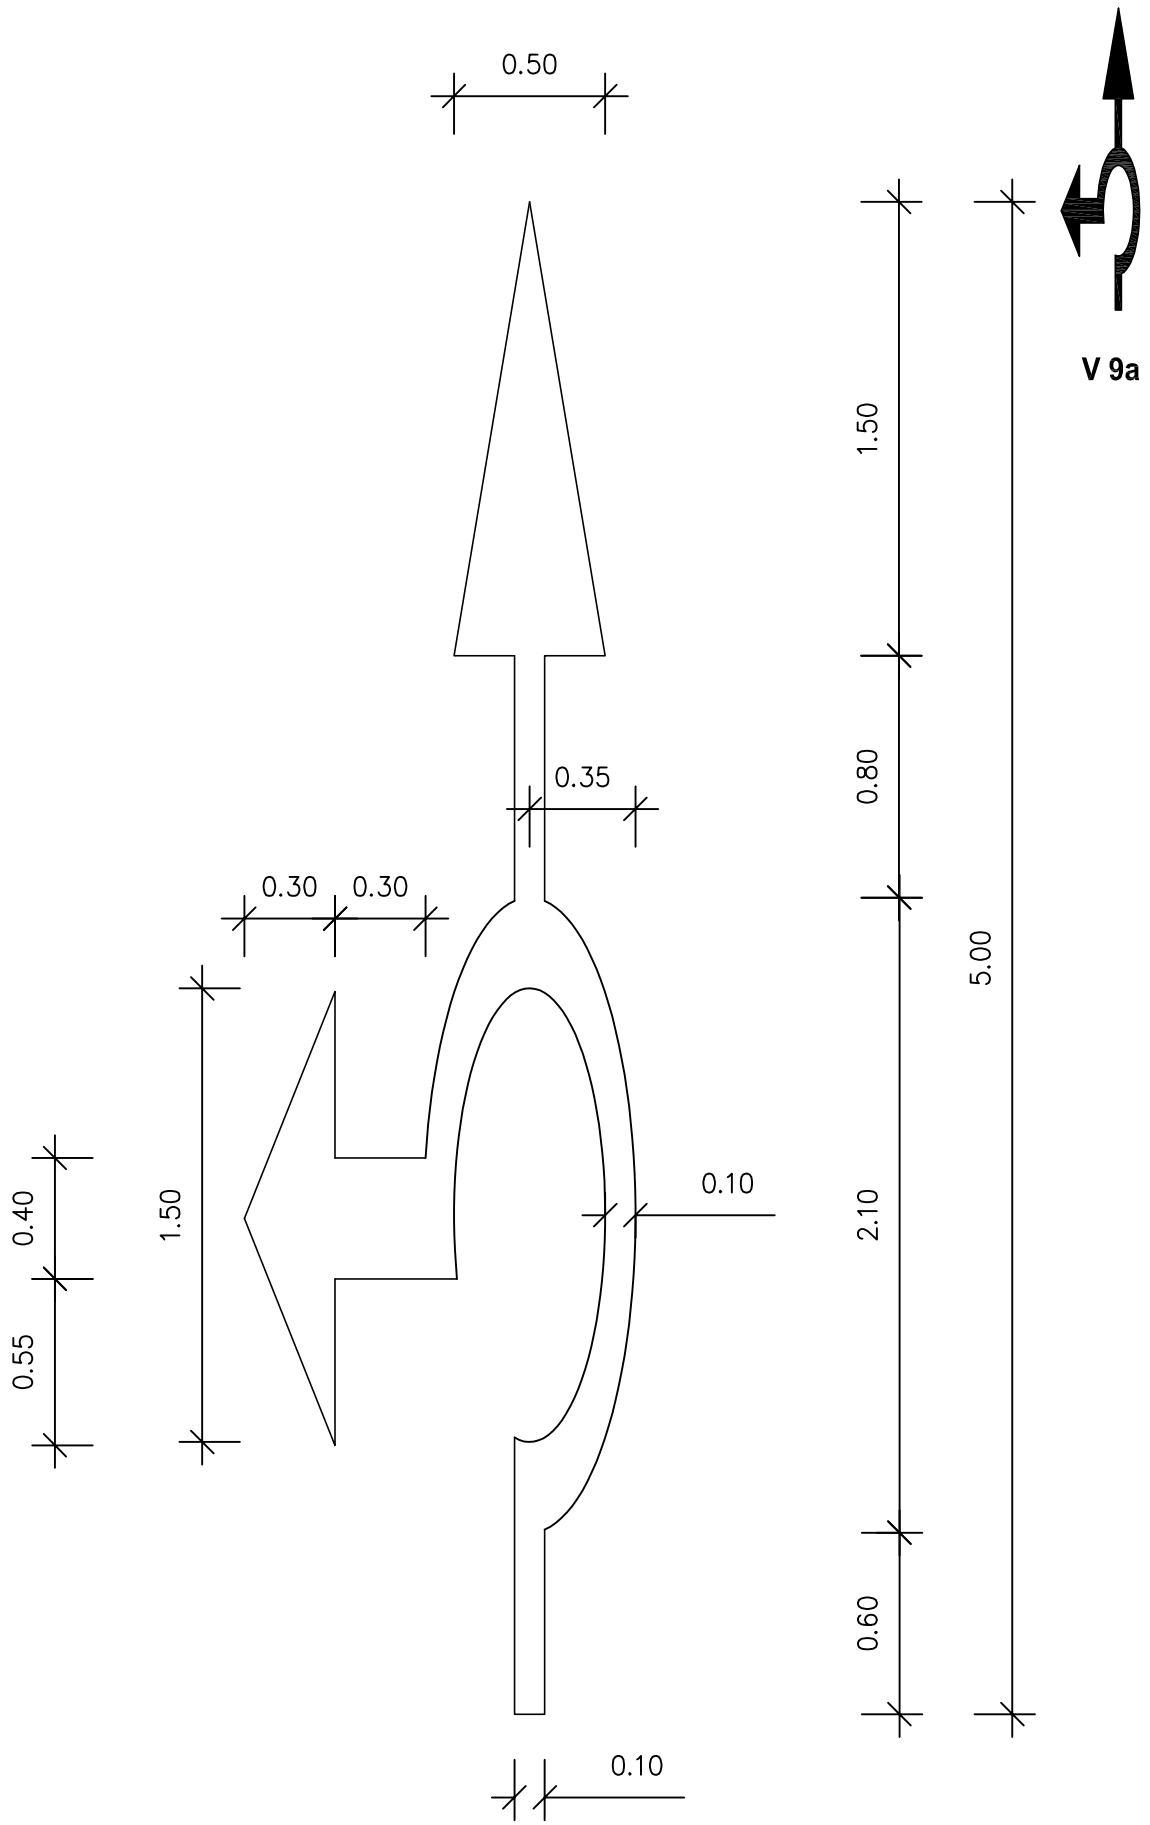



| | | | |
|---|---|---|---|
| **6** **VYBAVENÍ POZEMNÍCH KOMUNIKACÍ**<br>**6.2** **VODOROVNÉ DOPRAVNÍ ZNAČKY**<br>**Šipky**<br>**V 9a** **Směrové šipky** | **MINISTERSTVO DOPRAVY**<br>**ODBOR POZEMNÍCH KOMUNIKACÍ**<br>**VZOROVÉ LISTY** | **VL 6**<br>**V 9a - 14**<br>**02.17** |

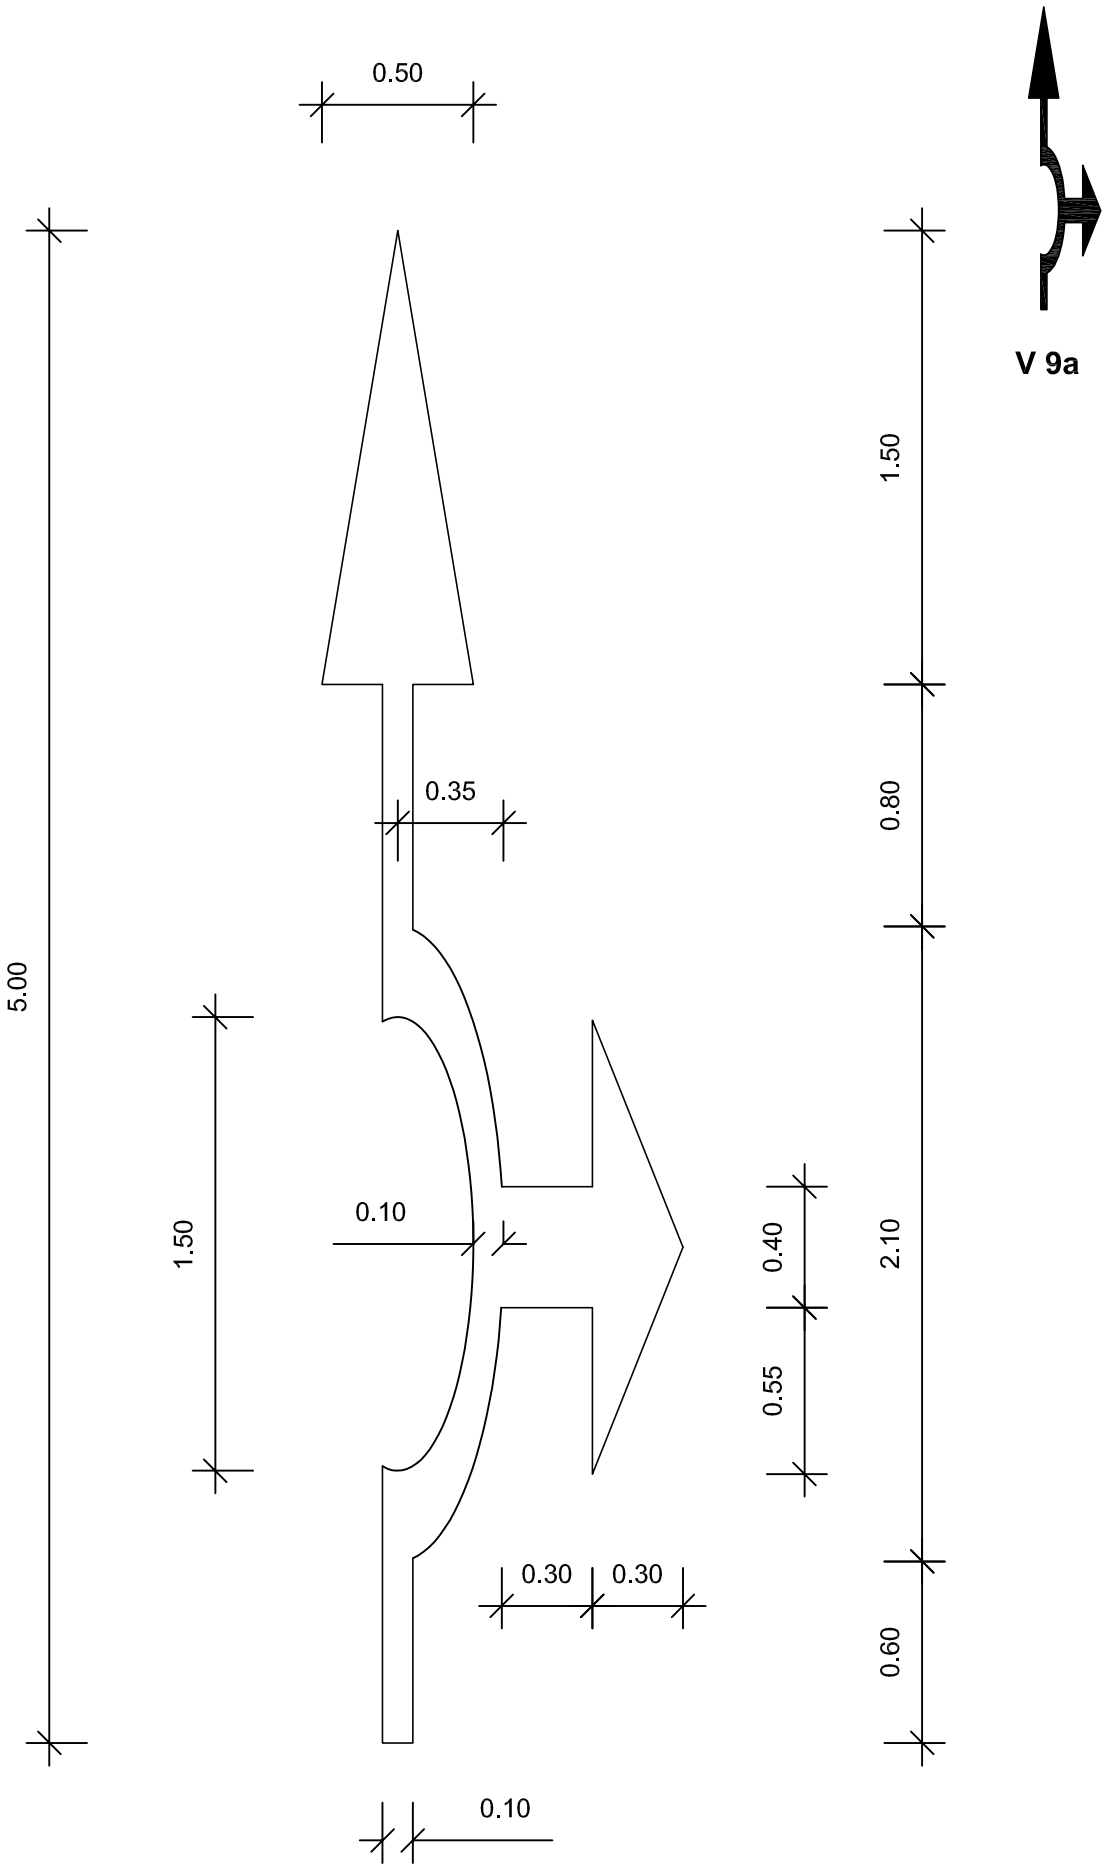


V 9a


| | | | |
|---|---|---|---|
| **6** **VYBAVENÍ POZEMNÍCH KOMUNIKACÍ**<br>**6.2** **VODOROVNÉ DOPRAVNÍ ZNAČKY**<br>**Šipky**<br>**V 9a Směrové šipky** | **MINISTERSTVO DOPRAVY**<br>**ODBOR POZEMNÍCH KOMUNIKACÍ**<br>**VZOROVÉ LISTY** | **VL 6**<br>**V 9a - 15**<br>**02.17** |

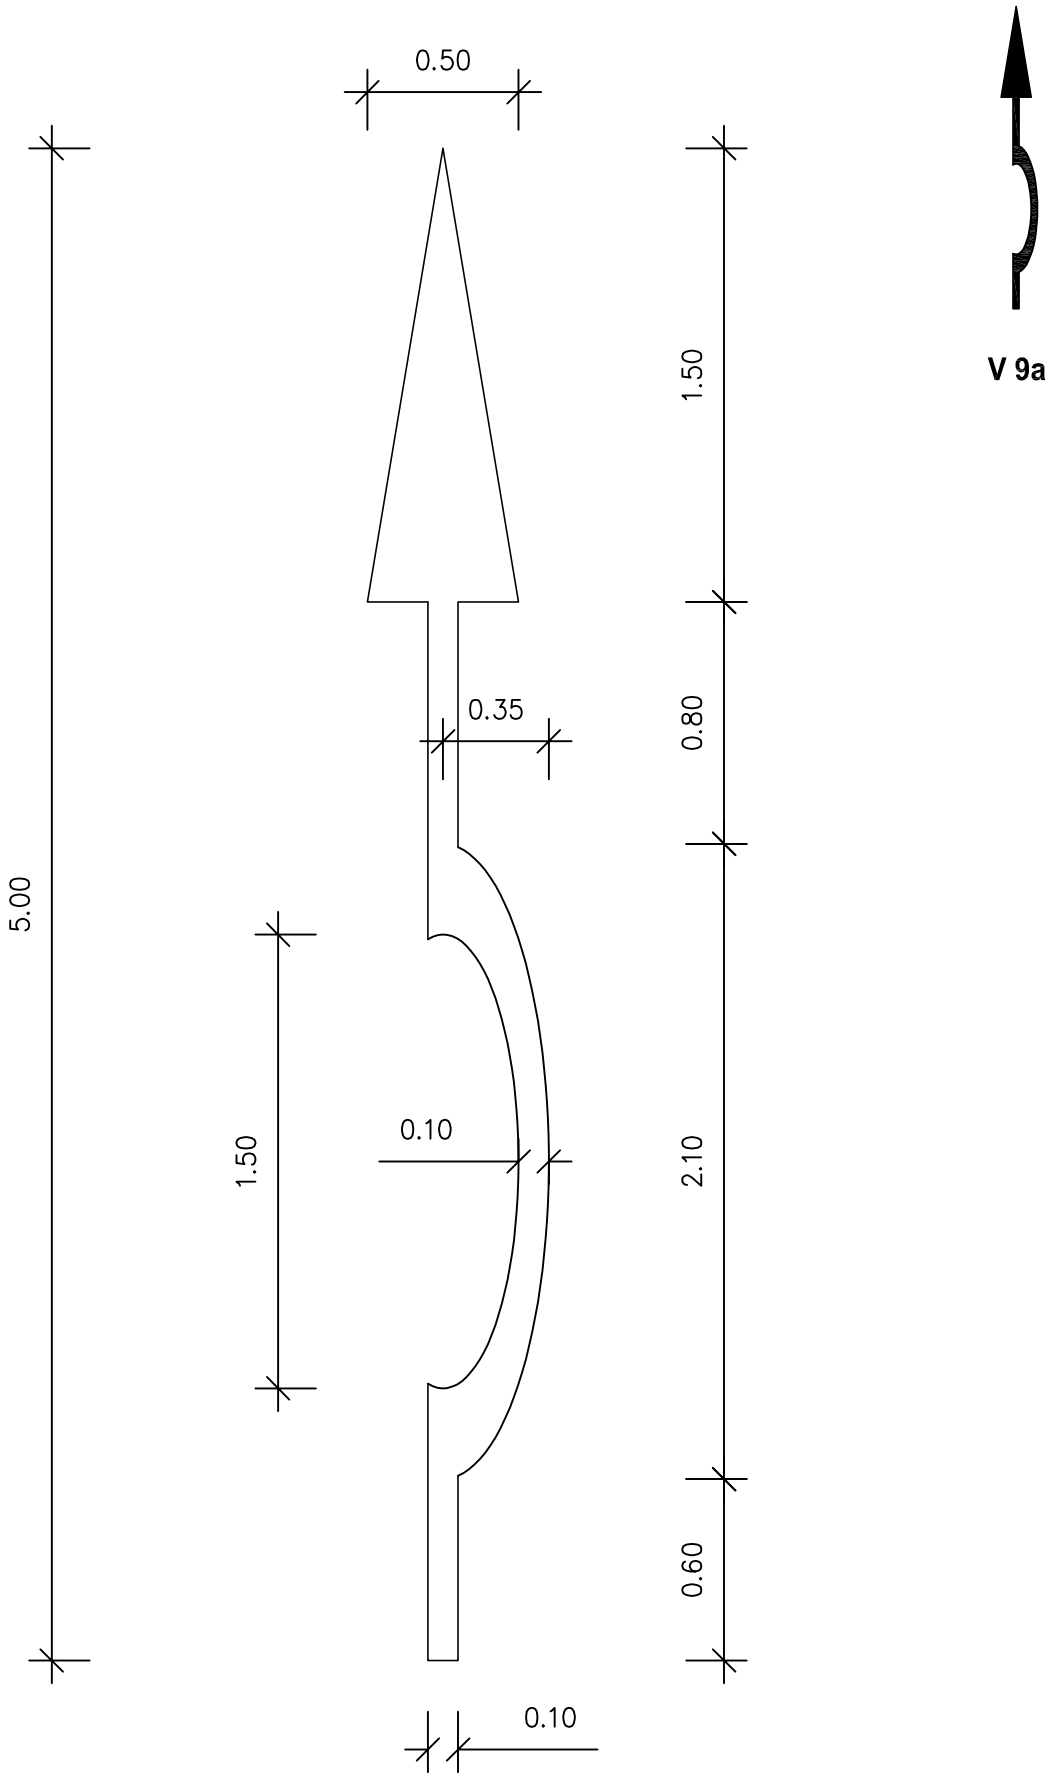




**V 9a**


| | | | |
|---|---|---|---|
| **6** **VYBAVENÍ POZEMNÍCH KOMUNIKACÍ**<br>**6.2** **VODOROVNÉ DOPRAVNÍ ZNAČKY**<br>**Šipky**<br>**V 9a Směrové šipky** | **MINISTERSTVO DOPRAVY**<br>**ODBOR POZEMNÍCH KOMUNIKACÍ**<br>**VZOROVÉ LISTY** | **VL 6**<br>**V 9a - 16**<br>**02.17** |

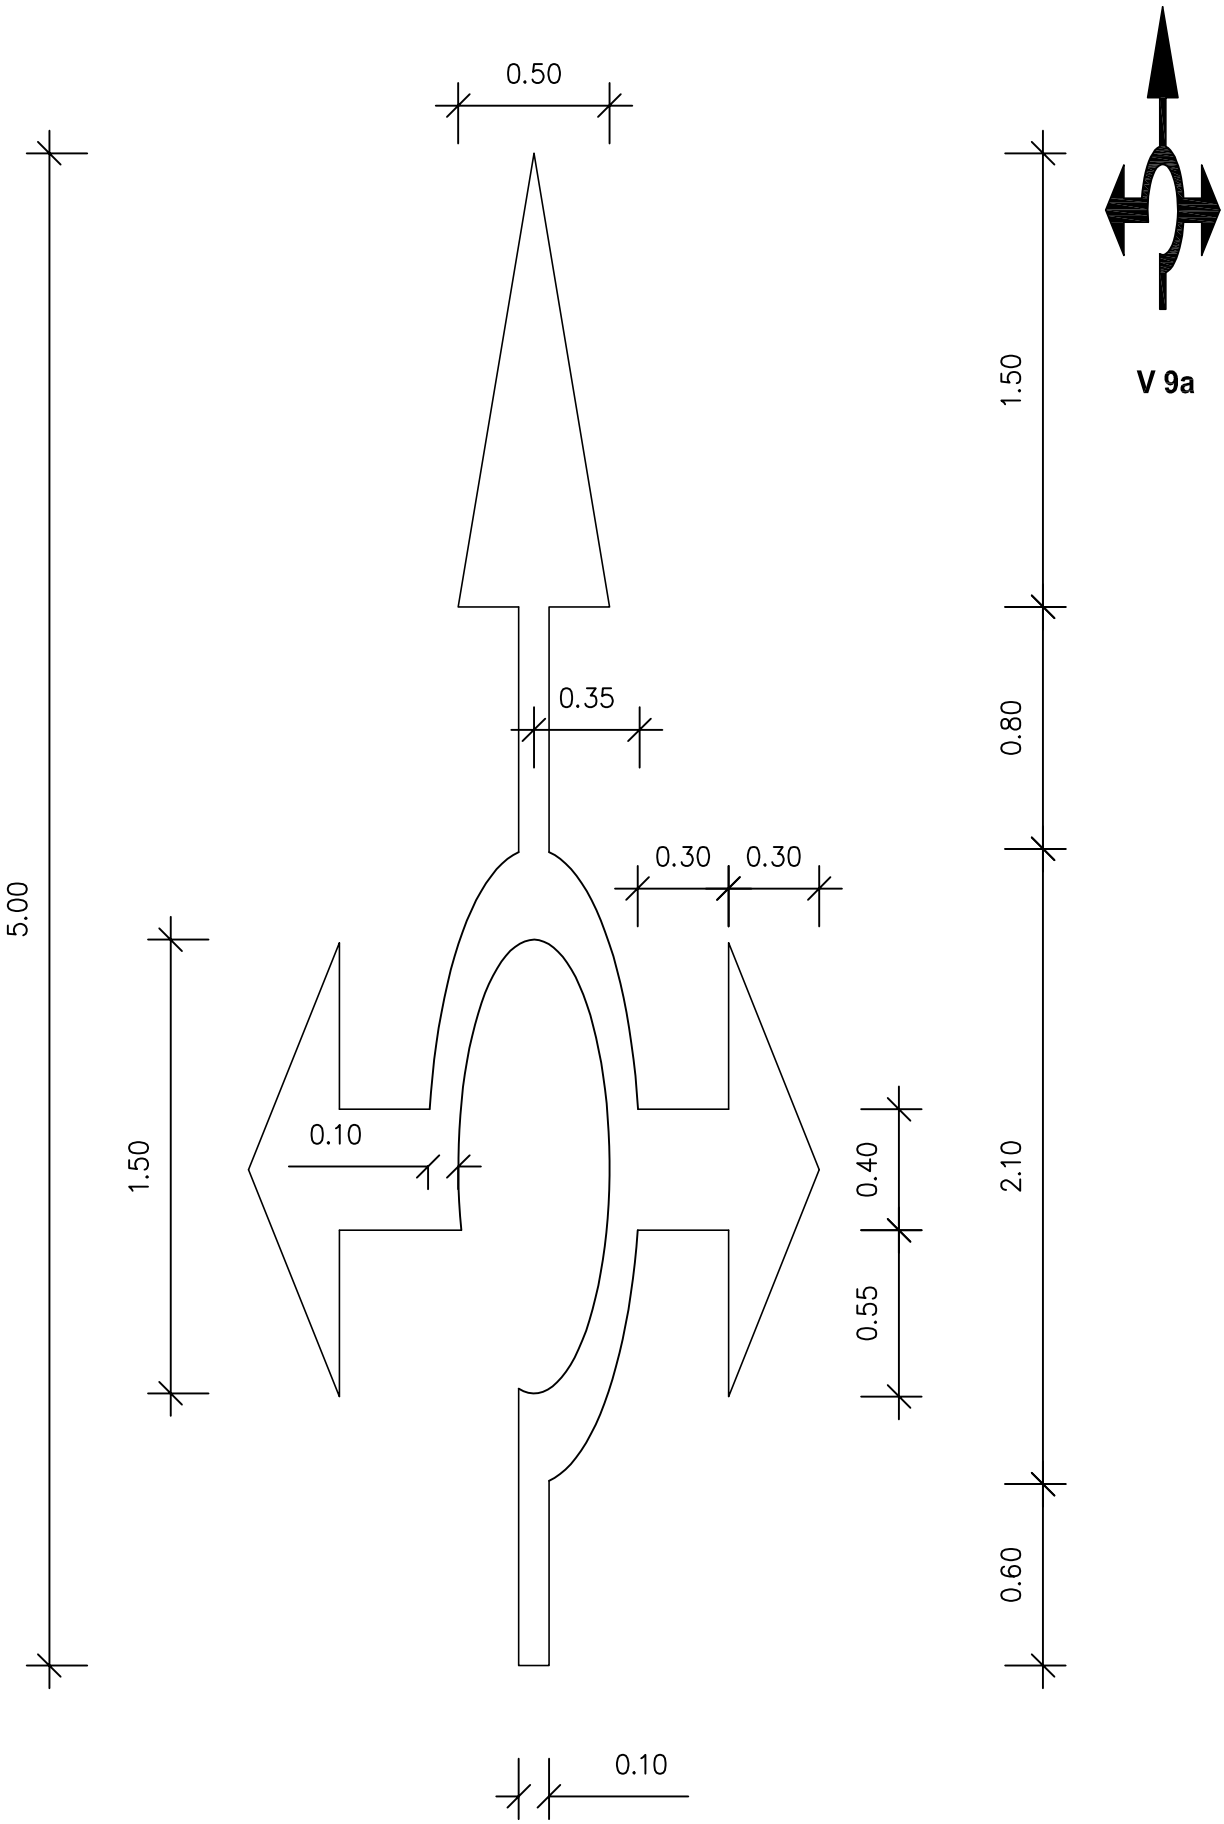




**V 9a**

| | | | |
|---|---|---|---|
| **6** **VYBAVENÍ POZEMNÍCH KOMUNIKACÍ**<br>**6.2** **VODOROVNÉ DOPRAVNÍ ZNAČKY**<br>**Šipky**<br>**V 9a Směrové šipky** | **MINISTERSTVO DOPRAVY**<br>**ODBOR POZEMNÍCH KOMUNIKACÍ**<br>**VZOROVÉ LISTY** | **VL 6**<br>**V 9a - 17**<br>**02.17** |

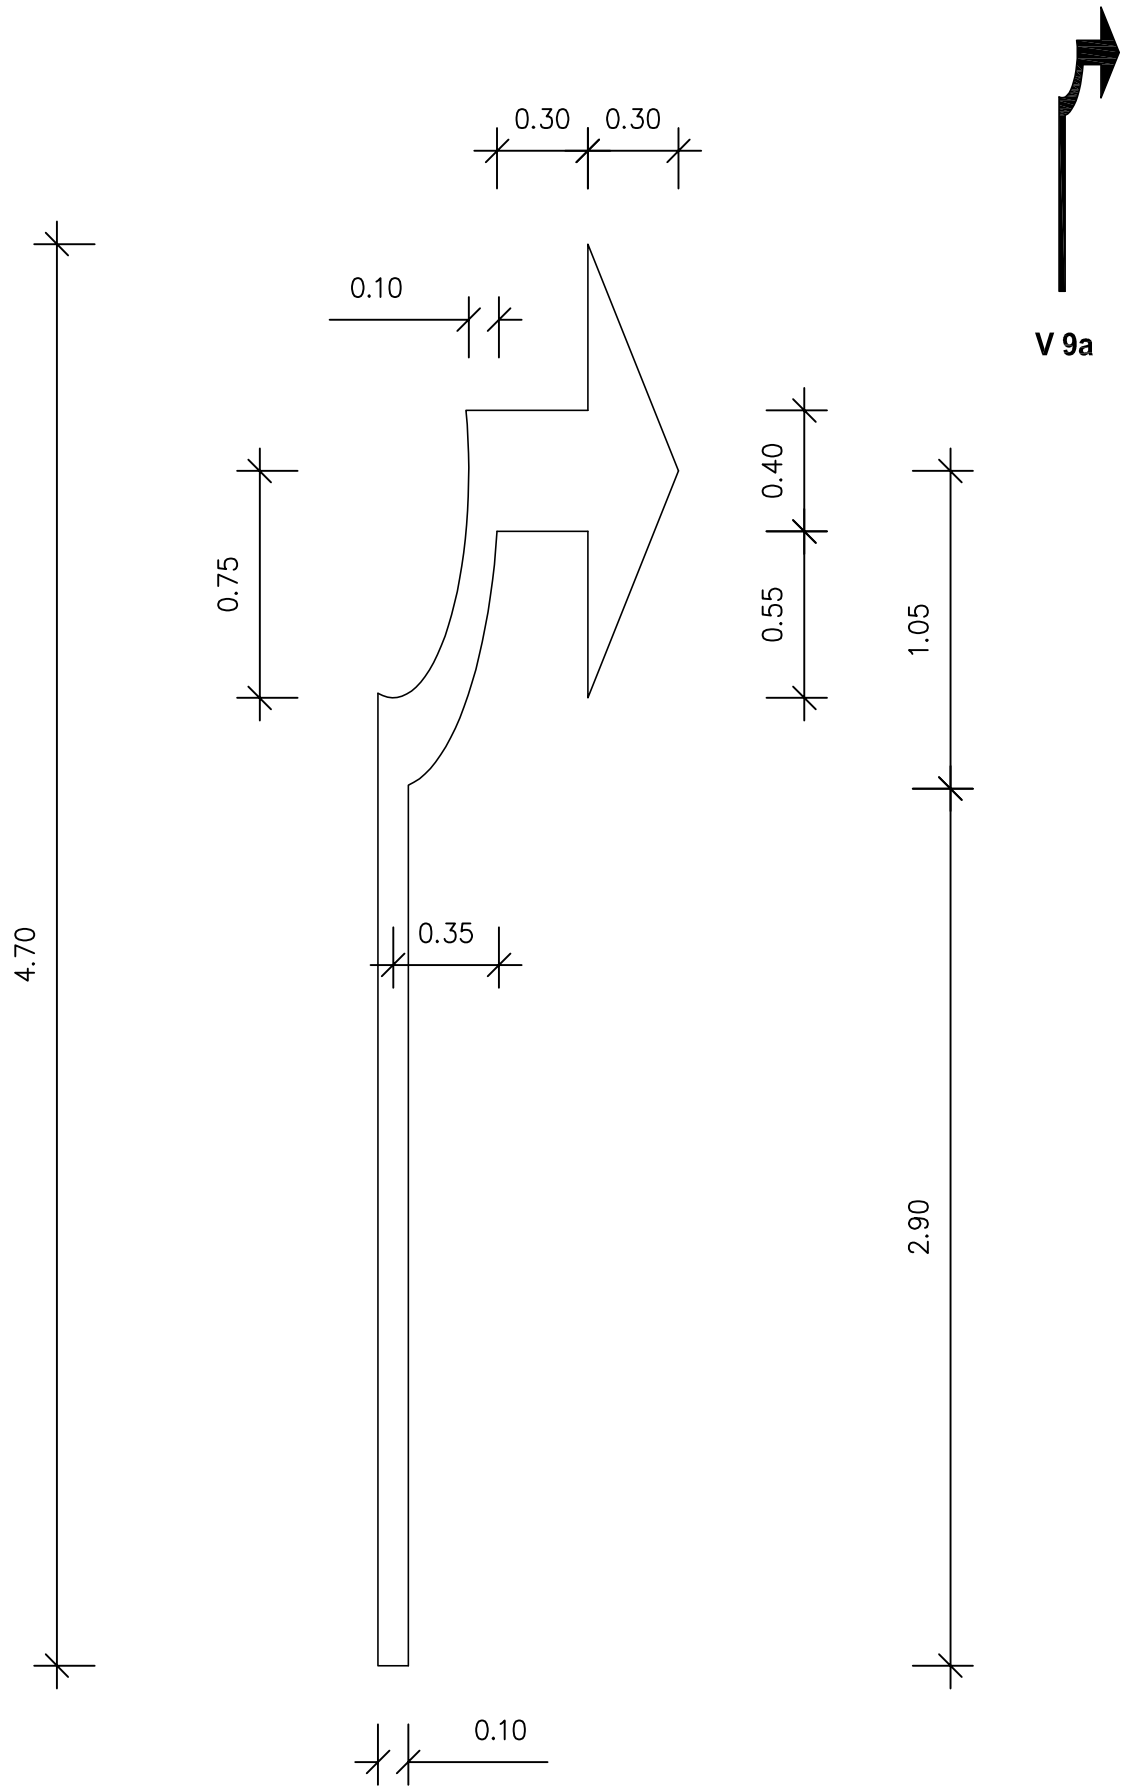





**V 9a**


| | | | |
|---|---|---|---|
| **6** **VYBAVENÍ POZEMNÍCH KOMUNIKACÍ**<br>**6.2** **VODOROVNÉ DOPRAVNÍ ZNAČKY**<br>**Šipky**<br>**V 9a Směrové šipky** | **MINISTERSTVO DOPRAVY**<br>**ODBOR POZEMNÍCH KOMUNIKACÍ**<br>**VZOROVÉ LISTY** | **VL 6**<br>**V 9a - 18**<br>**02.17** |




**V 9b**

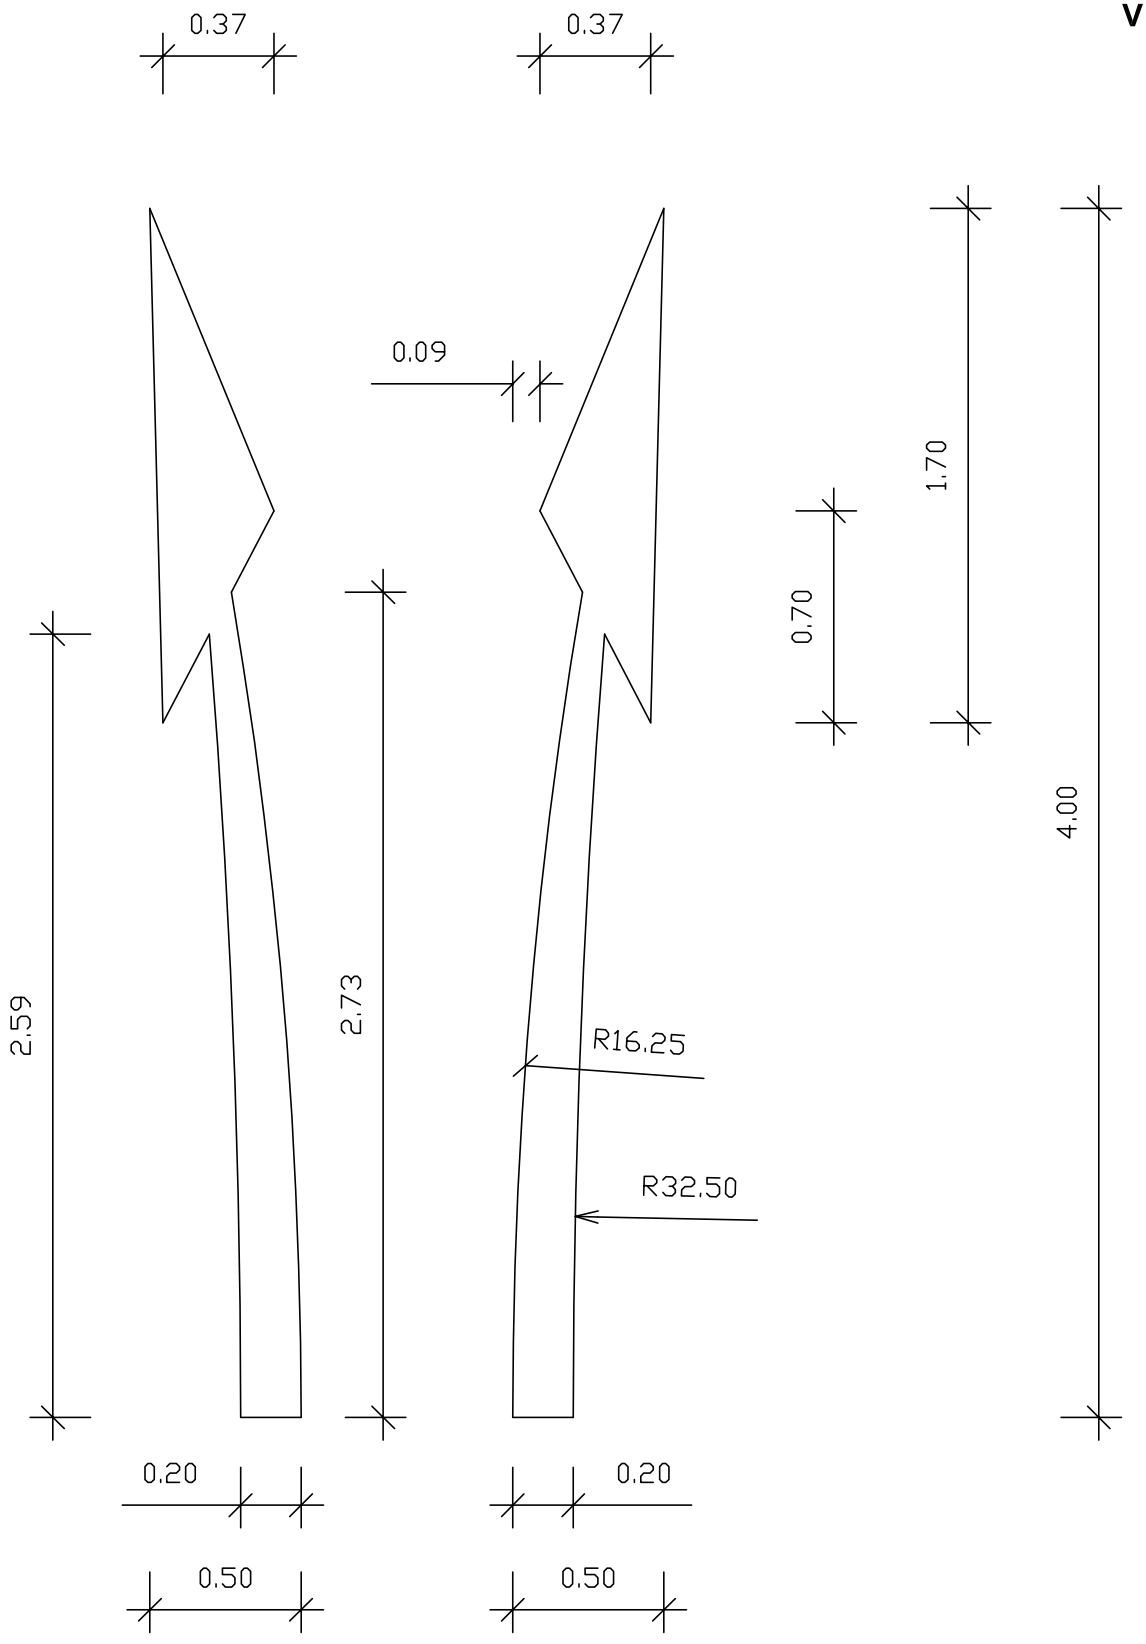


| | | | |
|---|---|---|---|
| **6** **VYBAVENÍ POZEMNÍCH KOMUNIKACÍ**<br>**6.2** **VODOROVNÉ DOPRAVNÍ ZNAČKY**<br>**Šipky**<br>**V 9b Předběžné šipky** | **MINISTERSTVO DOPRAVY**<br>**ODBOR POZEMNÍCH KOMUNIKACÍ**<br>**VZOROVÉ LISTY** | **VL 6**<br>**V 9b**<br>**02.17** |

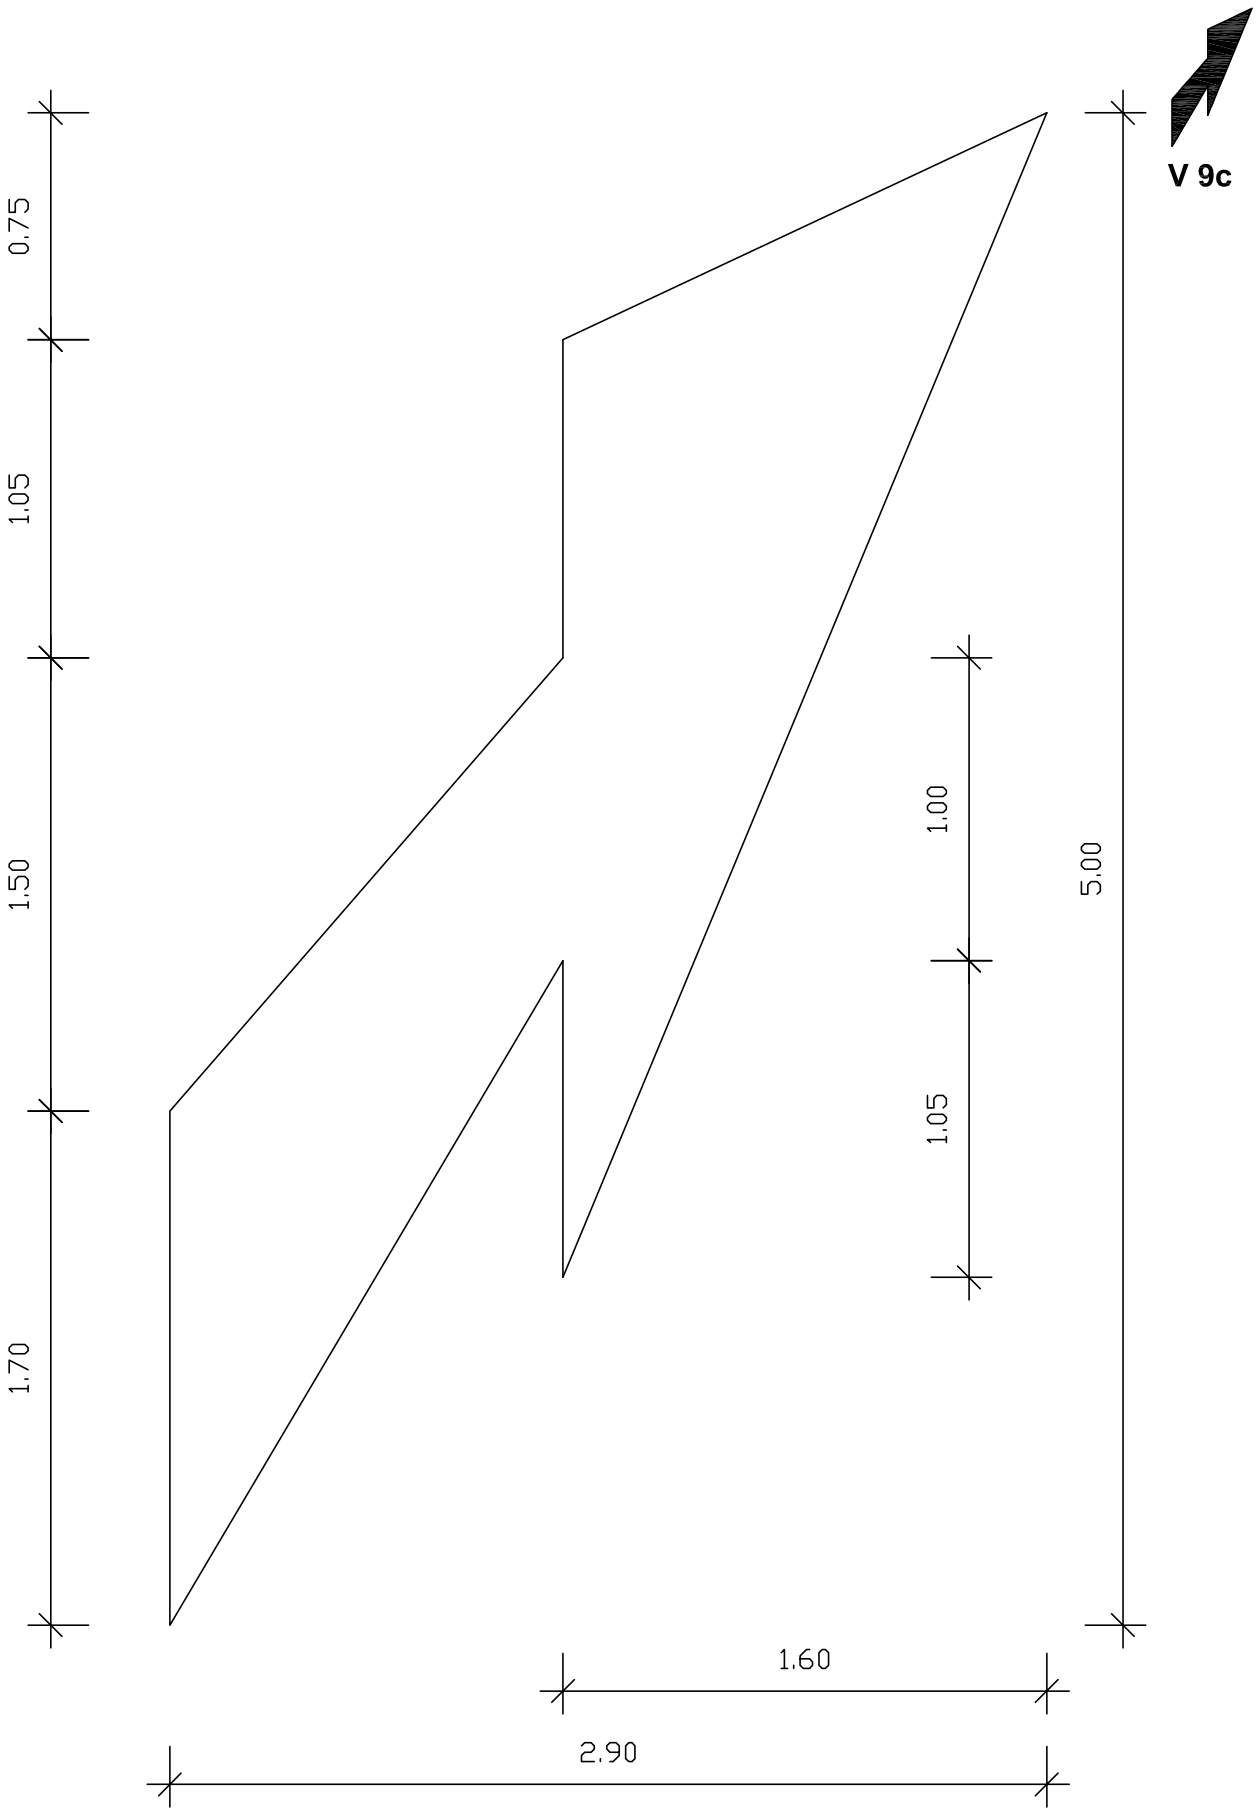


| | | | |
|---|---|---|---|
| **6** **VYBAVENÍ POZEMNÍCH KOMUNIKACÍ**<br>**6.2** **VODOROVNÉ DOPRAVNÍ ZNAČKY**<br>**Šipky**<br>**V 9c Předběžné šipky** | **MINISTERSTVO DOPRAVY**<br>**ODBOR POZEMNÍCH KOMUNIKACÍ**<br>**VZOROVÉ LISTY** | **VL 6**<br>**V 9c - 1**<br>**02.17** |

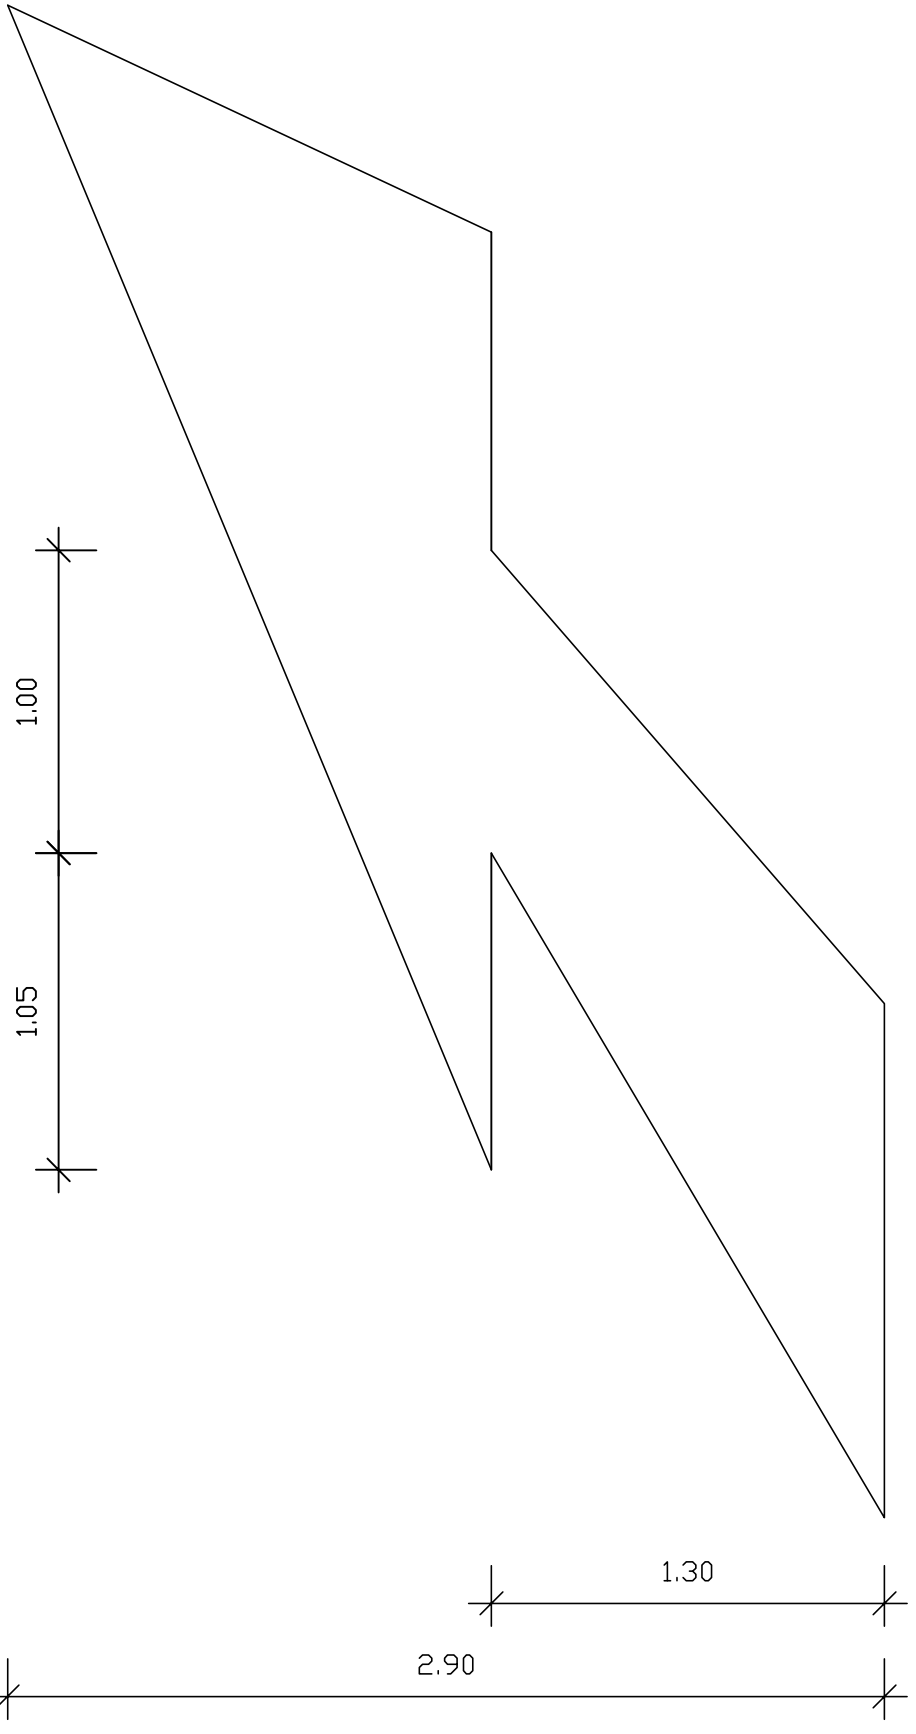



V 9c

| | | |
|---|---|---|
| **6 VYBAVENÍ POZEMNÍCH KOMUNIKACÍ**<br>**6.2 VODOROVNÉ DOPRAVNÍ ZNAČKY**<br>**Šipky**<br>**V 9c Předběžné šipky** | **MINISTERSTVO DOPRAVY**<br>**ODBOR POZEMNÍCH KOMUNIKACÍ**<br>**VZOROVÉ LISTY** | **VL 6**<br>**V 9c - 2**<br>**02.17** |

ABC


V 15

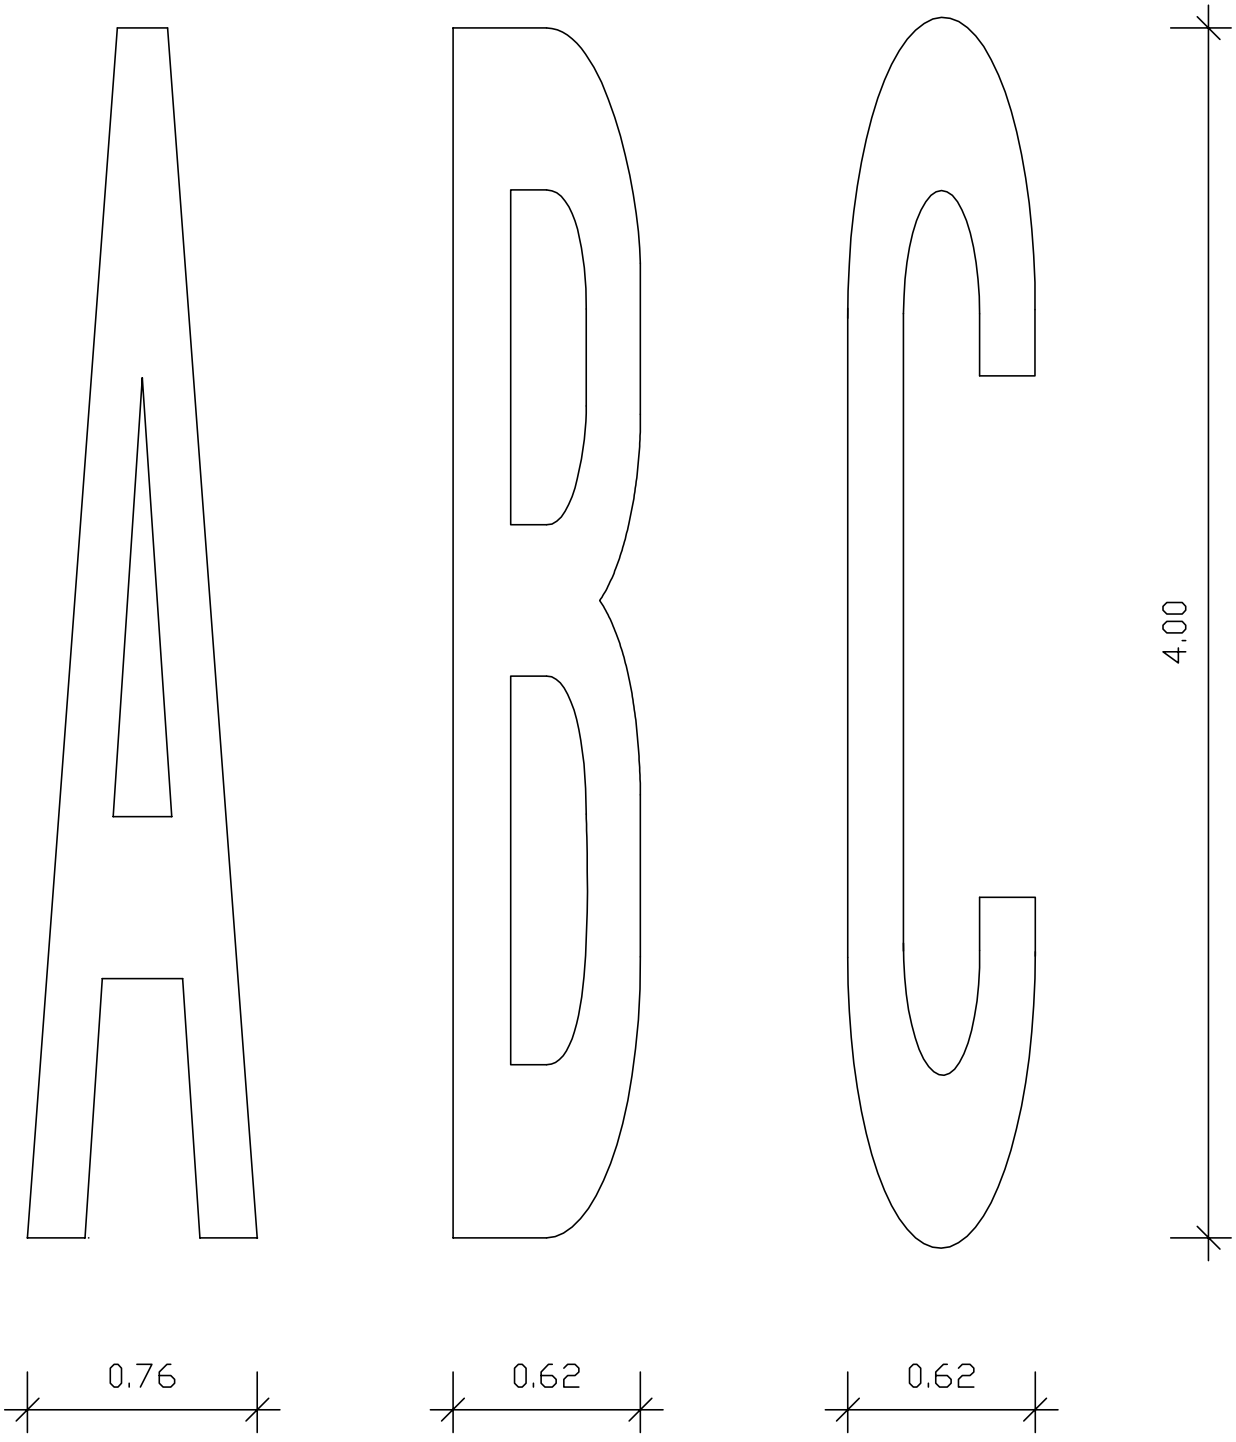


| | | | |
|---|---|---|---|
| 6<br>6.2<br>Písmo<br>Písmena | VYBAVENÍ POZEMNÍCH KOMUNIKACÍ<br>VODOROVNÉ DOPRAVNÍ ZNAČKY | MINISTERSTVO DOPRAVY<br>ODBOR POZEMNÍCH KOMUNIKACÍ<br>VZOROVÉ LISTY | VL 6<br>V 15 - 1<br>02.17 |

DEF


V 15

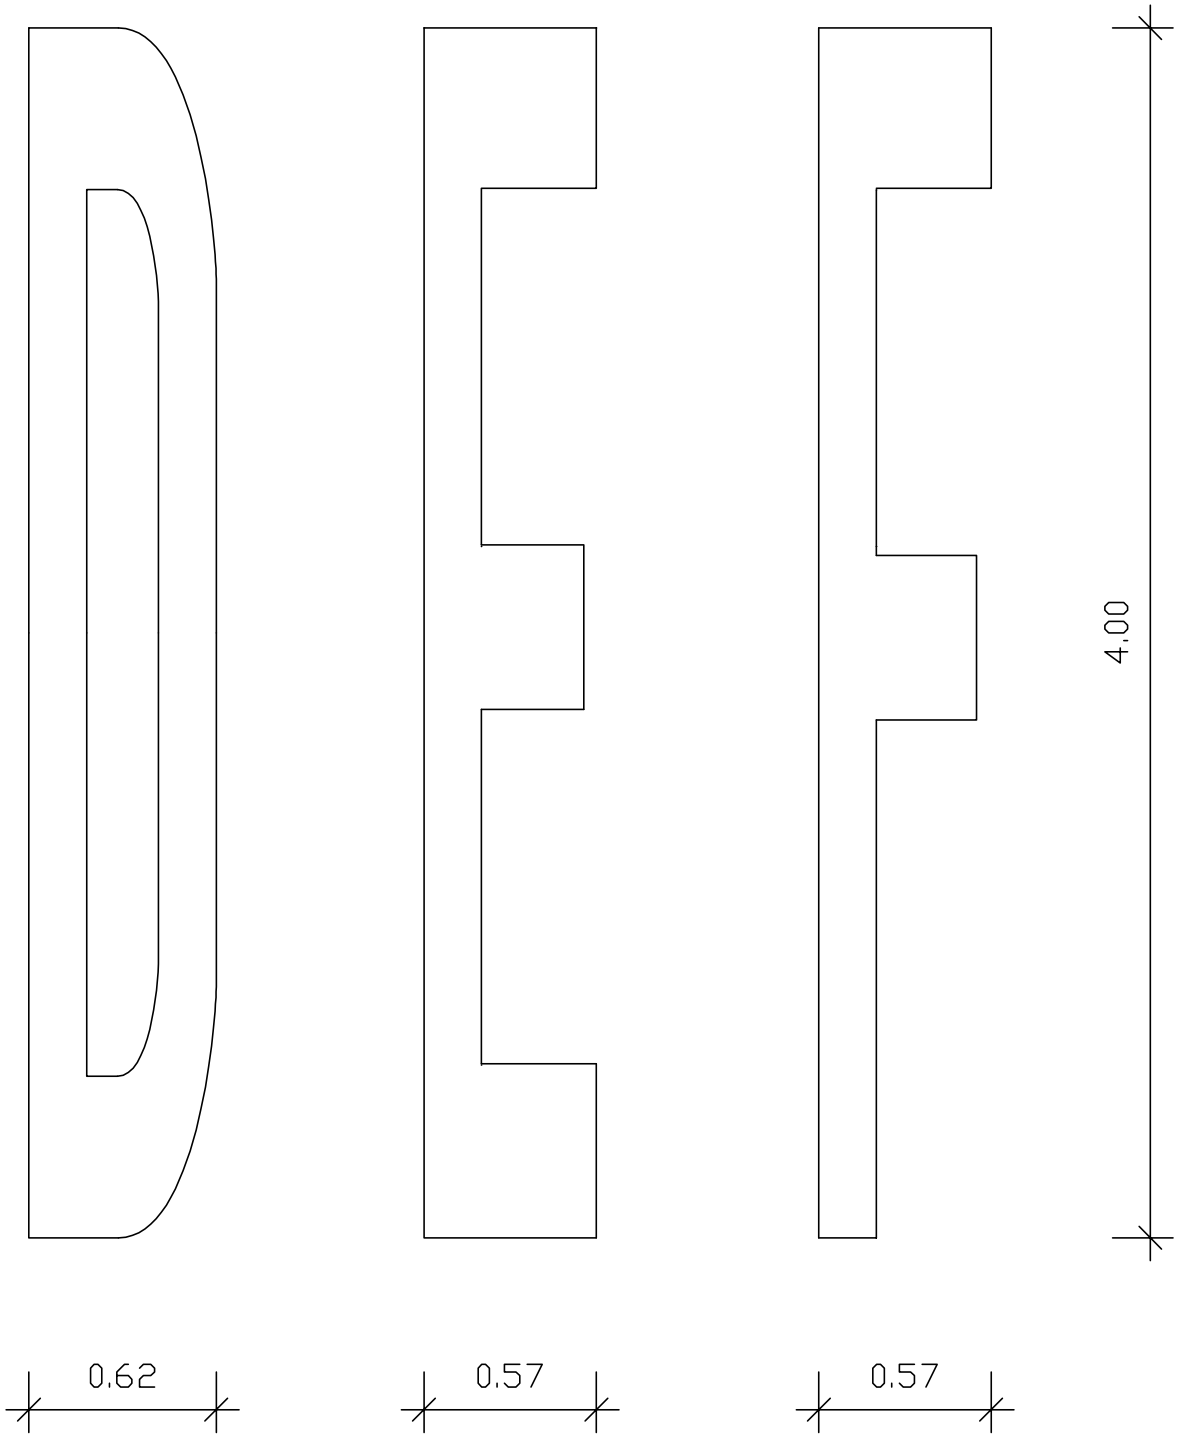


| | | | |
|---|---|---|---|
| 6<br>6.2 | VYBAVENÍ POZEMNÍCH KOMUNIKACÍ<br>VODOROVNÉ DOPRAVNÍ ZNAČKY<br>Písmo<br>Písmena | MINISTERSTVO DOPRAVY<br>ODBOR POZEMNÍCH KOMUNIKACÍ<br>VZOROVÉ LISTY | VL 6<br>V 15 - 2<br>02.17 |

GHI


V 15

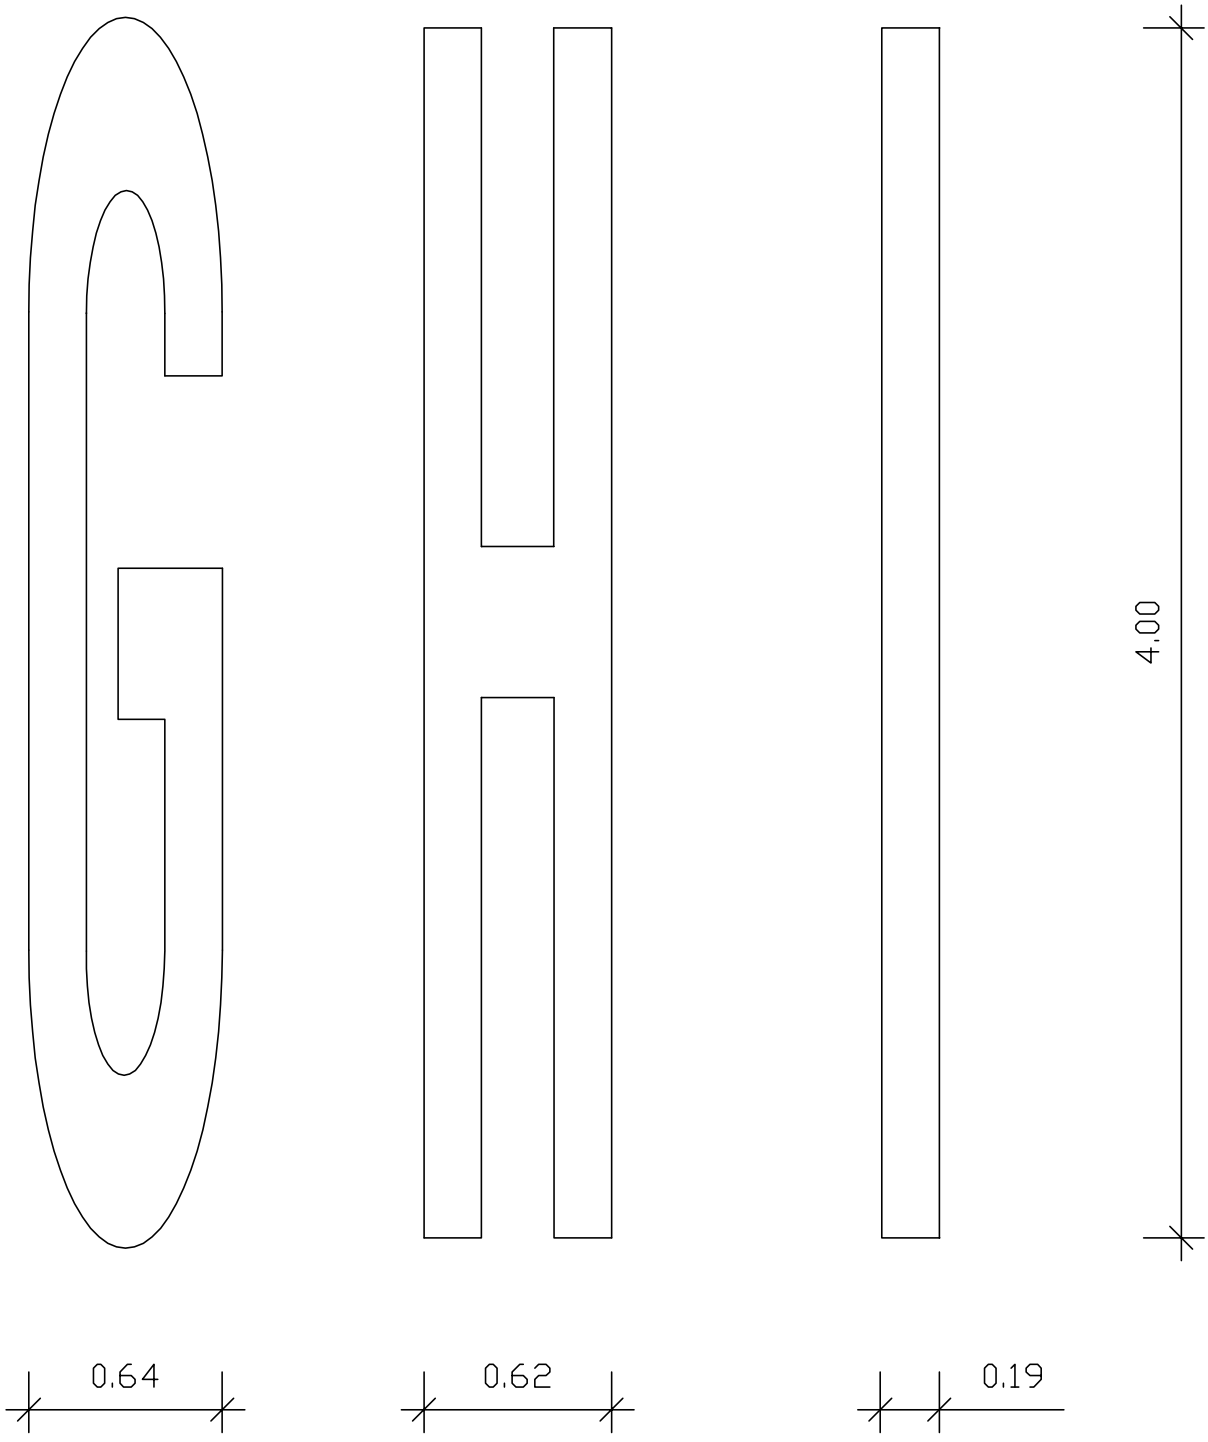


| | | | |
|---|---|---|---|
| 6<br>6.2 | VYBAVENÍ POZEMNÍCH KOMUNIKACÍ<br>VODOROVNÉ DOPRAVNÍ ZNAČKY<br>Písmo<br>Písmena | MINISTERSTVO DOPRAVY<br>ODBOR POZEMNÍCH KOMUNIKACÍ<br>VZOROVÉ LISTY | VL 6<br>V 15 - 3<br>02.17 |

JKL


V 15

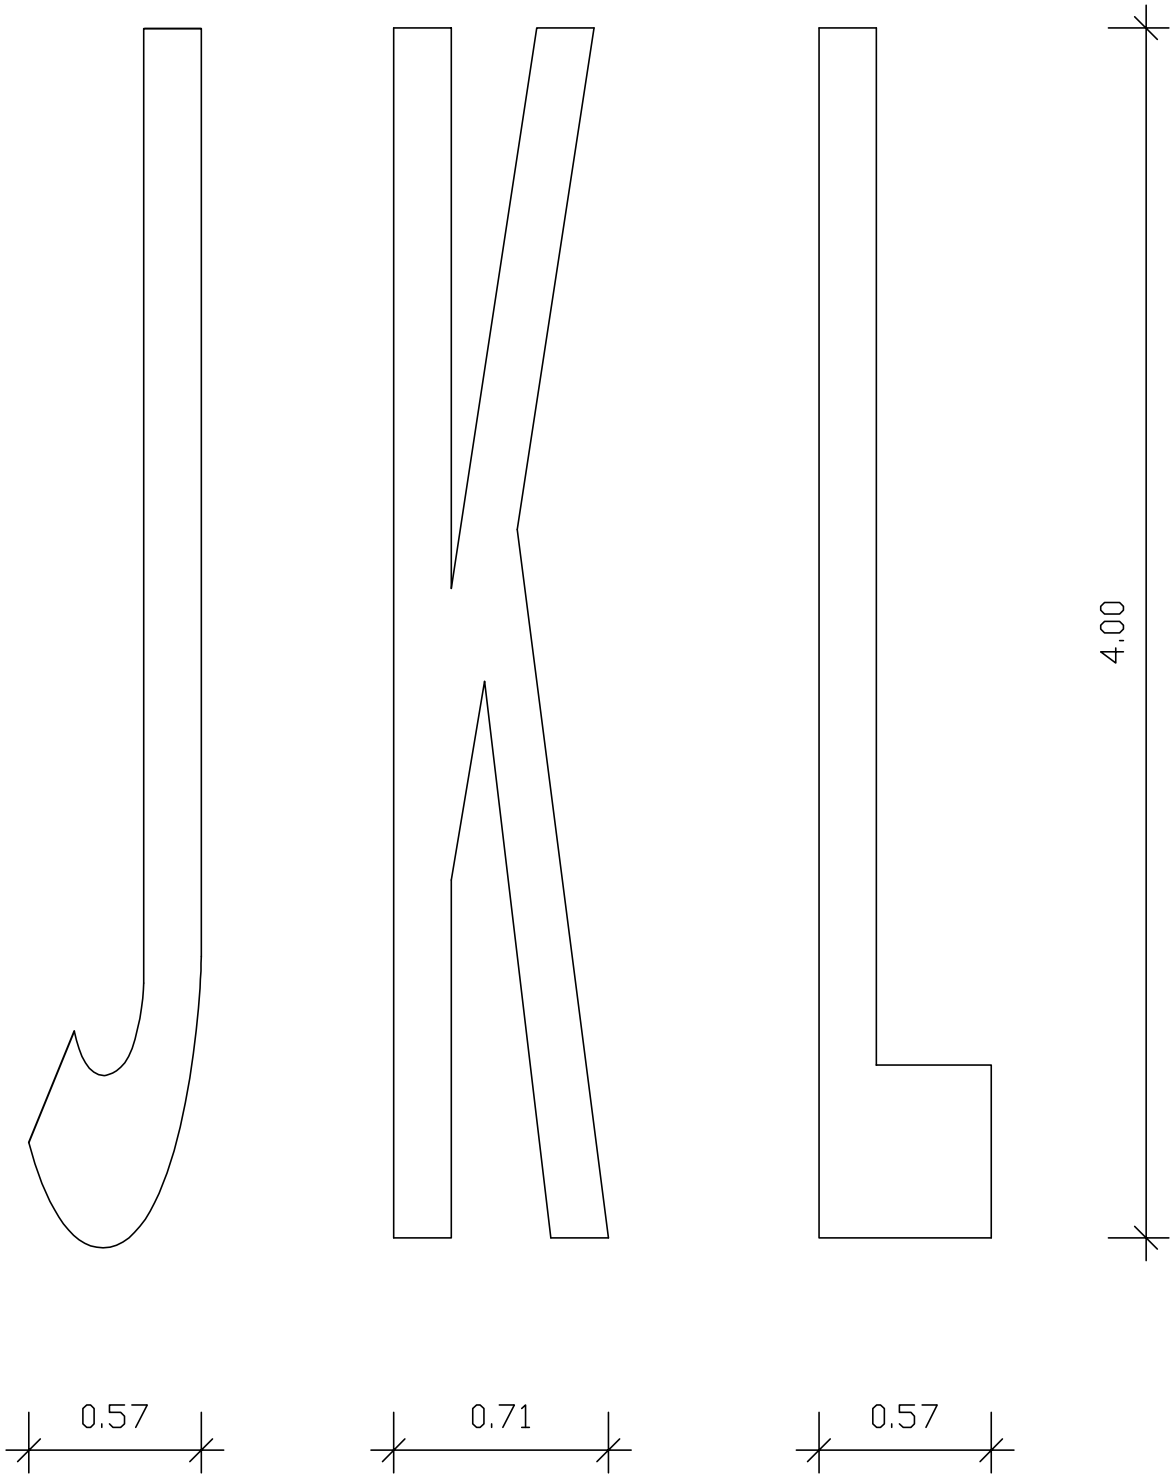


| | | | |
|---|---|---|---|
| 6<br>6.2 | VYBAVENÍ POZEMNÍCH KOMUNIKACÍ<br>VODOROVNÉ DOPRAVNÍ ZNAČKY<br>Písmo<br>Písmena | MINISTERSTVO DOPRAVY<br>ODBOR POZEMNÍCH KOMUNIKACÍ<br>VZOROVÉ LISTY | VL 6<br>V 15 - 4<br>02.17 |

MNO


V 15

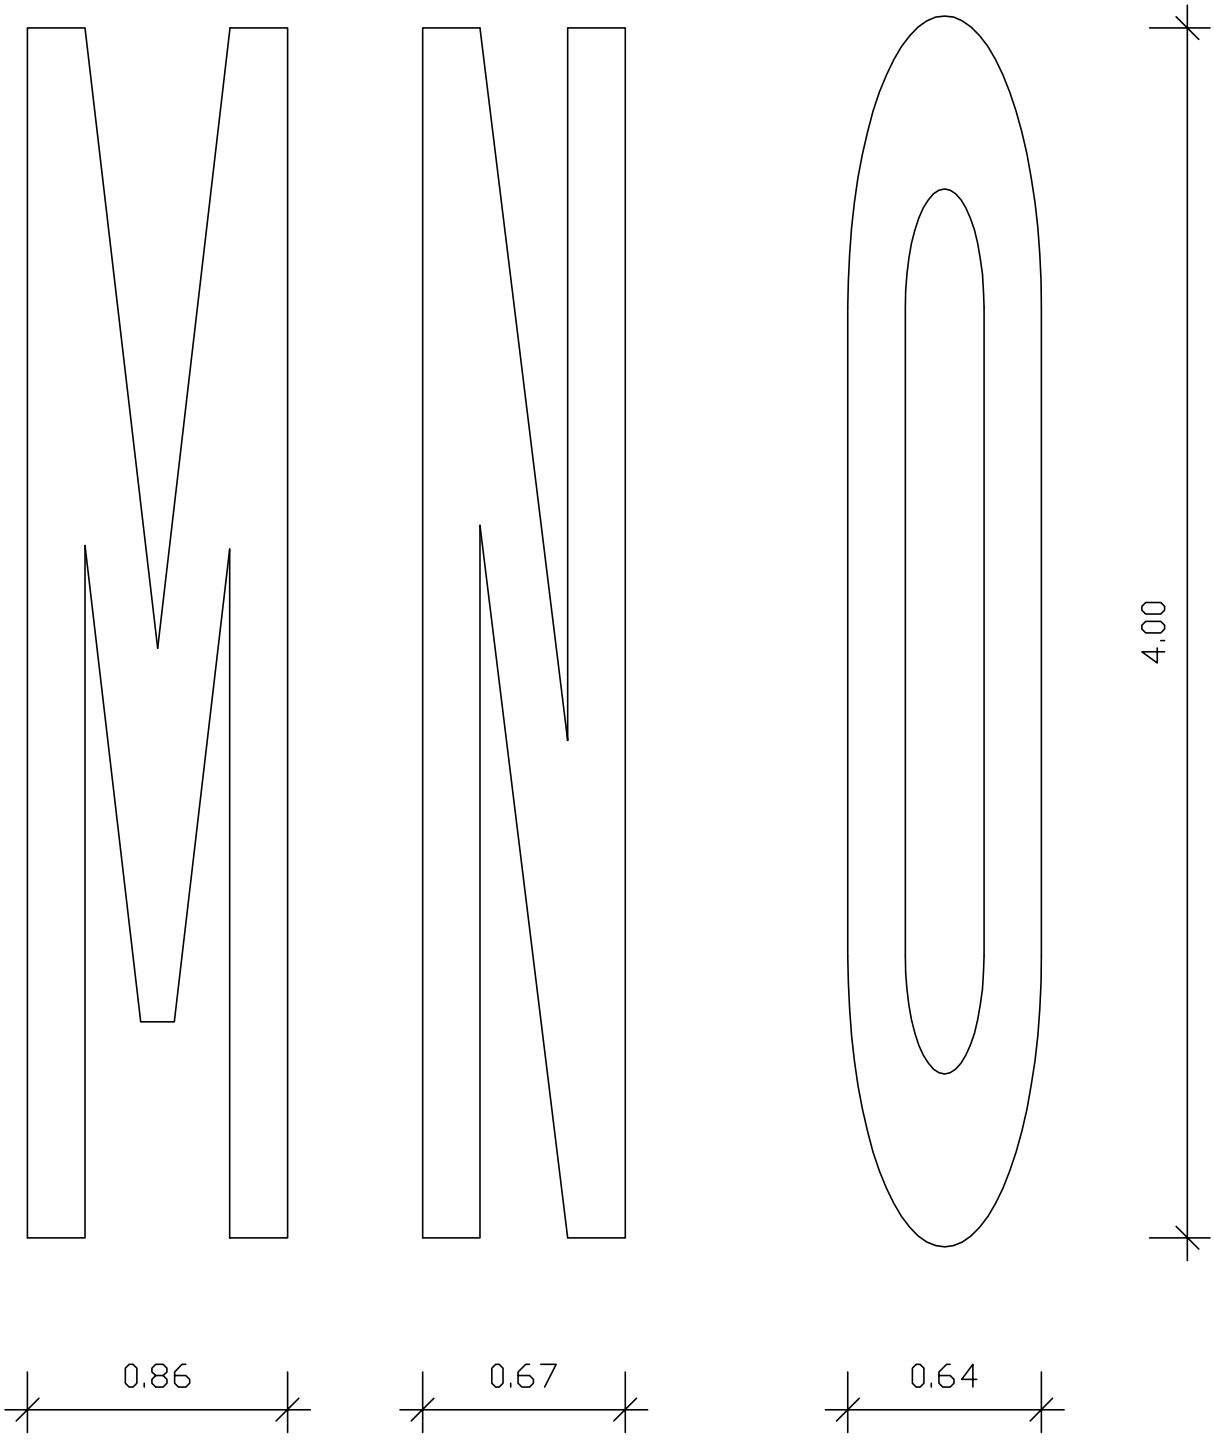


| | | | |
|---|---|---|---|
| 6<br>6.2 | VYBAVENÍ POZEMNÍCH KOMUNIKACÍ<br>VODOROVNÉ DOPRAVNÍ ZNAČKY<br>Písmo<br>Písmena | MINISTERSTVO DOPRAVY<br>ODBOR POZEMNÍCH KOMUNIKACÍ<br>VZOROVÉ LISTY | VL 6<br>V 15 - 5<br>02.17 |

PQR


V 15

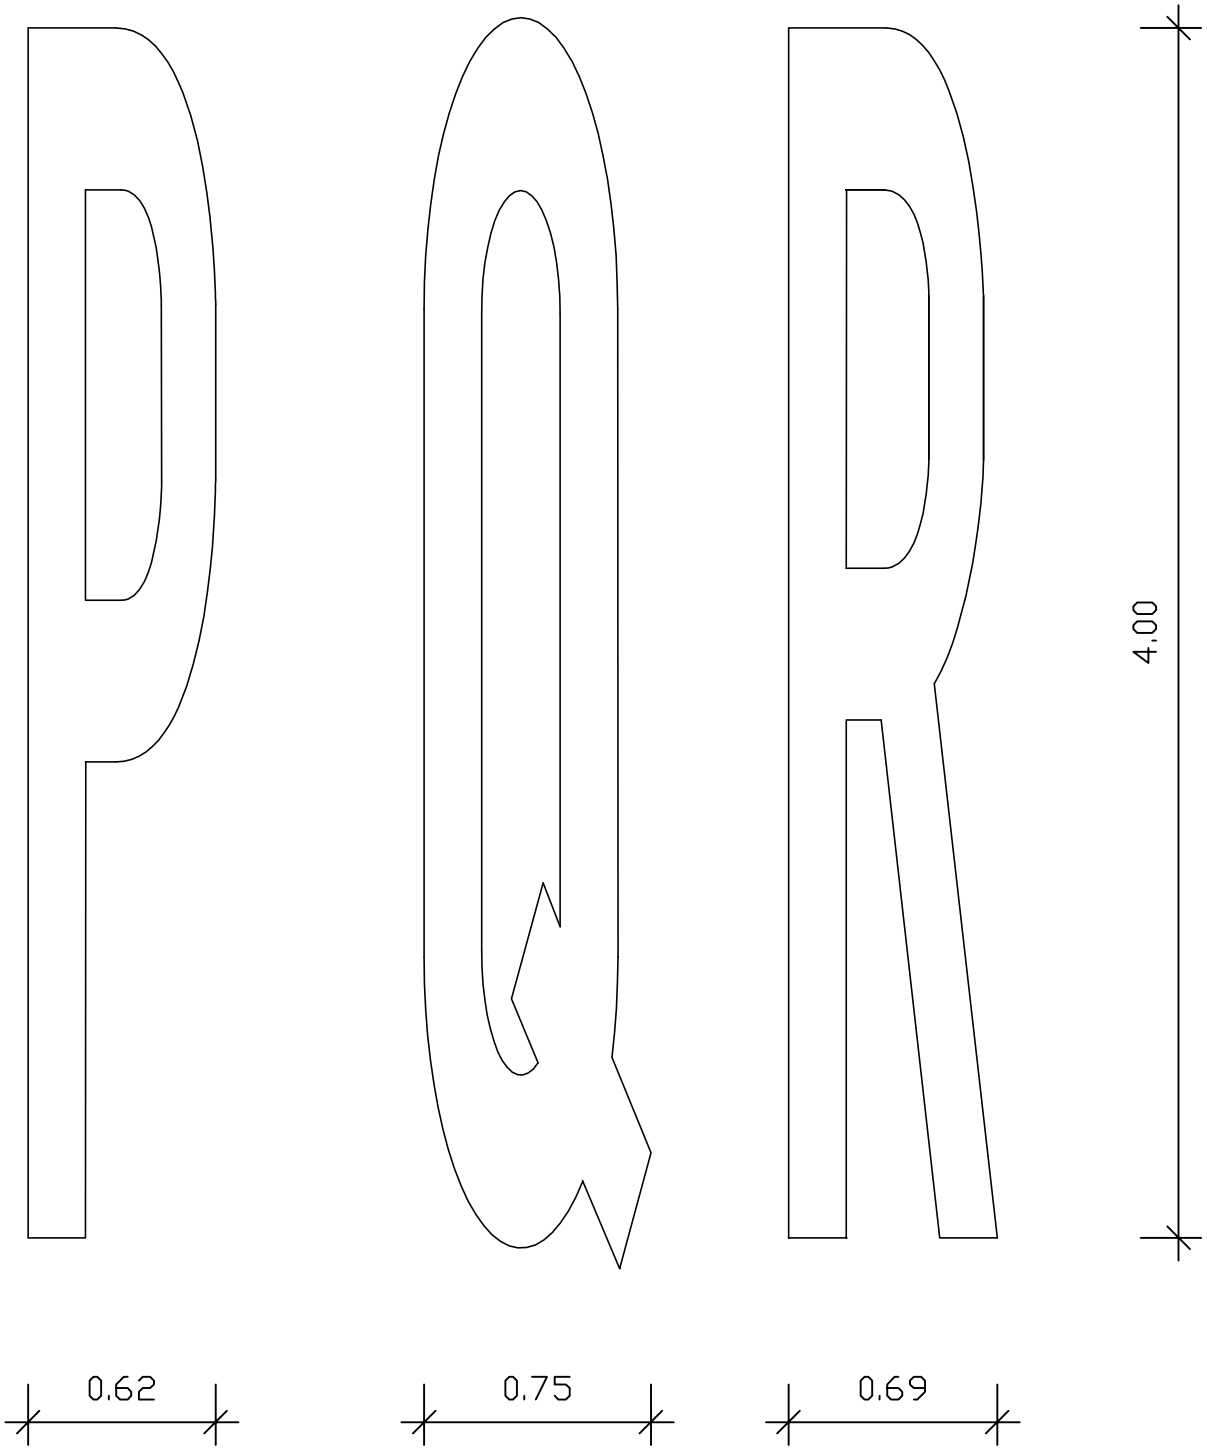


| | | | |
|---|---|---|---|
| 6<br>6.2 | VYBAVENÍ POZEMNÍCH KOMUNIKACÍ<br>VODOROVNÉ DOPRAVNÍ ZNAČKY<br>Písmo<br>Písmena | MINISTERSTVO DOPRAVY<br>ODBOR POZEMNÍCH KOMUNIKACÍ<br>VZOROVÉ LISTY | VL 6<br>V 15 - 6<br>02.17 |

STU


V 15

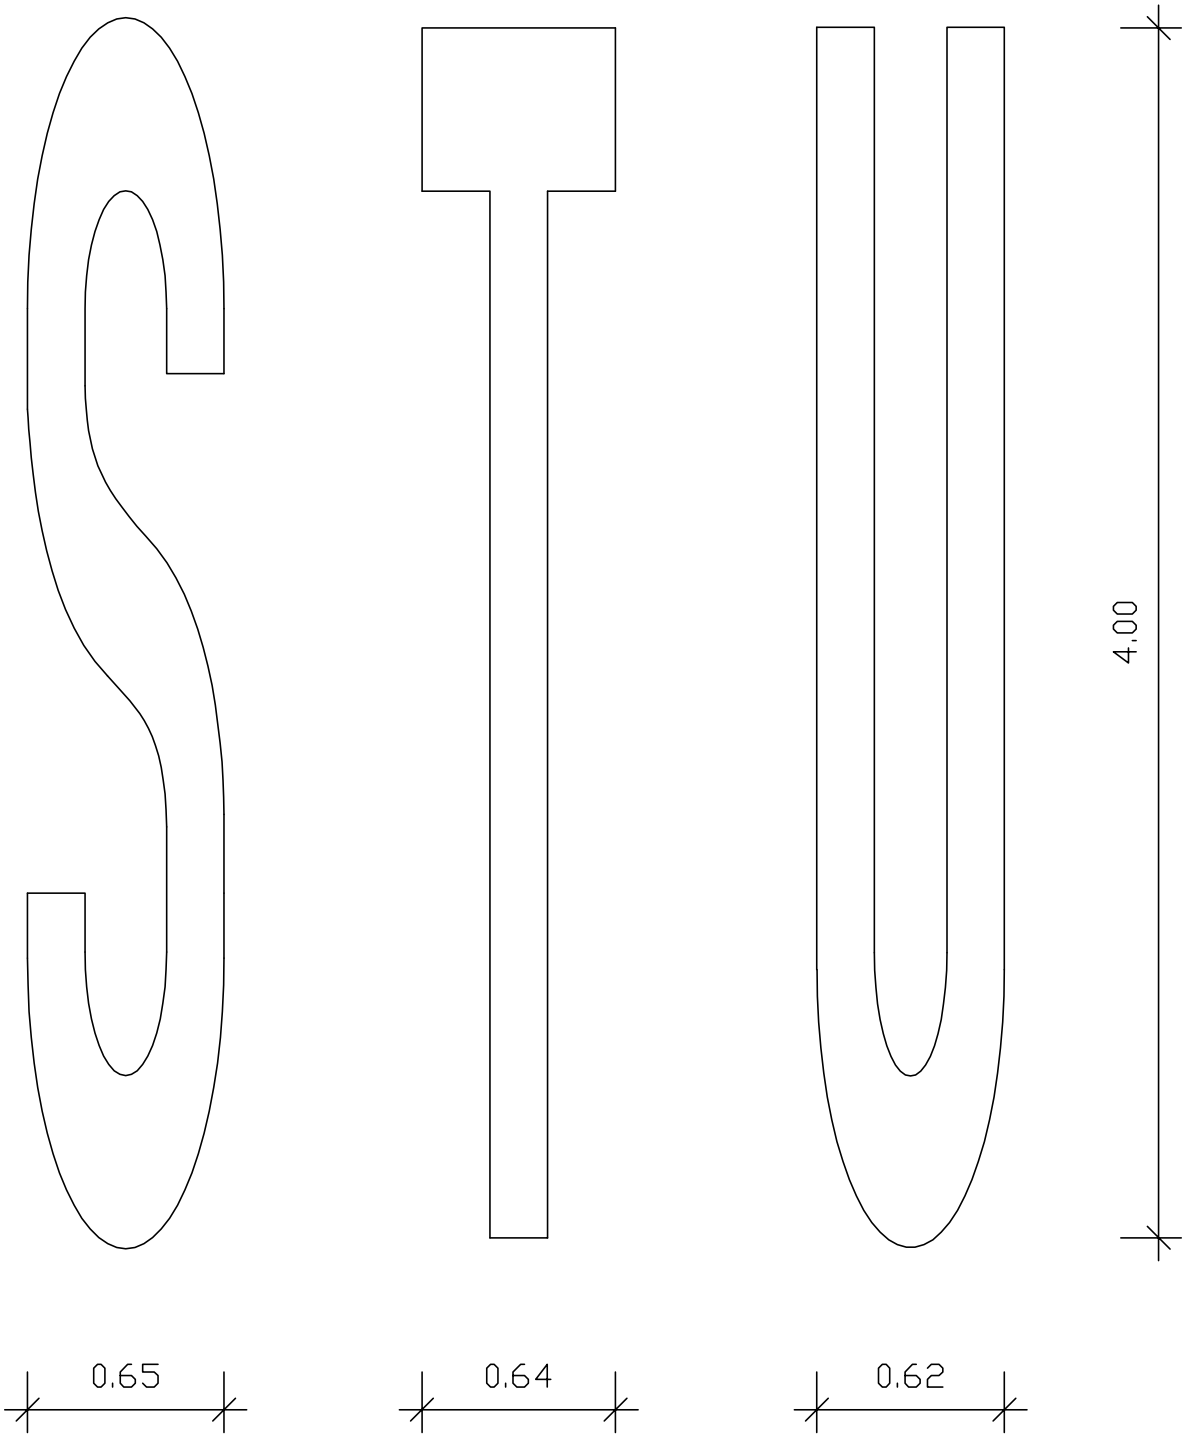


| | | | |
|---|---|---|---|
| 6<br>6.2 | VYBAVENÍ POZEMNÍCH KOMUNIKACÍ<br>VODOROVNÉ DOPRAVNÍ ZNAČKY<br>Písmo<br>Písmena | MINISTERSTVO DOPRAVY<br>ODBOR POZEMNÍCH KOMUNIKACÍ<br>VZOROVÉ LISTY | VL 6<br>V 15 - 7<br>02.17 |

VWX


V 15

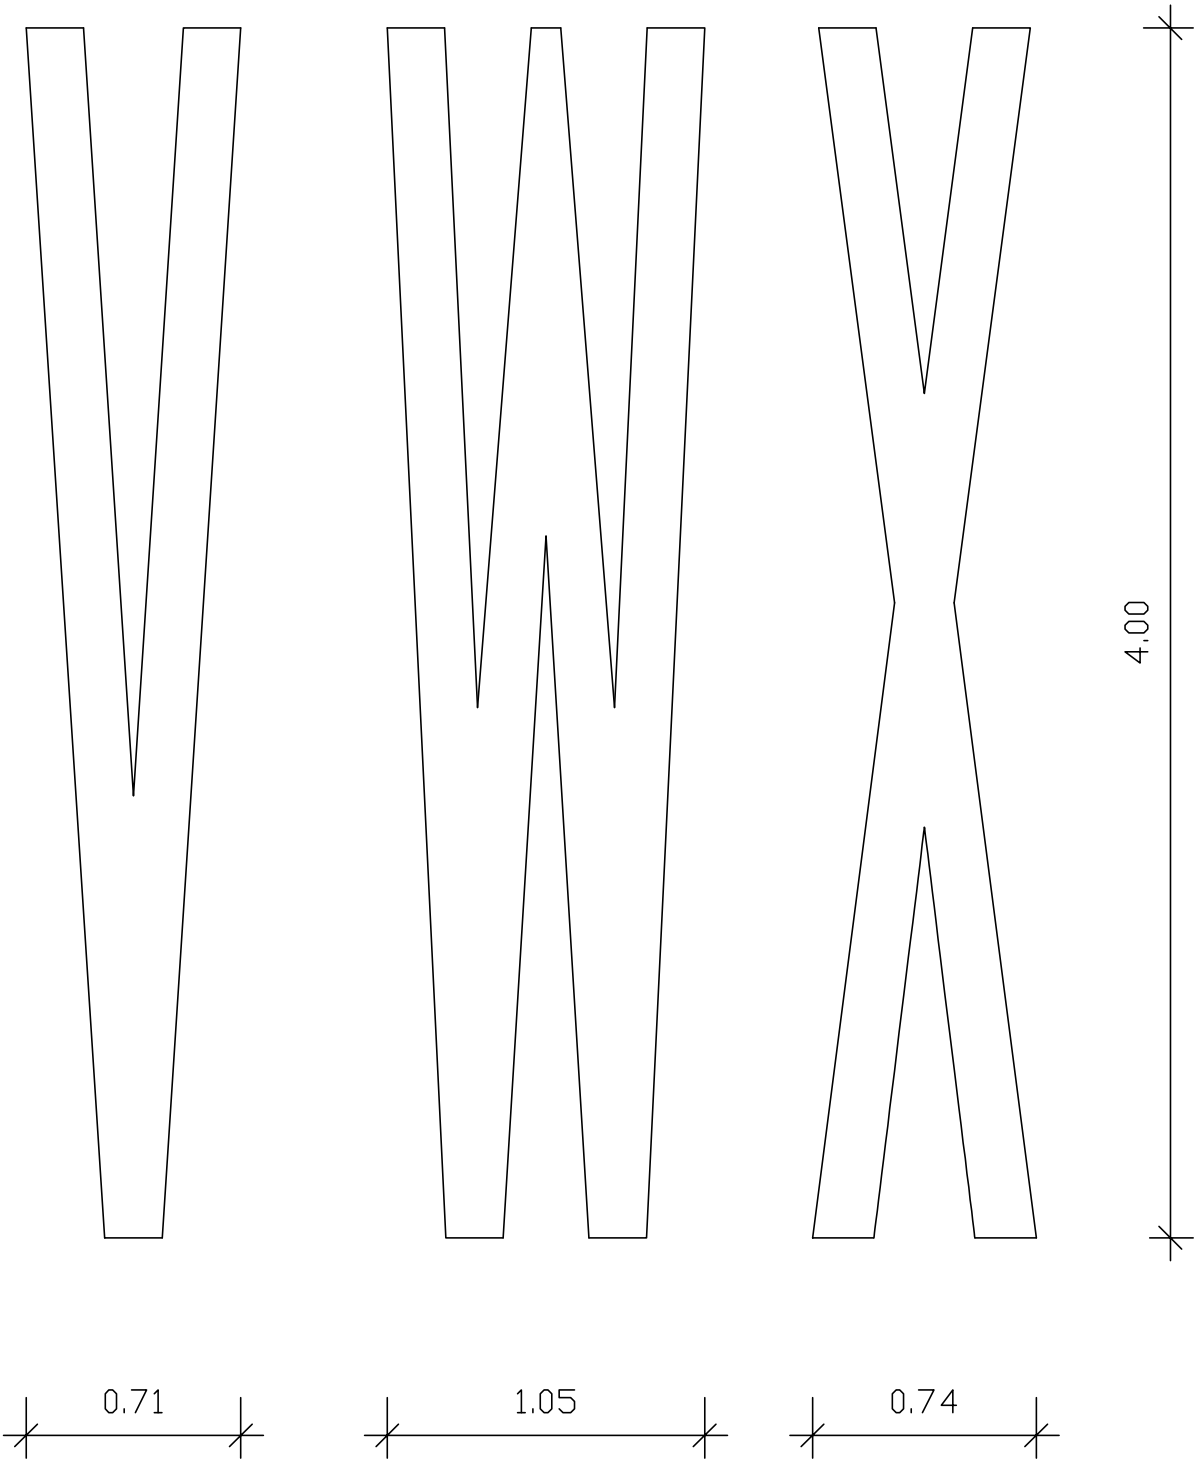


| | | | |
|---|---|---|---|
| 6<br>6.2 | VYBAVENÍ POZEMNÍCH KOMUNIKACÍ<br>VODOROVNÉ DOPRAVNÍ ZNAČKY<br>Písmo<br>Písmena | MINISTERSTVO DOPRAVY<br>ODBOR POZEMNÍCH KOMUNIKACÍ<br>VZOROVÉ LISTY | VL 6<br>V 15 - 8<br>02.17 |

YZ


V 15

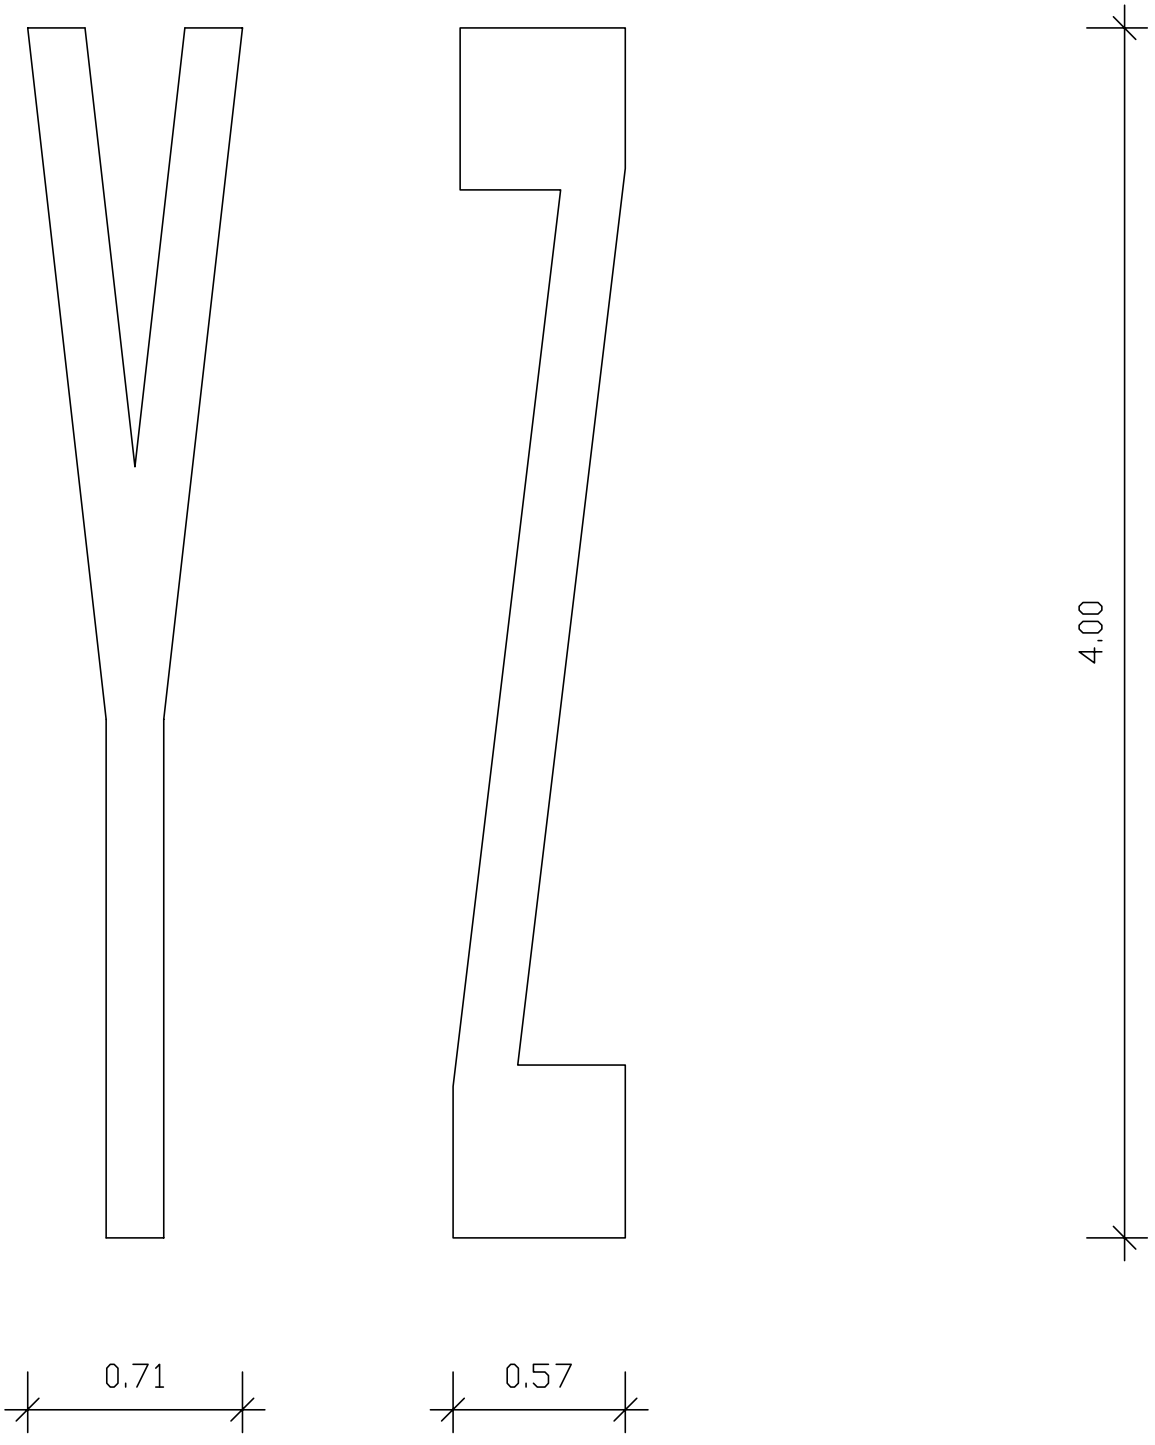


| | | | |
|---|---|---|---|
| 6<br>6.2 | VYBAVENÍ POZEMNÍCH KOMUNIKACÍ<br>VODOROVNÉ DOPRAVNÍ ZNAČKY<br>Písmo<br>Písmena | MINISTERSTVO DOPRAVY<br>ODBOR POZEMNÍCH KOMUNIKACÍ<br>VZOROVÉ LISTY | VL 6<br>V 15 - 9<br>02.17 |

123


V 15

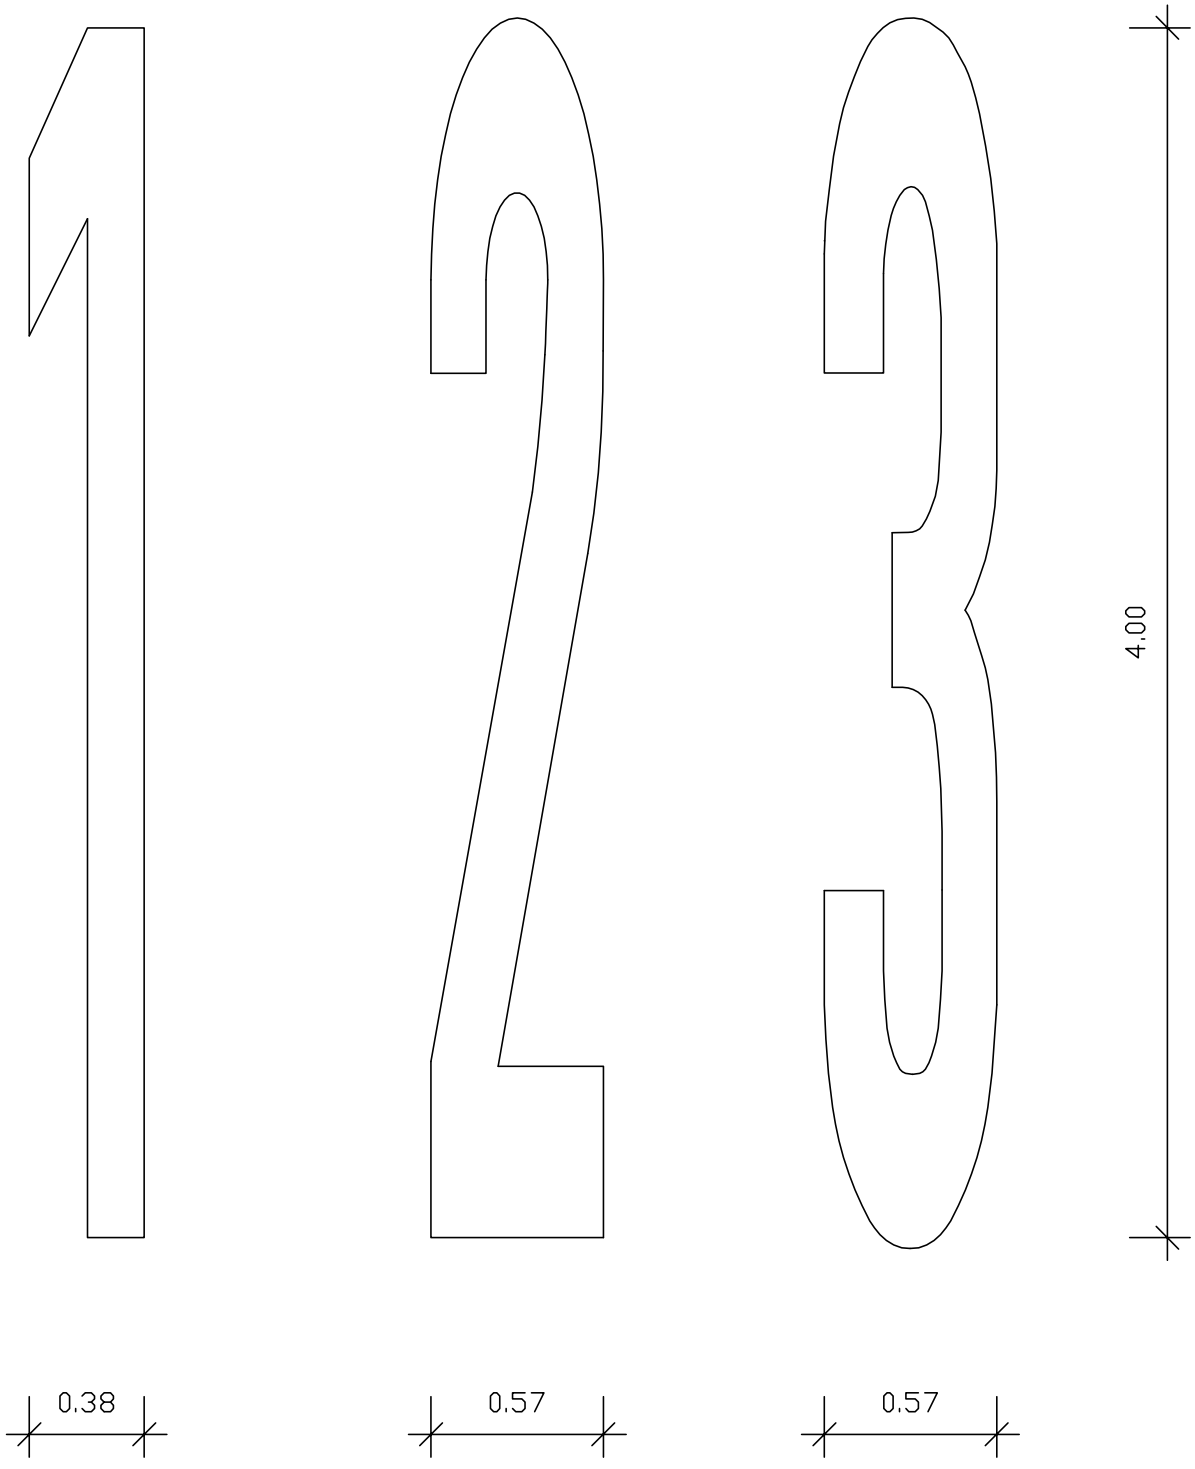


| | | | |
|---|---|---|---|
| 6 VYBAVENÍ POZEMNÍCH KOMUNIKACÍ<br>6.2 VODOROVNÉ DOPRAVNÍ ZNAČKY<br>Písmo<br>Číslice | MINISTERSTVO DOPRAVY<br>ODBOR POZEMNÍCH KOMUNIKACÍ<br>VZOROVÉ LISTY | VL 6<br>V 15 - 10<br>02.17 |

456


V 15

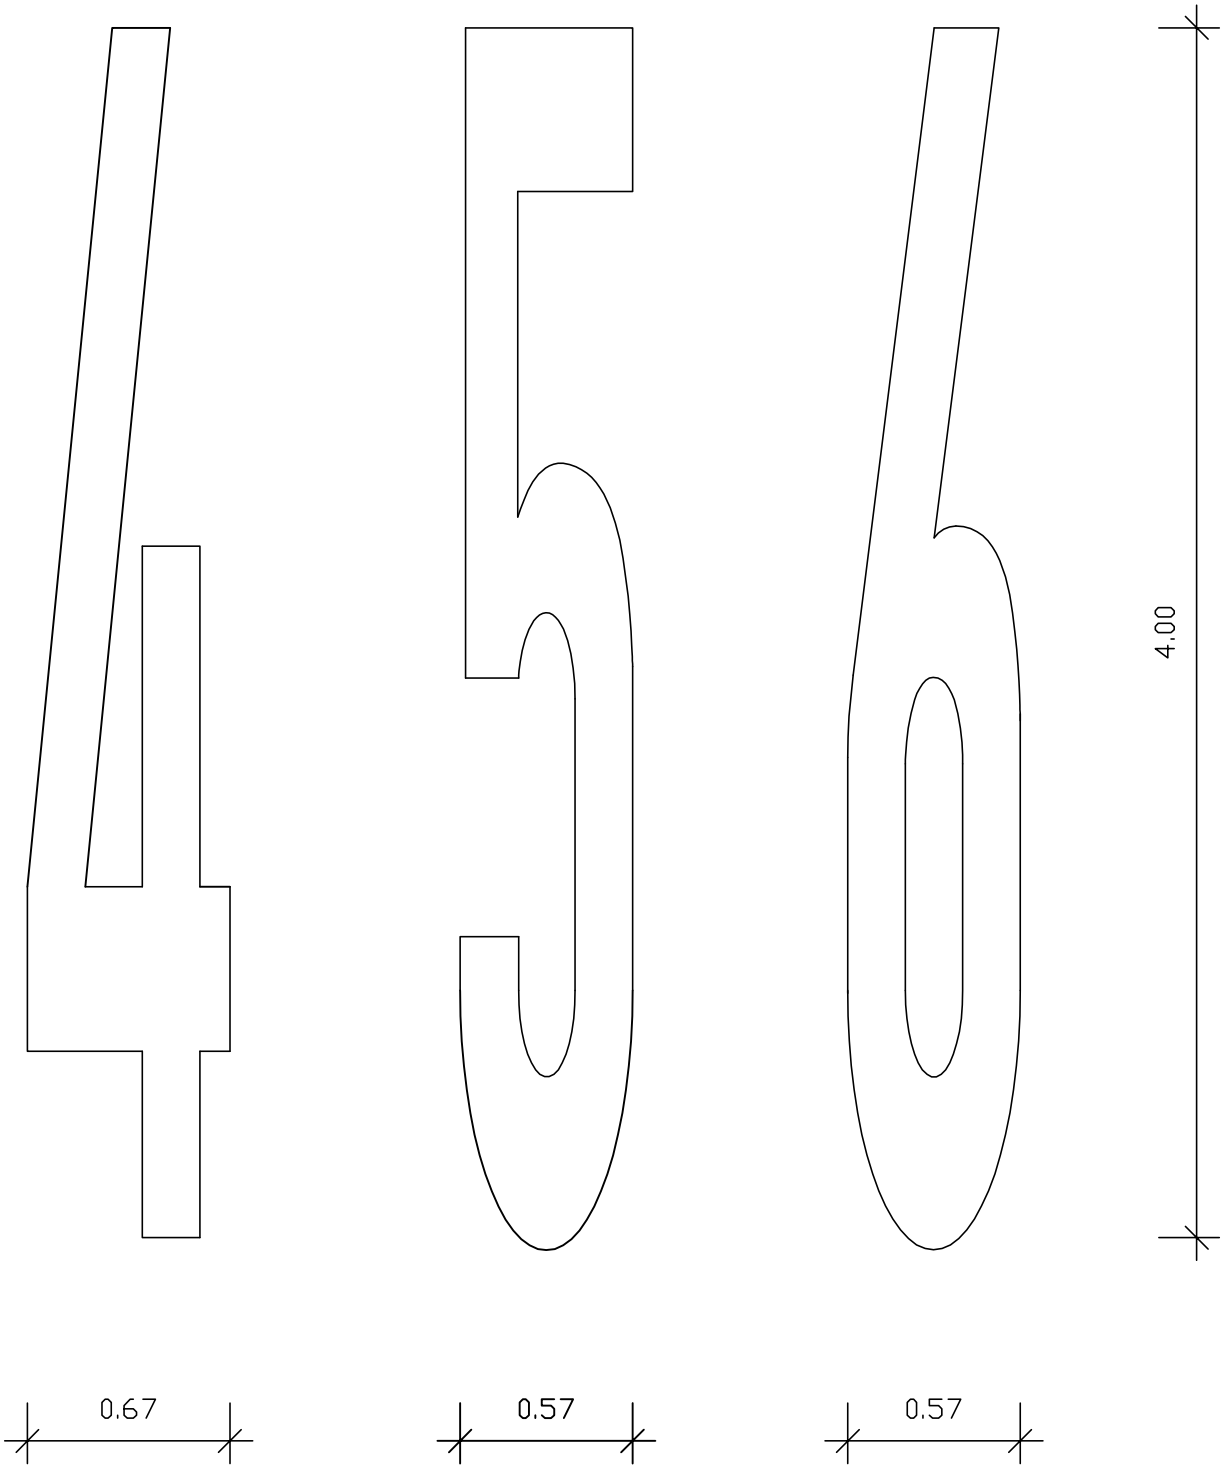


| | | | |
|---|---|---|---|
| 6 VYBAVENÍ POZEMNÍCH KOMUNIKACÍ<br>6.2 VODOROVNÉ DOPRAVNÍ ZNAČKY<br>Písmo<br>Číslice | MINISTERSTVO DOPRAVY<br>ODBOR POZEMNÍCH KOMUNIKACÍ<br>VZOROVÉ LISTY | VL 6<br>V 15 - 11<br>02.17 |

789


V 15

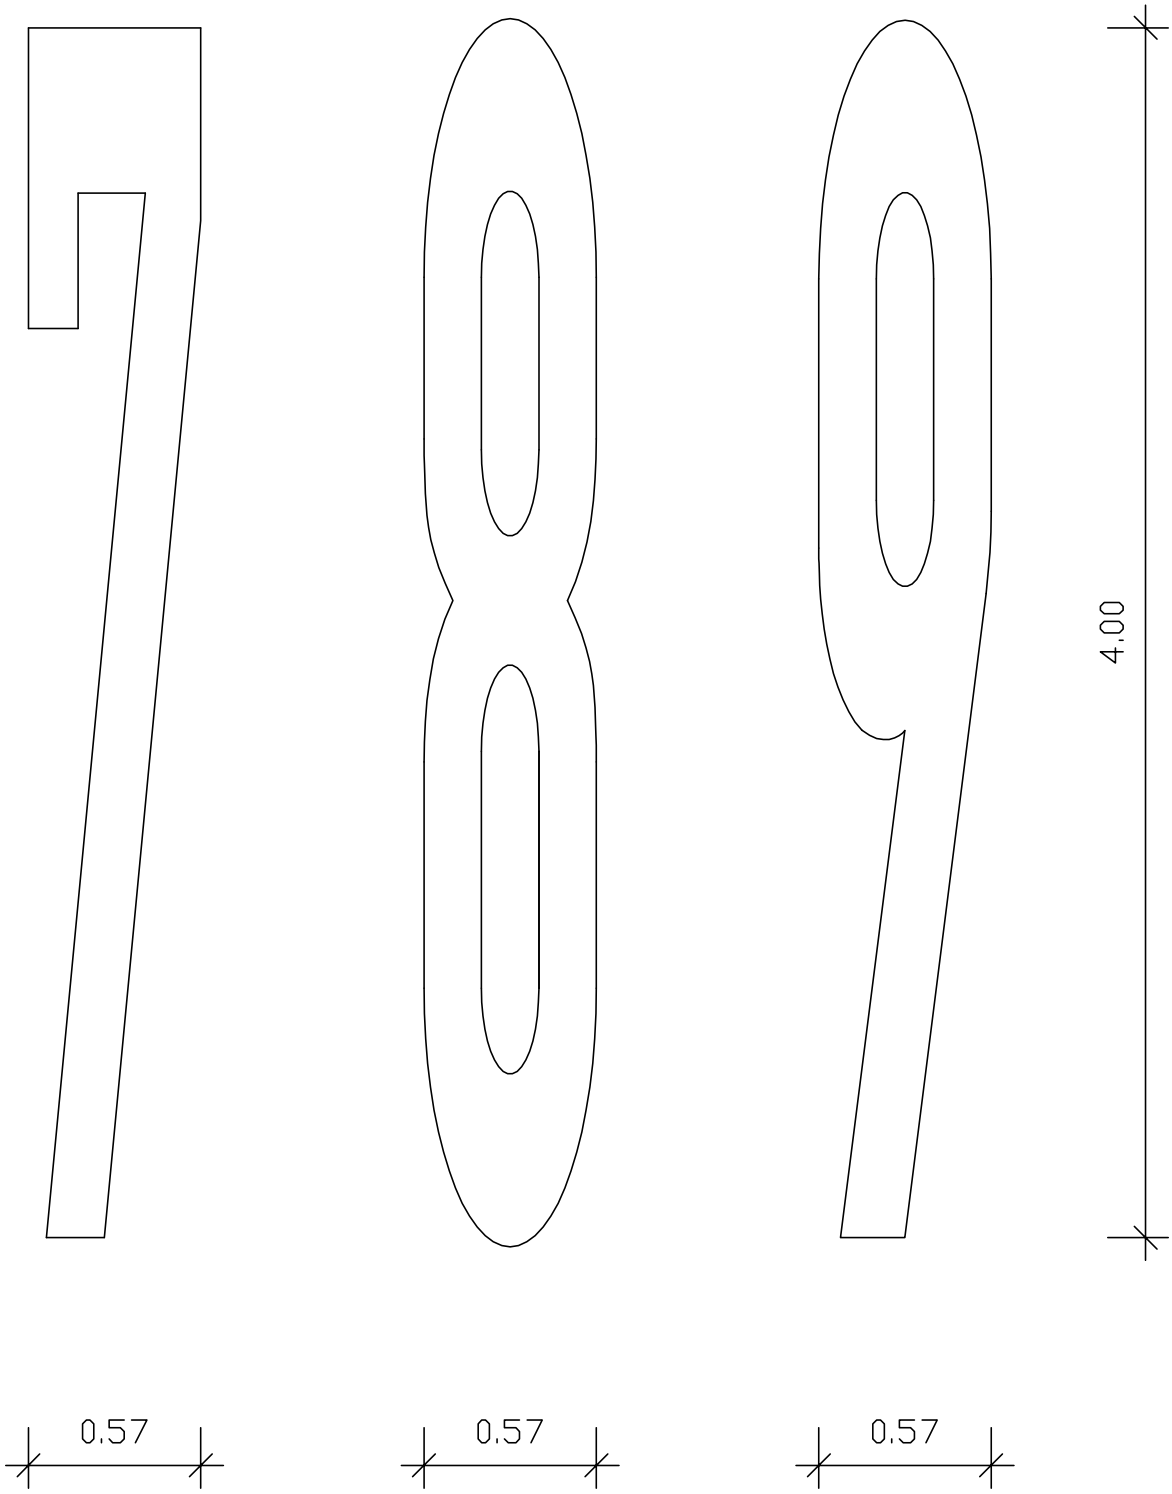




| | | | |
|---|---|---|---|
| 6<br>6.2<br>Písmo<br>Číslice | VYBAVENÍ POZEMNÍCH KOMUNIKACÍ<br>VODOROVNÉ DOPRAVNÍ ZNAČKY | MINISTERSTVO DOPRAVY<br>ODBOR POZEMNÍCH KOMUNIKACÍ<br>VZOROVÉ LISTY | VL 6<br>V 15 - 12<br>02.17 |




**V 15**

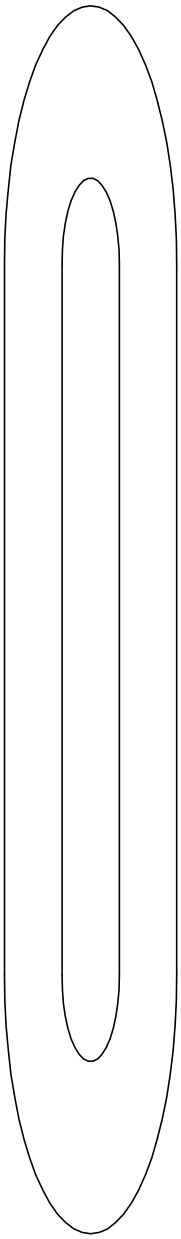

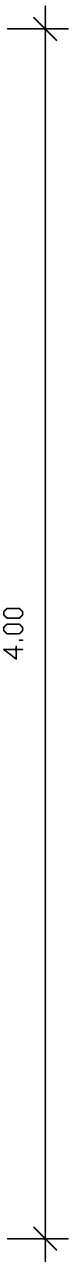

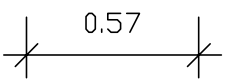


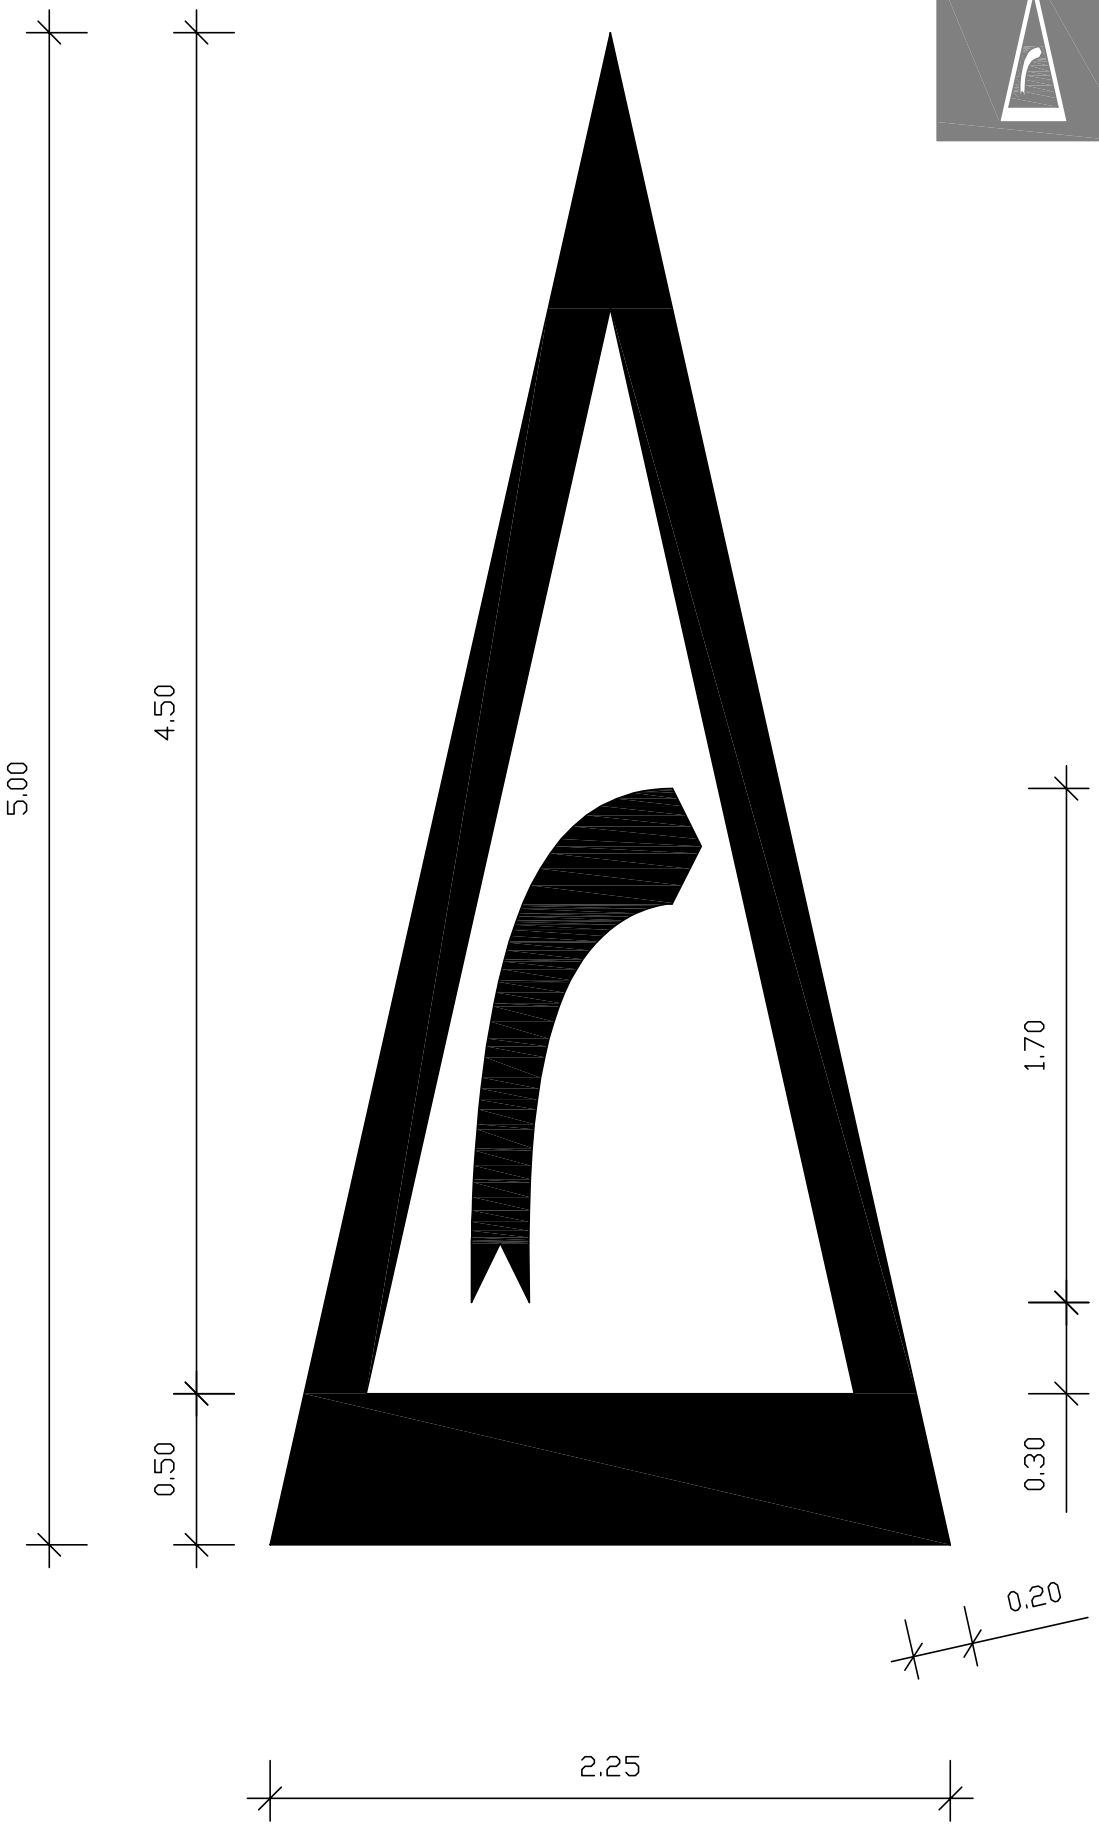

| | | | |
|---|---|---|---|
| **6** **VYBAVENÍ POZEMNÍCH KOMUNIKACÍ**<br>**6.2** **VODOROVNÉ DOPRAVNÍ ZNAČKY**<br>**Písmo**<br>**Číslice** | **MINISTERSTVO DOPRAVY**<br>**ODBOR POZEMNÍCH KOMUNIKACÍ**<br>**VZOROVÉ LISTY** | **VL 6**<br>**V 15 - 13**<br>**02.17** |




**V 15**
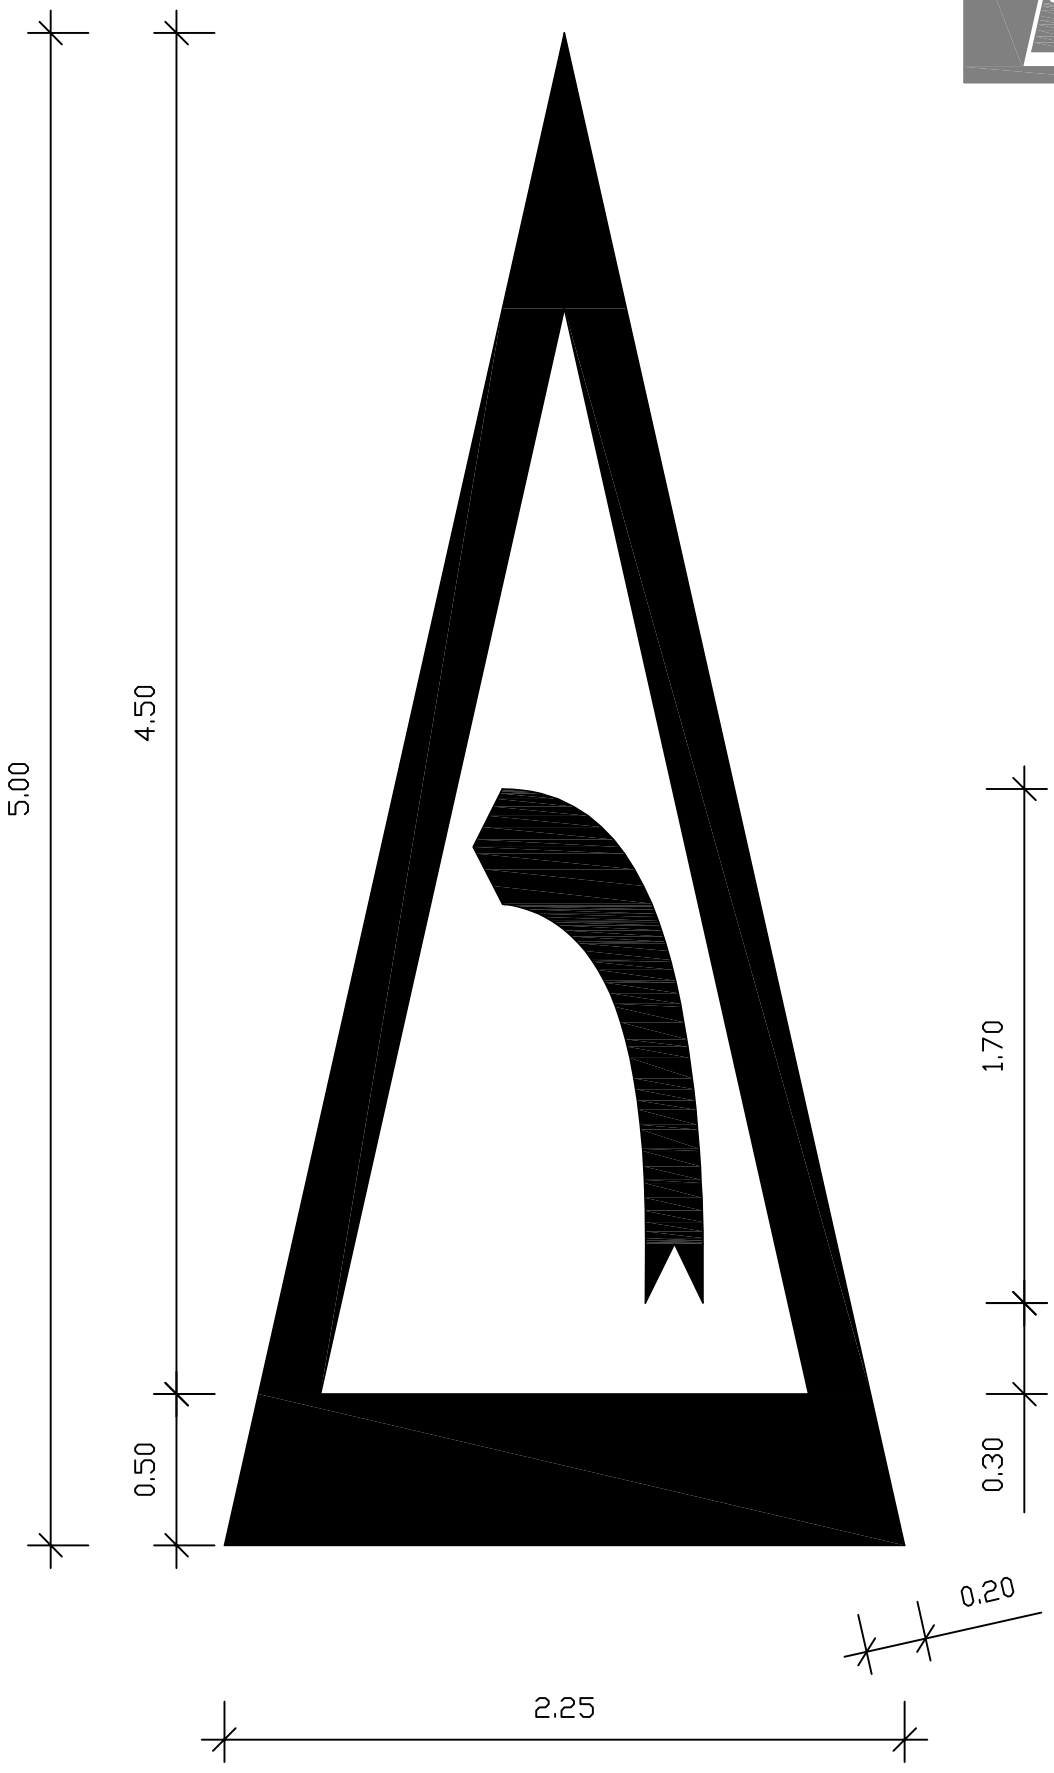
| | | | |
|---|---|---|---|
| **6**<br>**6.2** | **VYBAVENÍ POZEMNÍCH KOMUNIKACÍ**<br>**VODOROVNÉ DOPRAVNÍ ZNAČKY**<br>**č. V 15 Nápis na vozovce**<br>Symbol značky č. A 1a Zatáčka vpravo | MINISTERSTVO DOPRAVY<br>ODBOR POZEMNÍCH KOMUNIKACÍ<br>**VZOROVÉ LISTY** | **VL 6**<br>**V 15 - 14**<br>**02.17** |




V 15

**6 VYBAVENÍ POZEMNÍCH KOMUNIKACÍ**


**6.2 VODOROVNÉ DOPRAVNÍ ZNAČKY**

**č. V 15 Nápis na vozovce**


Symbol značky č. A 1b Zatáčka vlevo

MINISTERSTVO DOPRAVY
ODBOR POZEMNÍCH KOMUNIKACÍ
**VZOROVÉ LISTY**


**VL 6**
**V 15 - 15**
**02.17**

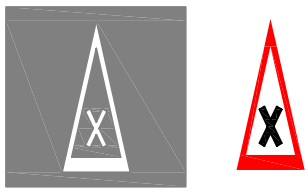


**V 15**

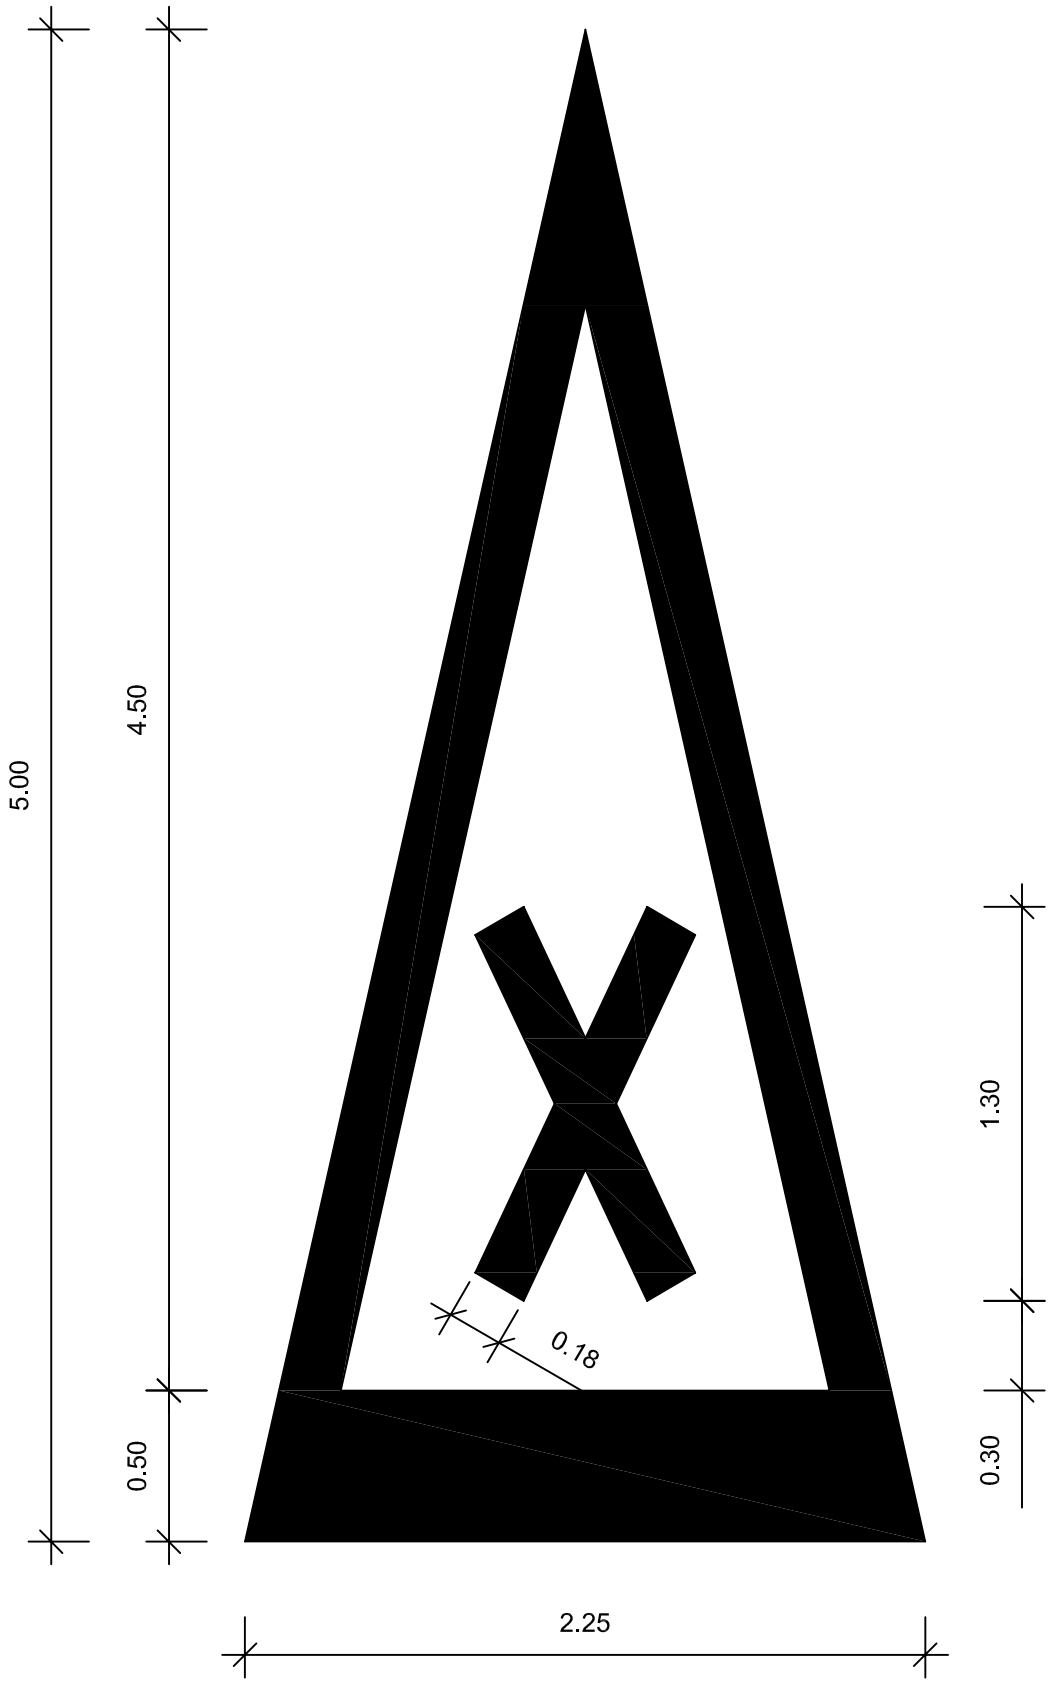



| | | | |
|---|---|---|---|
| **6** **6.2** | **VYBAVENÍ POZEMNÍCH KOMUNIKACÍ**<br>**VODOROVNÉ DOPRAVNÍ ZNAČKY**<br>**č. V 15 Nápis na vozovce**<br>Symbol značky č. A 3 Křižovatka | MINISTERSTVO DOPRAVY<br>ODBOR POZEMNÍCH KOMUNIKACÍ<br>**VZOROVÉ LISTY** | **VL 6**<br>**V 15 - 16**<br>**02.17** |

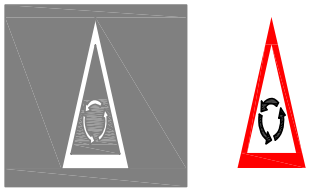

**V 15**

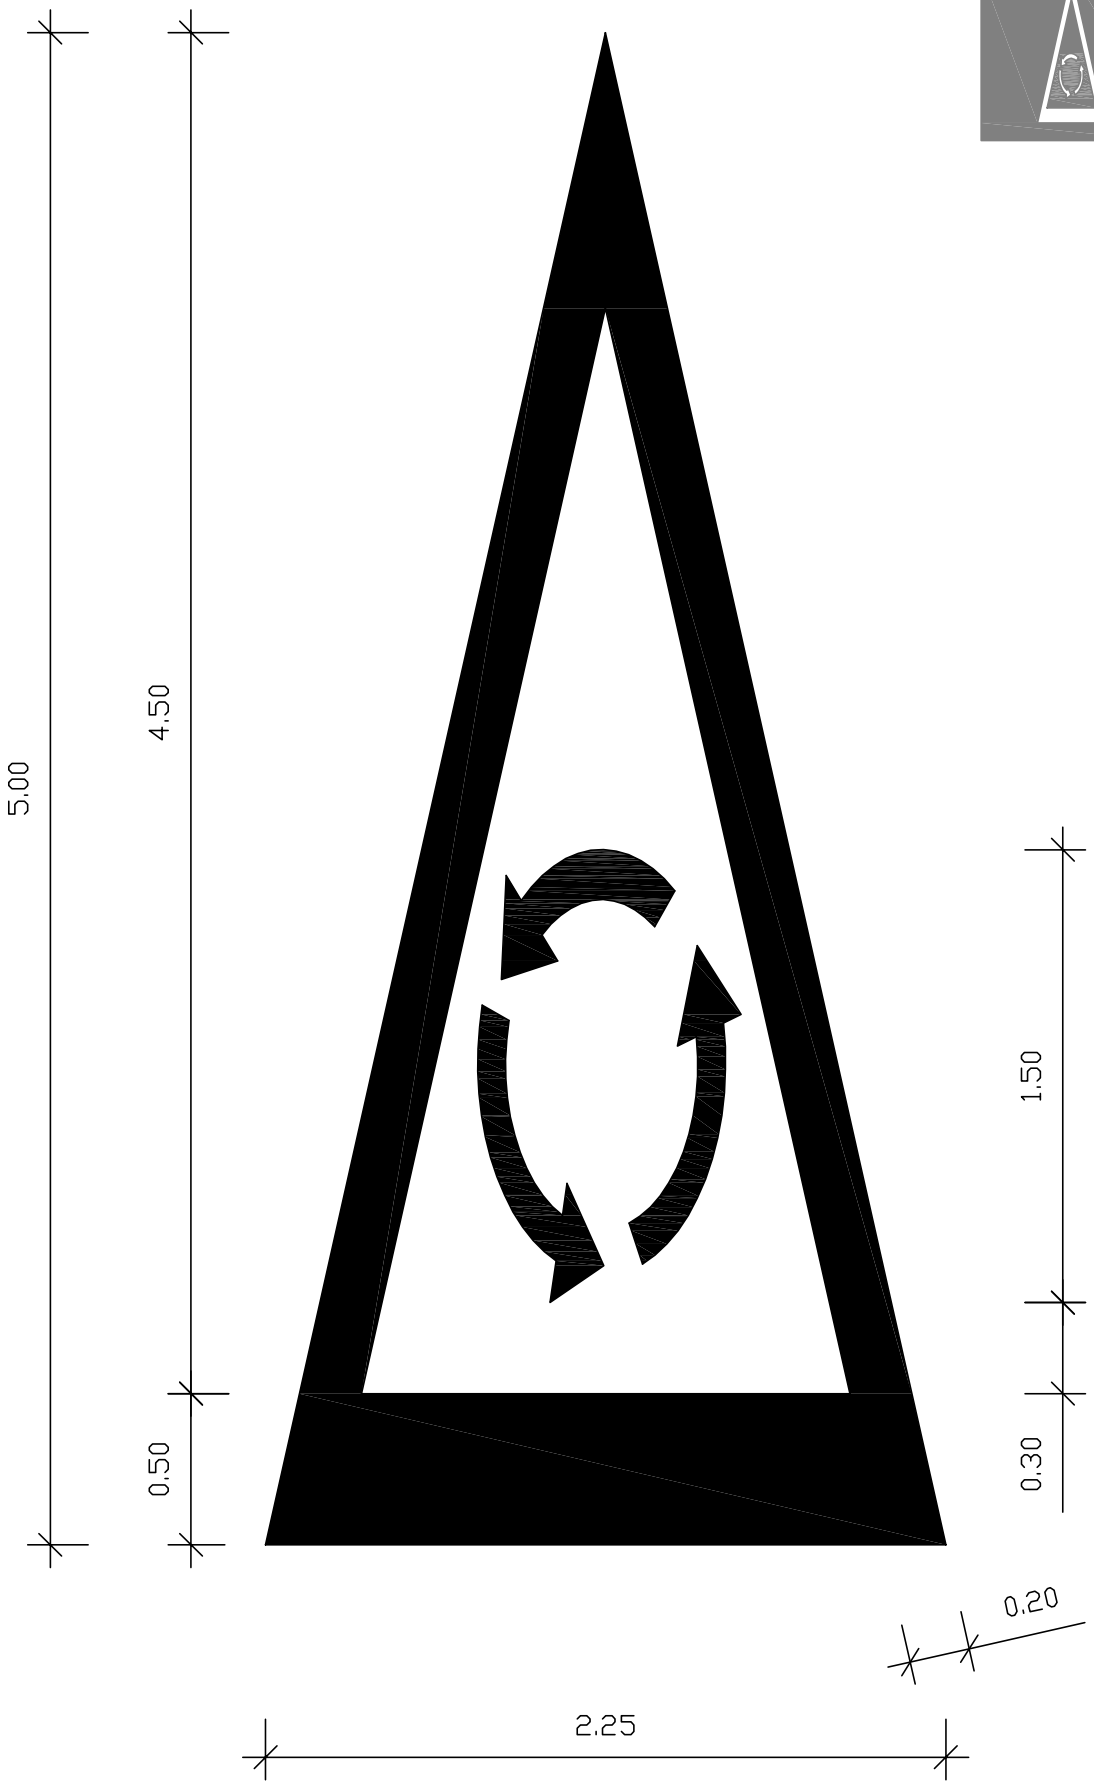



| | | | |
|---|---|---|---|
| **6**<br>**6.2** | **VYBAVENÍ POZEMNÍCH KOMUNIKACÍ**<br>**VODOROVNÉ DOPRAVNÍ ZNAČKY**<br>**č. V 15 Nápis na vozovce**<br>Symbol značky č. A 4 Křižovatka s kruhovým objezdem | MINISTERSTVO DOPRAVY<br>ODBOR POZEMNÍCH KOMUNIKACÍ<br>**VZOROVÉ LISTY** | **VL 6**<br>**V 15 - 17**<br>**02.17** |

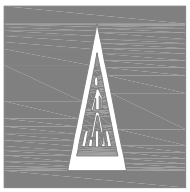




**V 15**

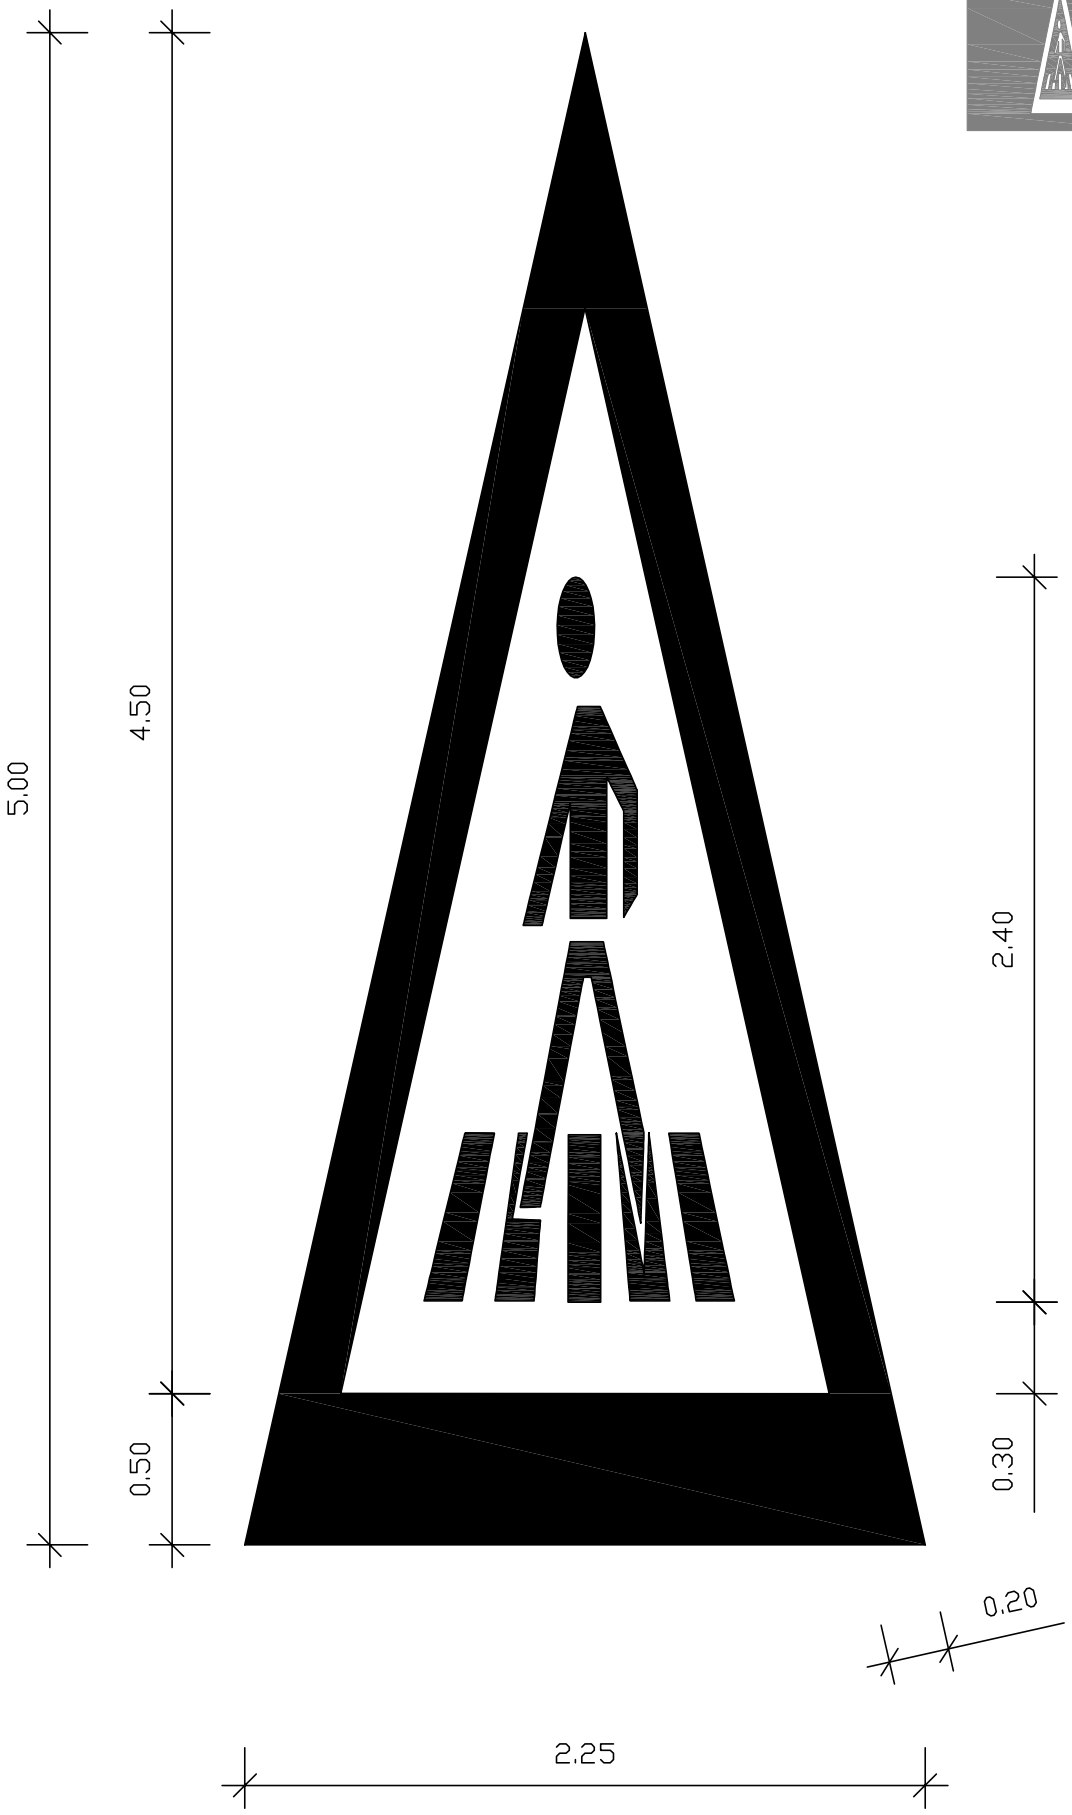



| | | | |
|---|---|---|---|
| **6**<br>**6.2** | **VYBAVENÍ POZEMNÍCH KOMUNIKACÍ**<br>**VODOROVNÉ DOPRAVNÍ ZNAČKY**<br>**č. V 15 Nápis na vozovce**<br>Symbol značky č. A 11 Přechod pro chodce | MINISTERSTVO DOPRAVY<br>ODBOR POZEMNÍCH KOMUNIKACÍ<br>**VZOROVÉ LISTY** | **VL 6**<br>**V 15 - 18**<br>**02.17** |

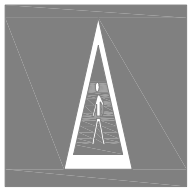





**V 15**

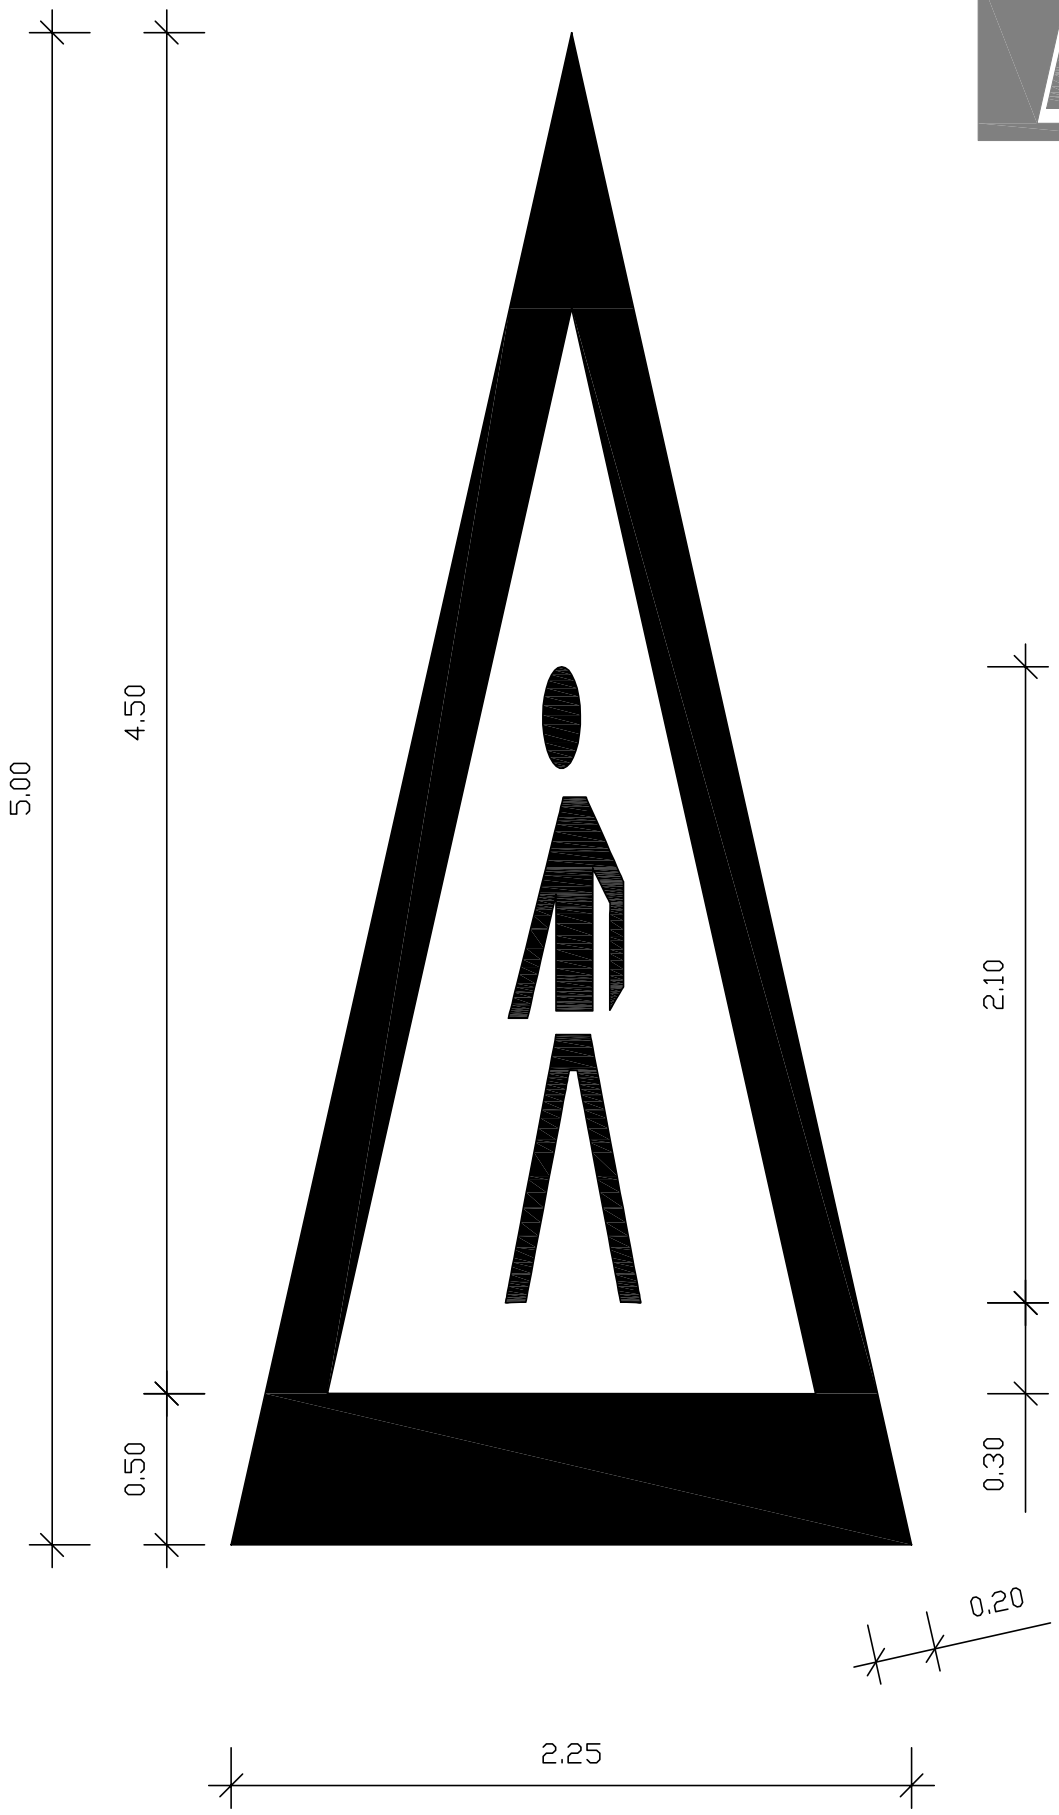



| | | | |
|---|---|---|---|
| **6**<br>**6.2** | **VYBAVENÍ POZEMNÍCH KOMUNIKACÍ**<br>**VODOROVNÉ DOPRAVNÍ ZNAČKY**<br>**č. V 15 Nápis na vozovce**<br>Symbol značky č. A 12a Chodci | MINISTERSTVO DOPRAVY<br>ODBOR POZEMNÍCH KOMUNIKACÍ<br>**VZOROVÉ LISTY** | **VL 6**<br>**V 15 - 19**<br>**02.17** |

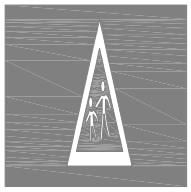

**V 15**

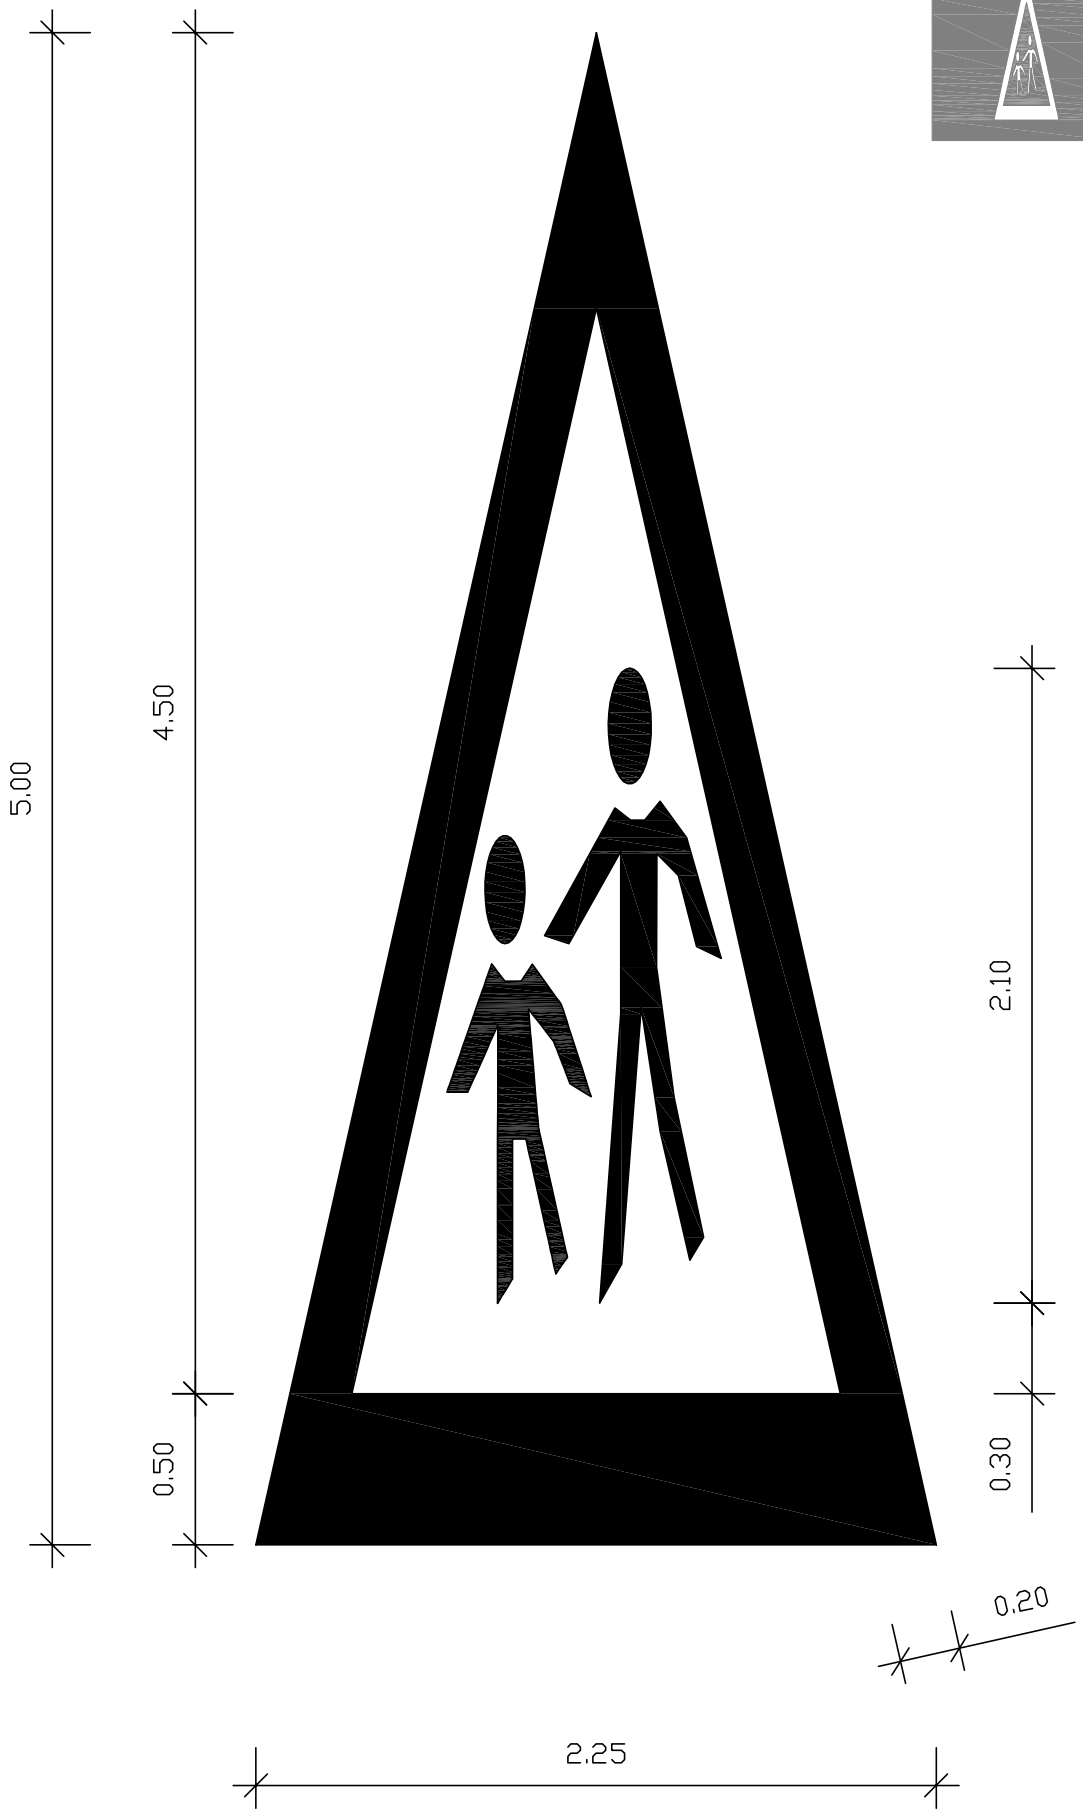



| | | | |
|---|---|---|---|
| **6**<br>**6.2** | **VYBAVENÍ POZEMNÍCH KOMUNIKACÍ**<br>**VODOROVNÉ DOPRAVNÍ ZNAČKY**<br>**č. V15 Nápis na vozovce**<br>Symbol značky č. A 12b Děti | MINISTERSTVO DOPRAVY<br>ODBOR POZEMNÍCH KOMUNIKACÍ<br>**VZOROVÉ LISTY** | **VL 6**<br>**V 15 - 20**<br>**02.17** |

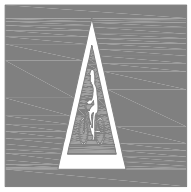




**V 15**

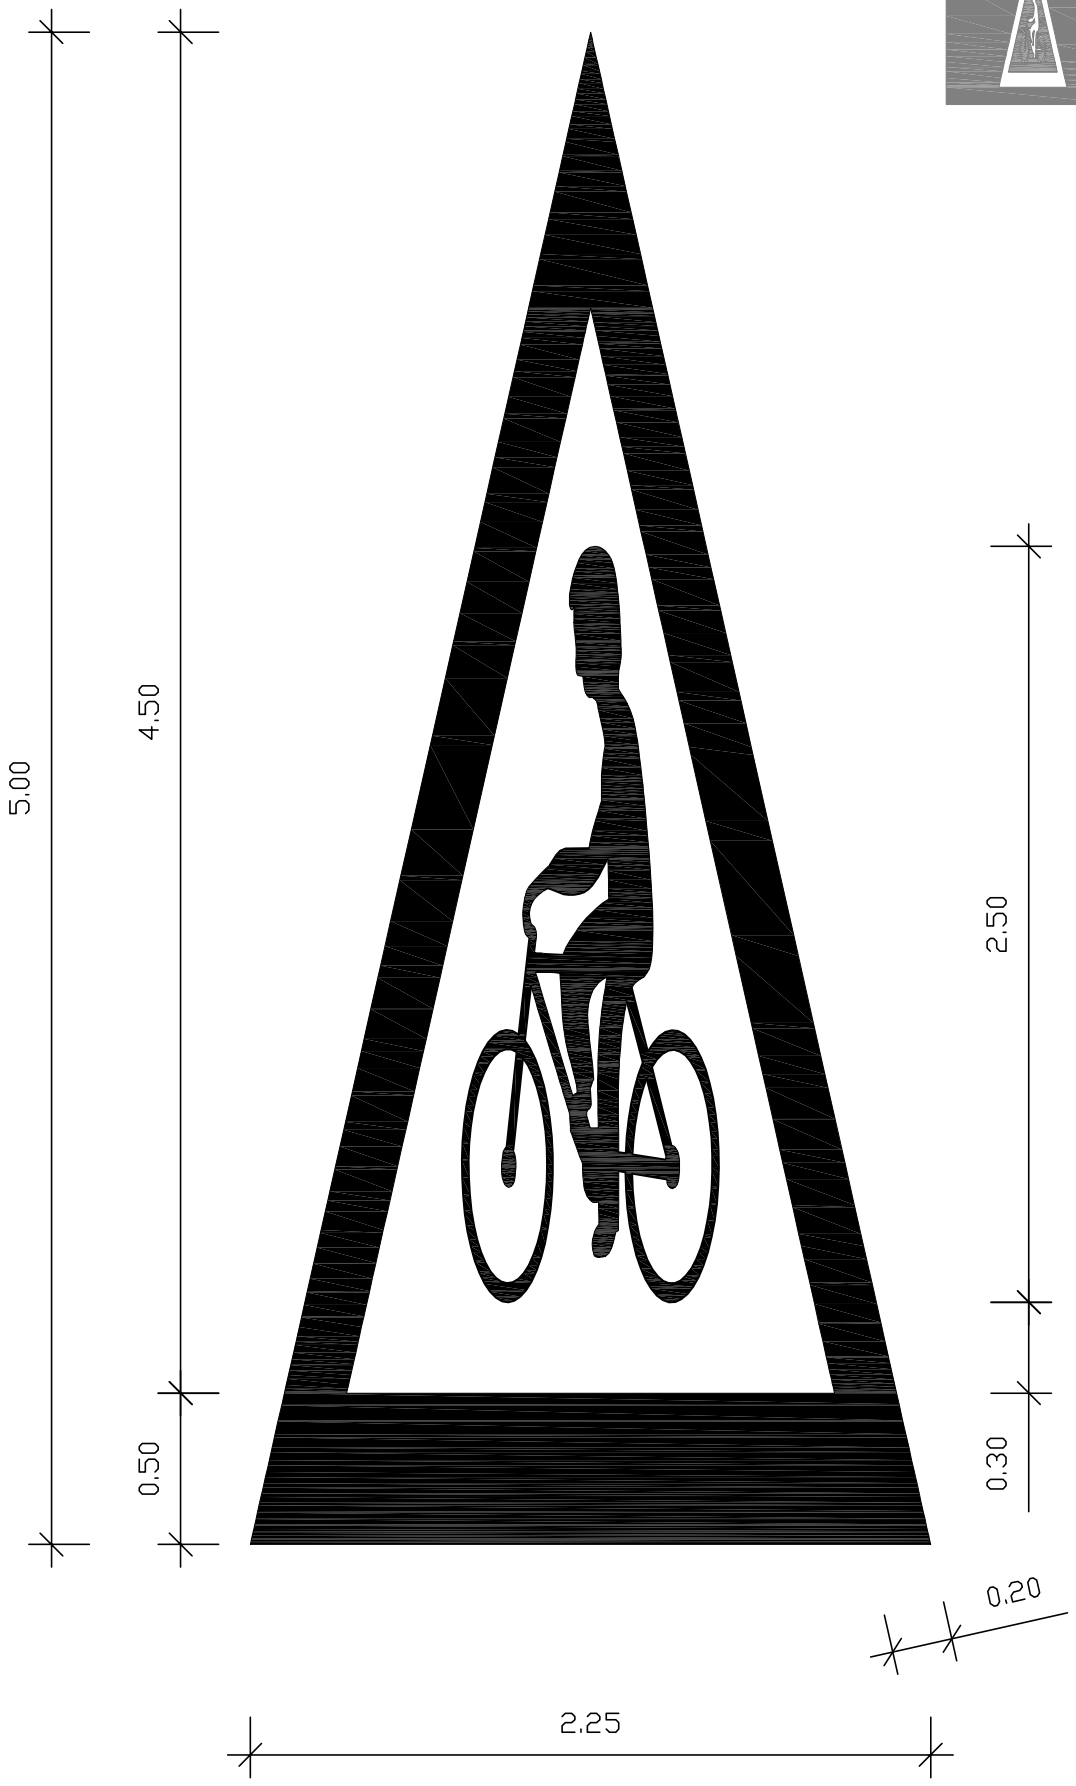



| | | | |
|---|---|---|---|
| **6**<br>**6.2** | **VYBAVENÍ POZEMNÍCH KOMUNIKACÍ**<br>**VODOROVNÉ DOPRAVNÍ ZNAČKY**<br>**č. V 15 Nápis na vozovce**<br>Symbol značky č. A 19 Cyklisté | MINISTERSTVO DOPRAVY<br>ODBOR POZEMNÍCH KOMUNIKACÍ<br>**VZOROVÉ LISTY** | **VL 6**<br>**V 15 - 21**<br>**02.17** |

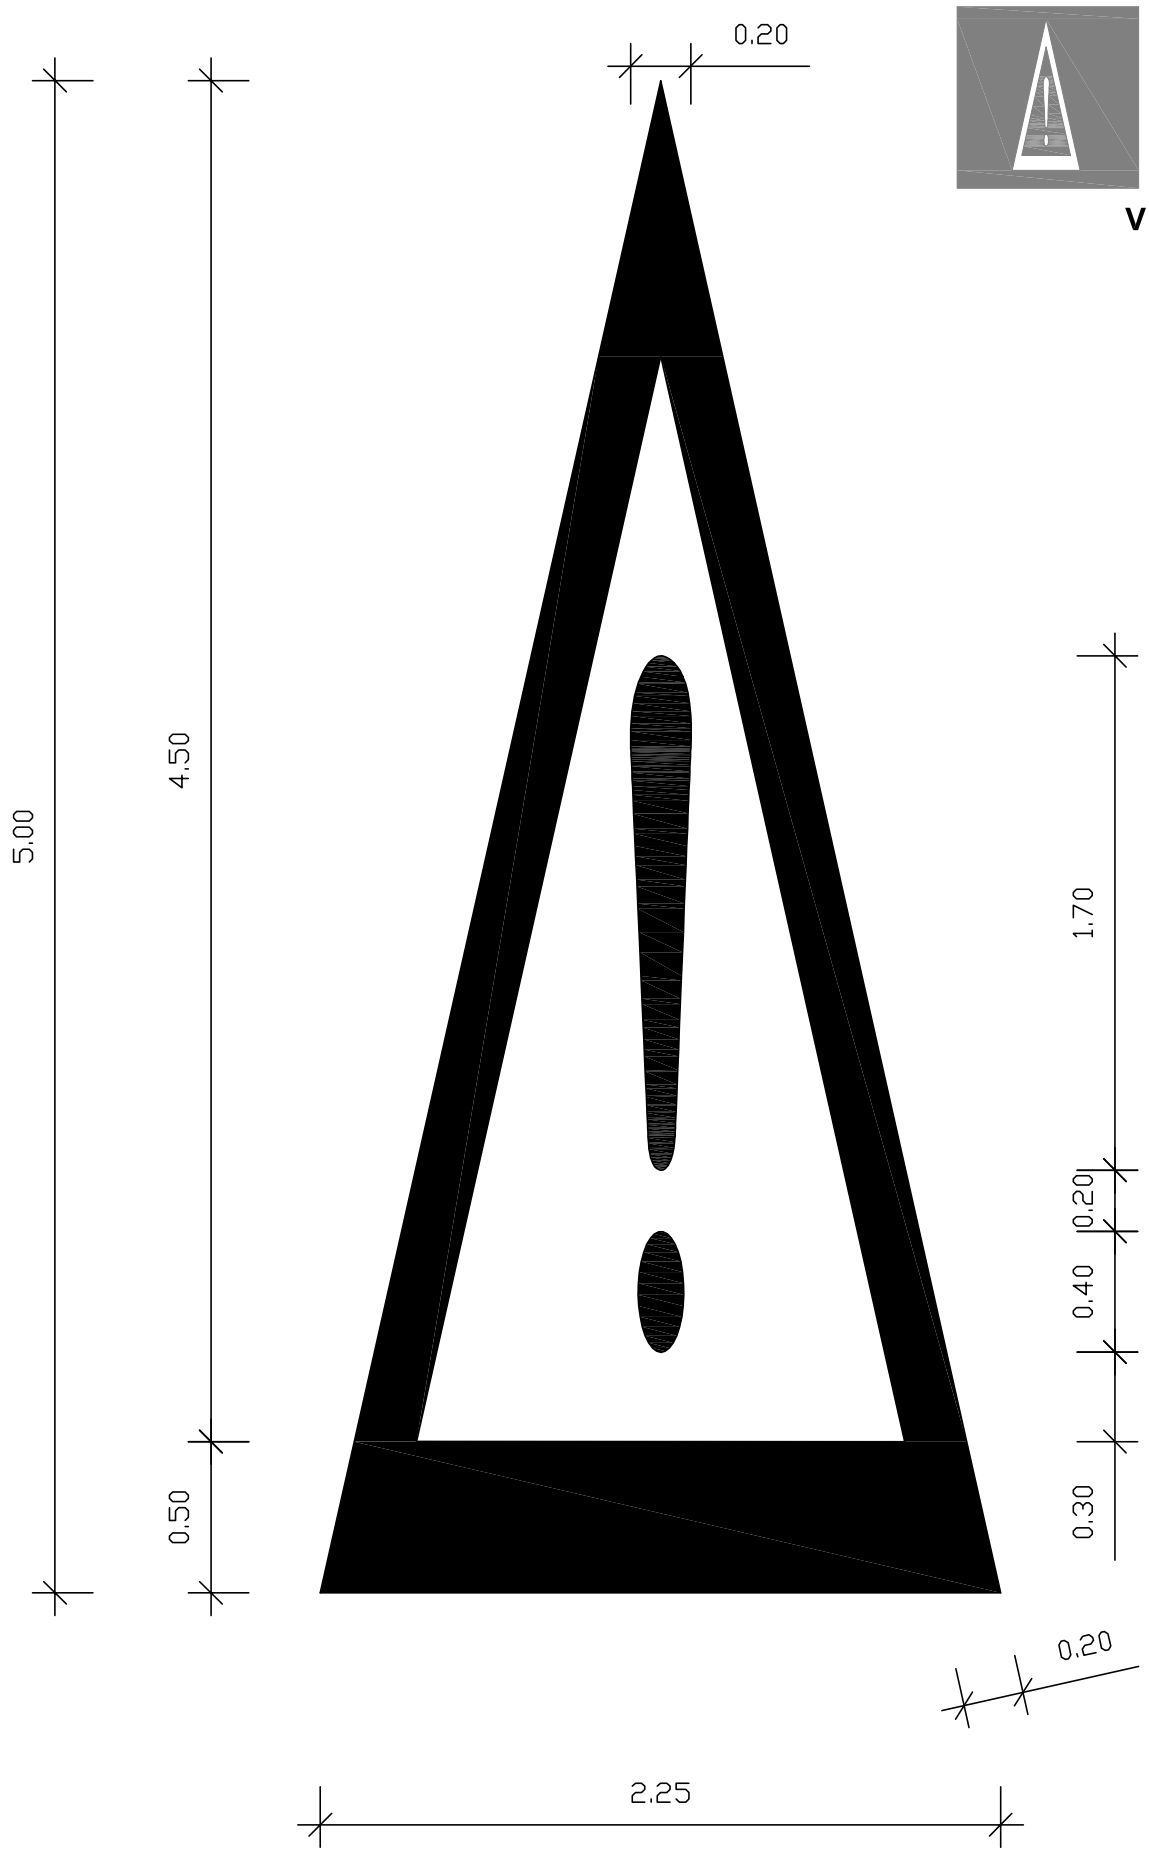




V 15

| | | | |
|---|---|---|---|
| 6<br>6.2 | VYBAVENÍ POZEMNÍCH KOMUNIKACÍ<br>VODOROVNÉ DOPRAVNÍ ZNAČKY<br>č. V 15 Nápis na vozovce<br>Symbol značky č. A 22 jiné nebezpečí | MINISTERSTVO DOPRAVY<br>ODBOR POZEMNÍCH KOMUNIKACÍ<br>VZOROVÉ LISTY | VL 6<br>V 15 - 22<br>02.17 |

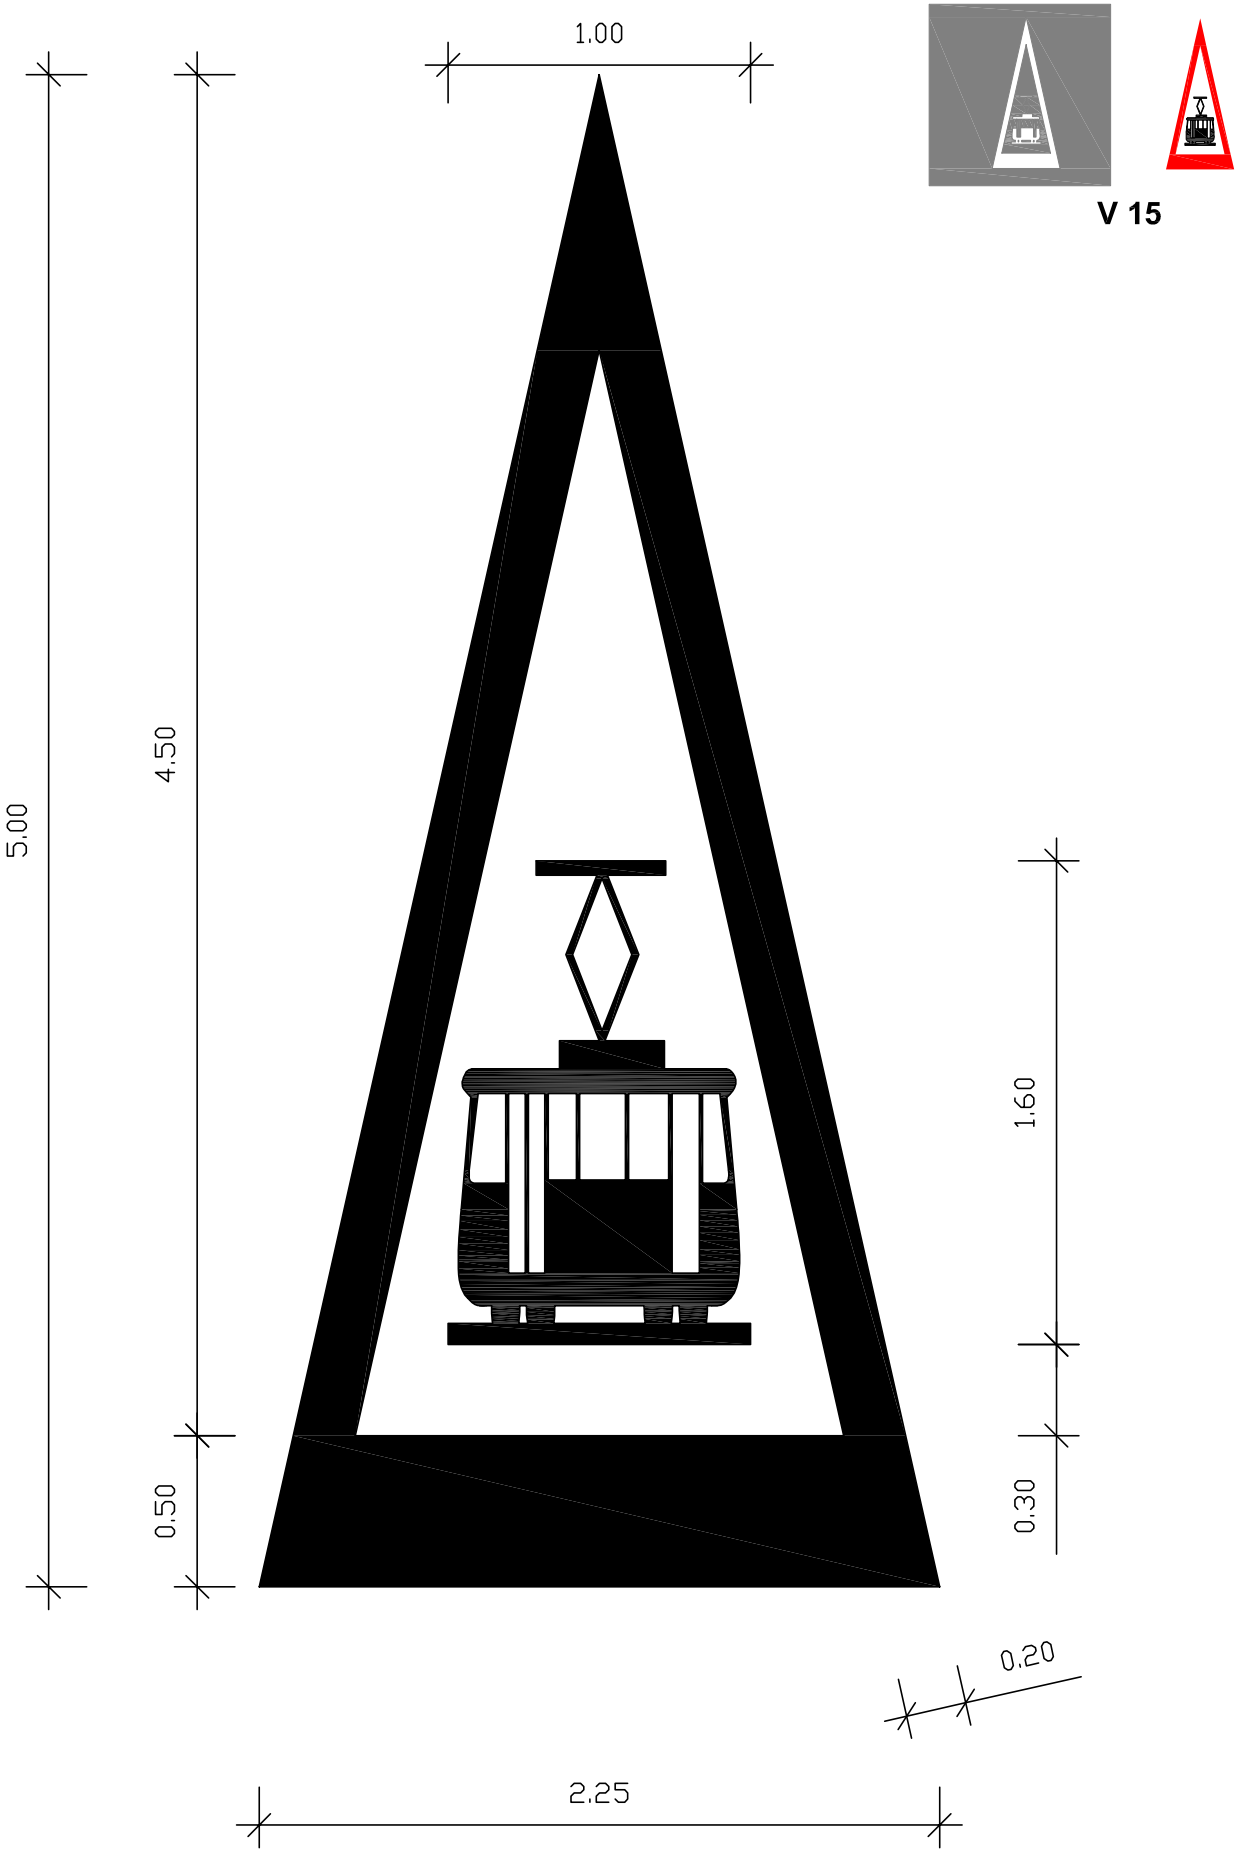








**V 15**

| | | | |
|---|---|---|---|
| **6**<br>**6.2** | **VYBAVENÍ POZEMNÍCH KOMUNIKACÍ**<br>**VODOROVNÉ DOPRAVNÍ ZNAČKY**<br>**č. V 15 Nápis na vozovce**<br>Symbol značky č. A 25 Tramvaj | MINISTERSTVO DOPRAVY<br>ODBOR POZEMNÍCH KOMUNIKACÍ<br>**VZOROVÉ LISTY** | **VL 6**<br>**V 15 - 23**<br>**02.17** |

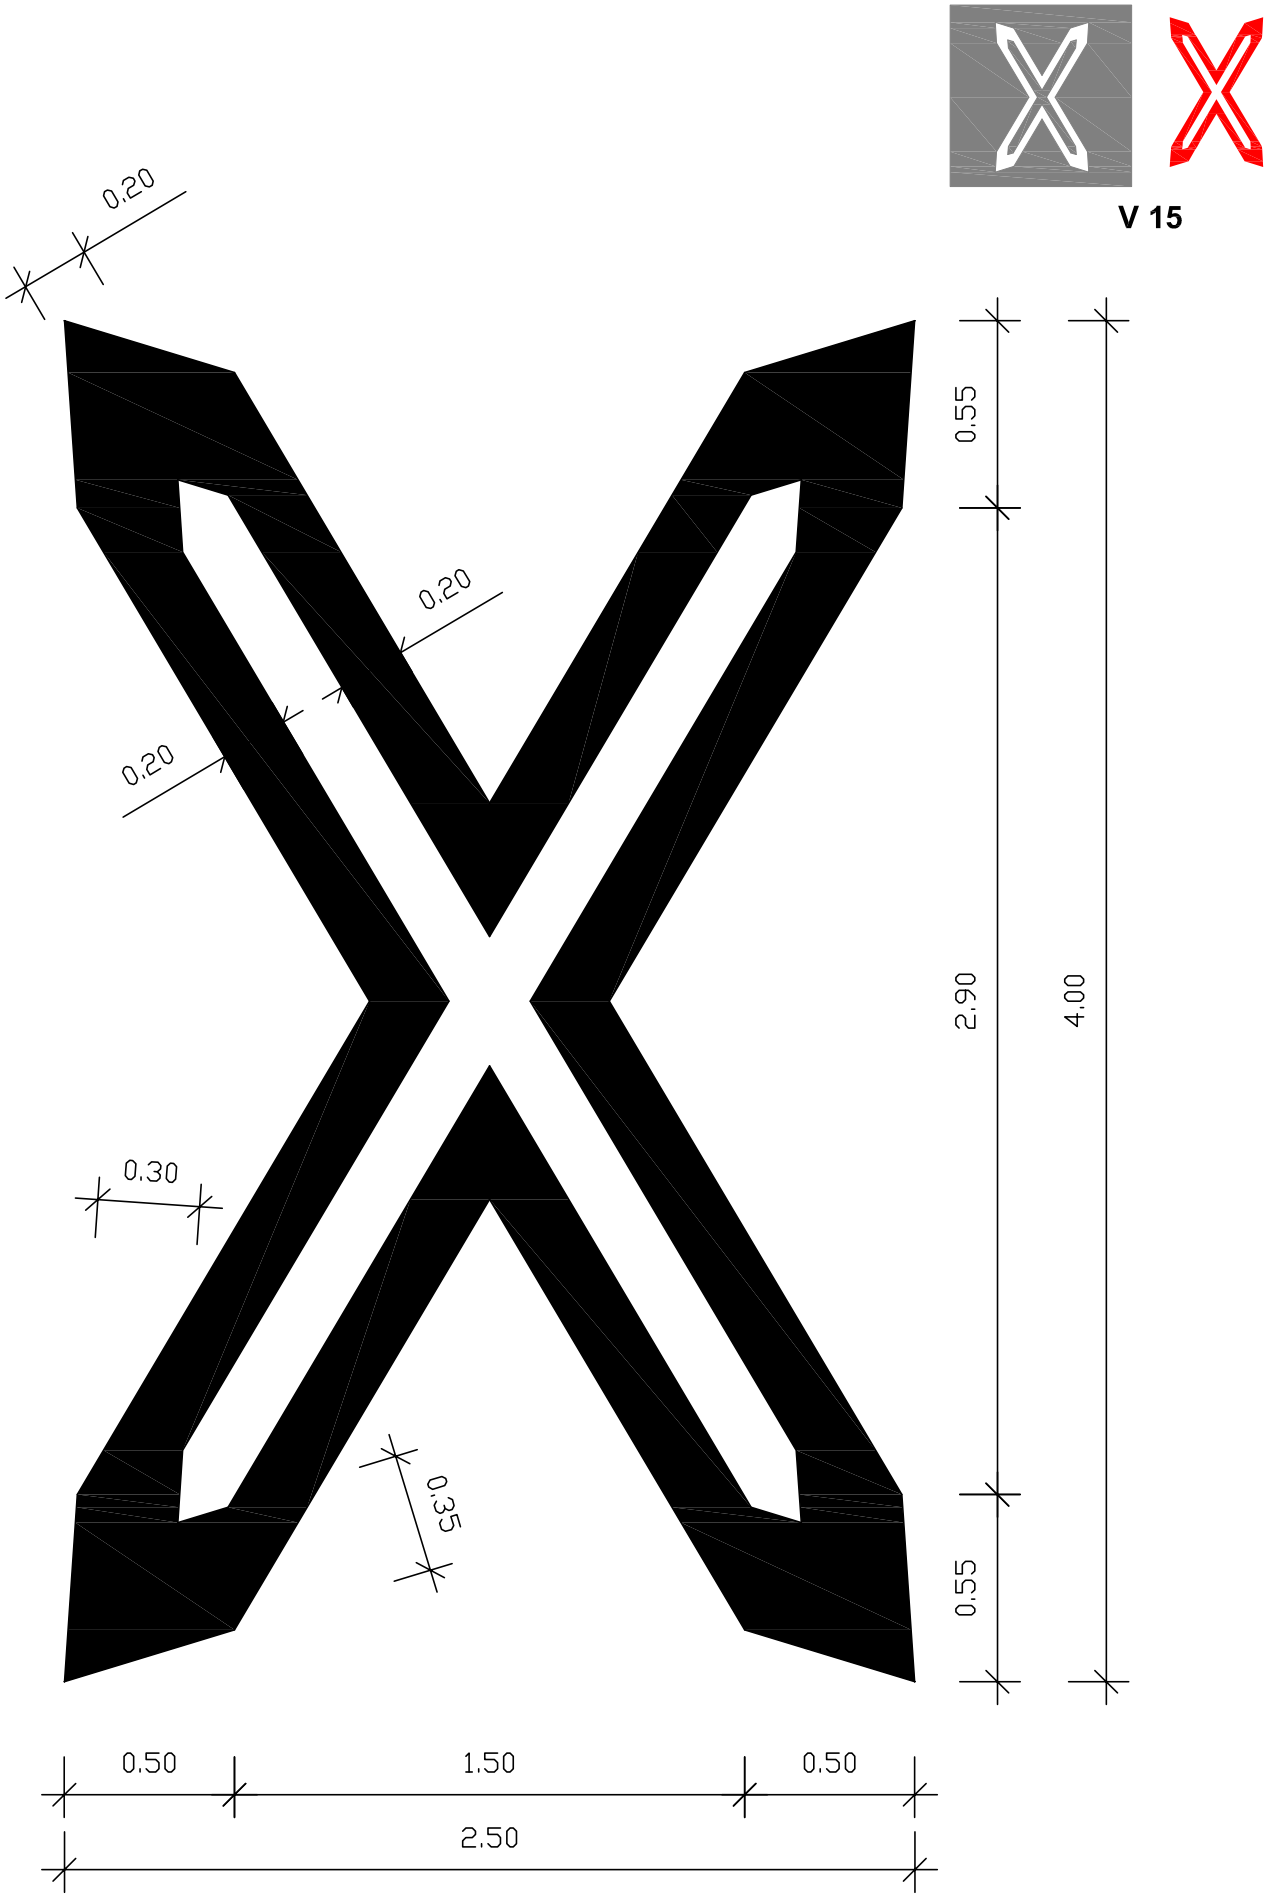


| | | | |
|---|---|---|---|
| **6**<br>**6.2** | **VYBAVENÍ POZEMNÍCH KOMUNIKACÍ**<br>**VODOROVNÉ DOPRAVNÍ ZNAČKY**<br>**č. V 15 Nápis na vozovce**<br>Symbol značky č. A 32a Výstražný kříž pro železniční přejezd jednokolejný | MINISTERSTVO DOPRAVY<br>ODBOR POZEMNÍCH KOMUNIKACÍ<br>**VZOROVÉ LISTY** | **VL 6**<br>**V 15 - 24**<br>**02.17** |

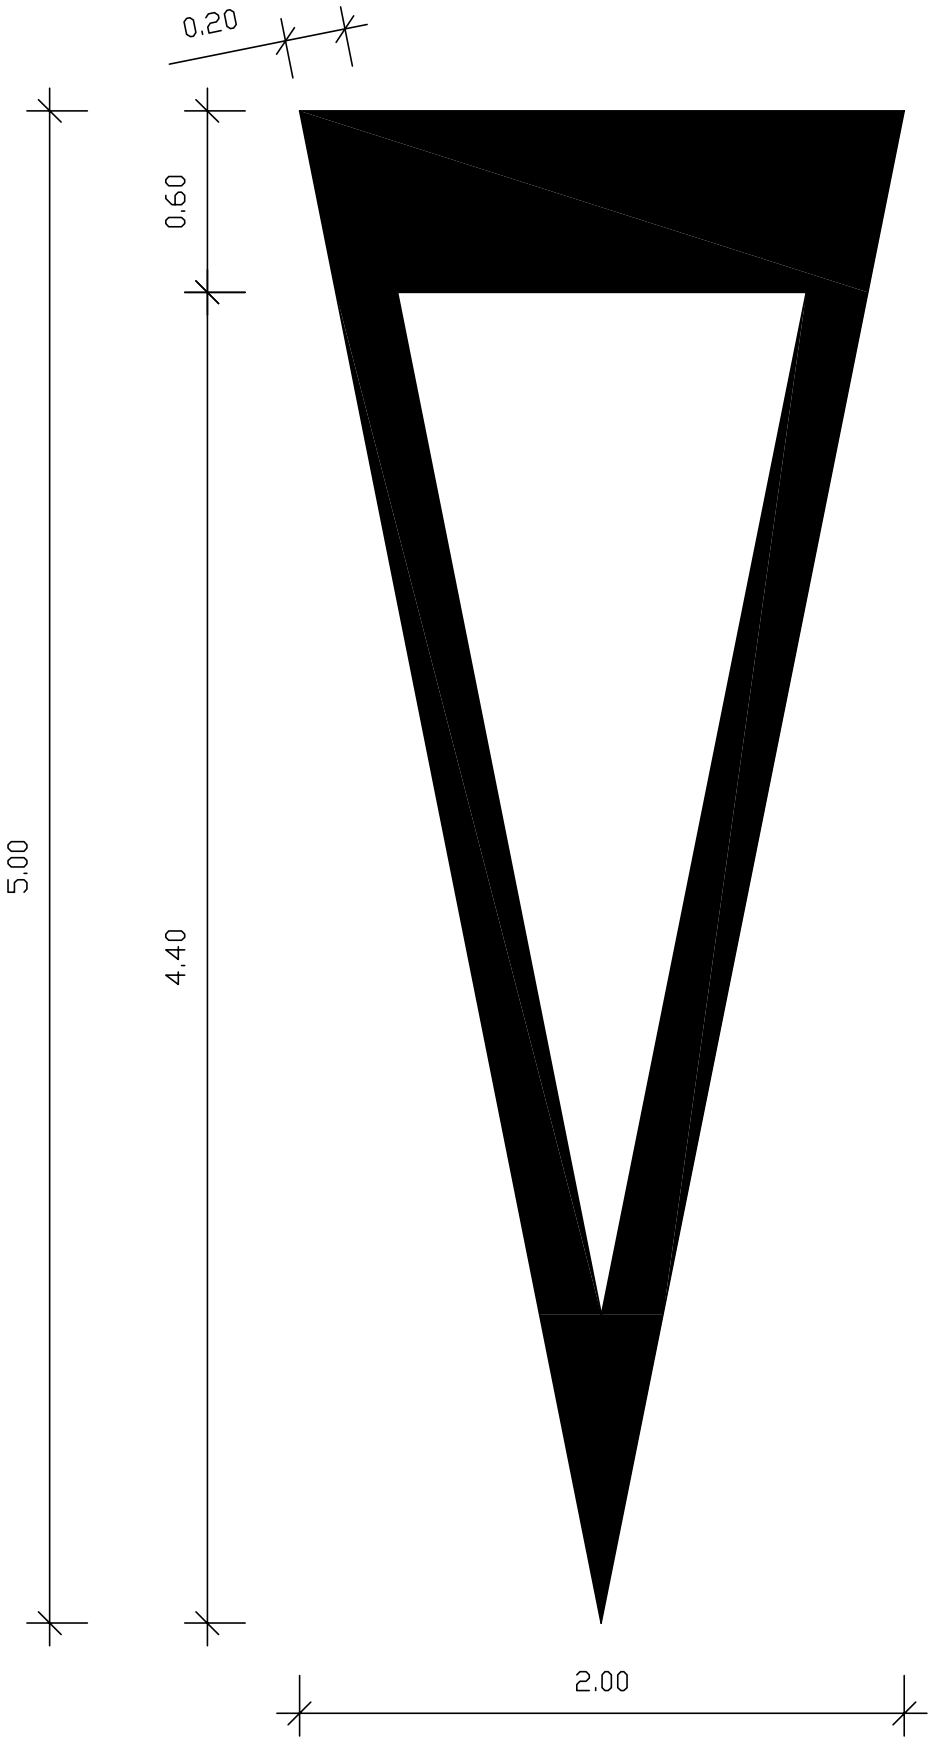


**V 15**

**6 VYBAVENÍ POZEMNÍCH KOMUNIKACÍ**

**6.2 VODOROVNÉ DOPRAVNÍ ZNAČKY**


**č. V 15 Nápis na vozovce**

Symbol značky č. P 4 Dej přednost v jízdě!

MINISTERSTVO DOPRAVY
ODBOR POZEMNÍCH KOMUNIKACÍ
**VZOROVÉ LISTY**


**VL 6**
**V 15 - 25**
**02.17**

V 15

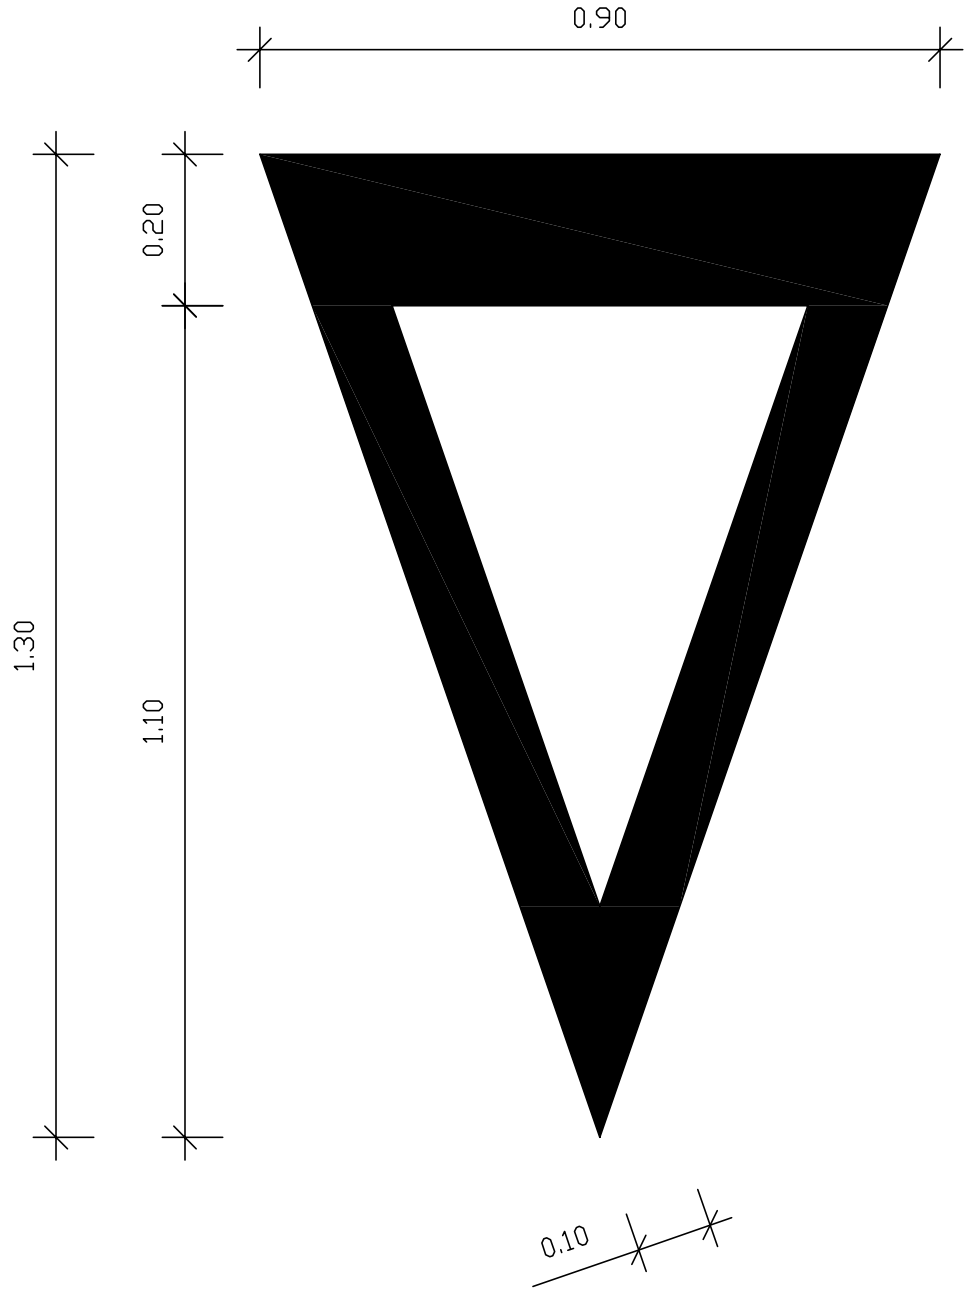


| | | |
|---|---|---|
| **6 VYBAVENÍ POZEMNÍCH KOMUNIKACÍ**<br>**6.2 VODOROVNÉ DOPRAVNÍ ZNAČKY**<br>**č. V 15 Nápis na vozovce**<br>Symbol značky č. P 4 Dej přednost v jízdě! | MINISTERSTVO DOPRAVY<br>ODBOR POZEMNÍCH KOMUNIKACÍ<br>**VZOROVÉ LISTY** | **VL 6**<br>**V 15 - 26**<br>**02.17** |


Pro rychlost > 50 km/h

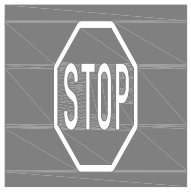






**V 15**

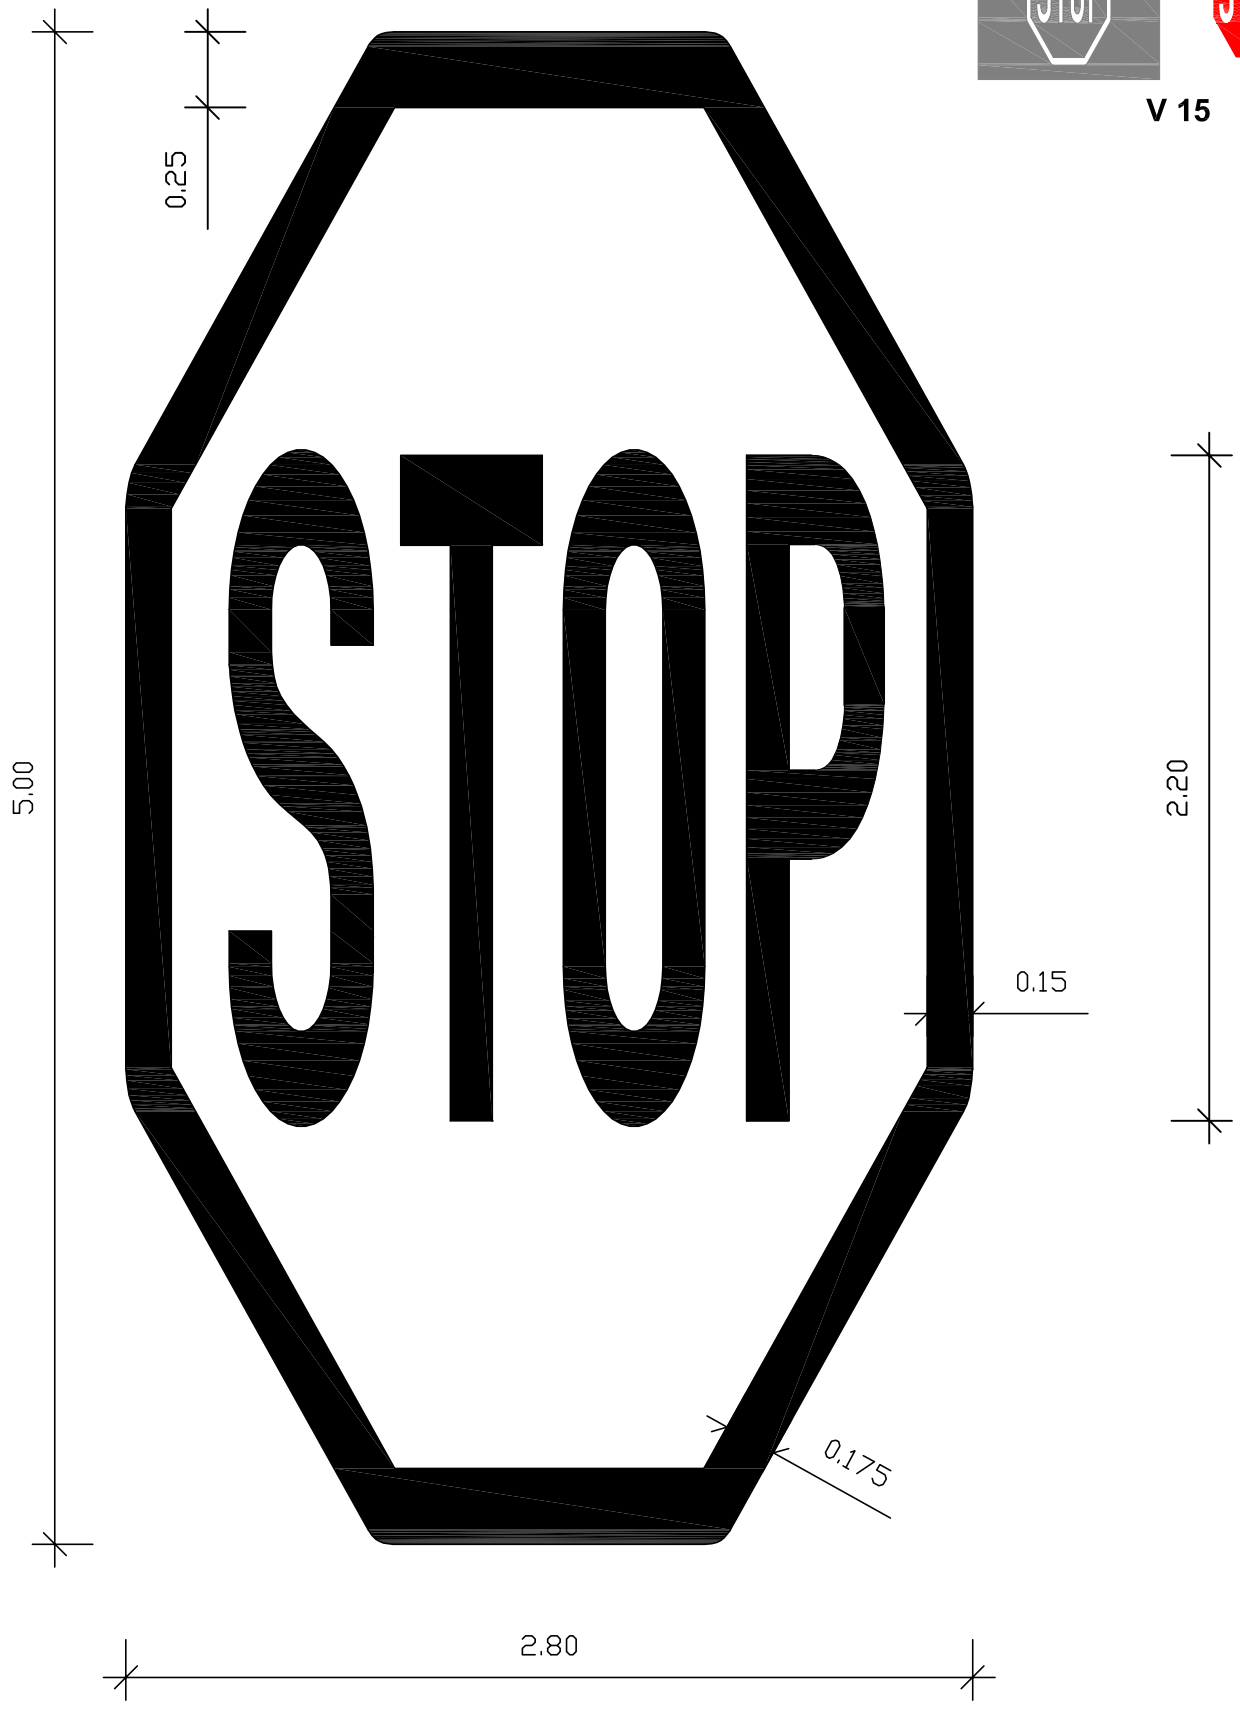


Písmo vychází z VL6.2: V 15-1 – V 15-9. Šířka písmen je zmenšena jen o 25%. Textový údaj se umísťuje symetricky.

| | | | |
|---|---|---|---|
| **6** **VYBAVENÍ POZEMNÍCH KOMUNIKACÍ**<br>**6.2** **VODOROVNÉ DOPRAVNÍ ZNAČKY**<br>**č. V 15 Nápis na vozovce**<br>Symbol značky č. P6 Stůj, dej přednost v jízdě! | MINISTERSTVO DOPRAVY<br>ODBOR POZEMNÍCH KOMUNIKACÍ<br>**VZOROVÉ LISTY** | **VL 6**<br>**V 15 - 27**<br>**02.17** |


Pro rychlost ≤ 50 km/h

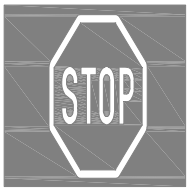







**V 15**

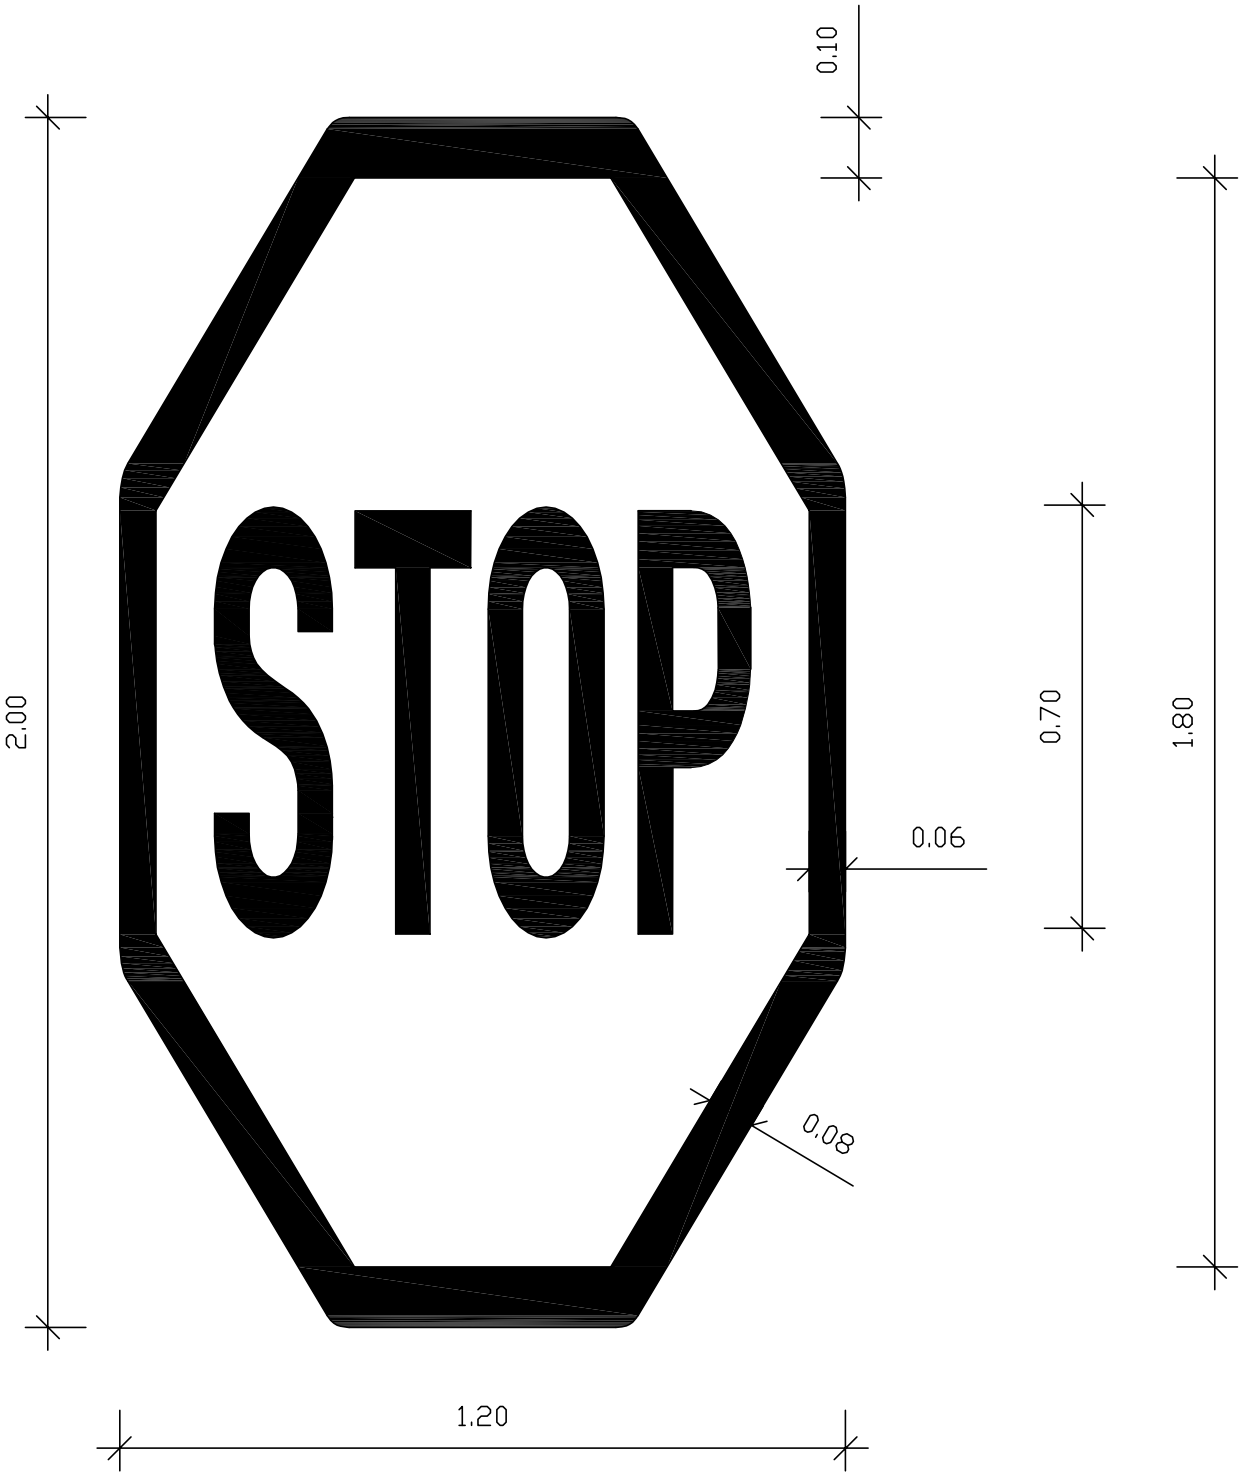


Písmo vychází z VL6.2: V 15-1 – V 15-9. Šířka písmen je zmenšena o 70%.
Textový údaj se umísťuje symetricky.

| | | |
|---|---|---|
| **6 VYBAVENÍ POZEMNÍCH KOMUNIKACÍ**<br>**6.2 VODOROVNÉ DOPRAVNÍ ZNAČKY**<br>**č. V 15 Nápis na vozovce**<br>**Symbol značky č. P6 Stůj, dej přednost v jízdě!** | **MINISTERSTVO DOPRAVY**<br>**ODBOR POZEMNÍCH KOMUNIKACÍ**<br>**VZOROVÉ LISTY** | **VL 6**<br>**V 15 - 28**<br>**02.17** |

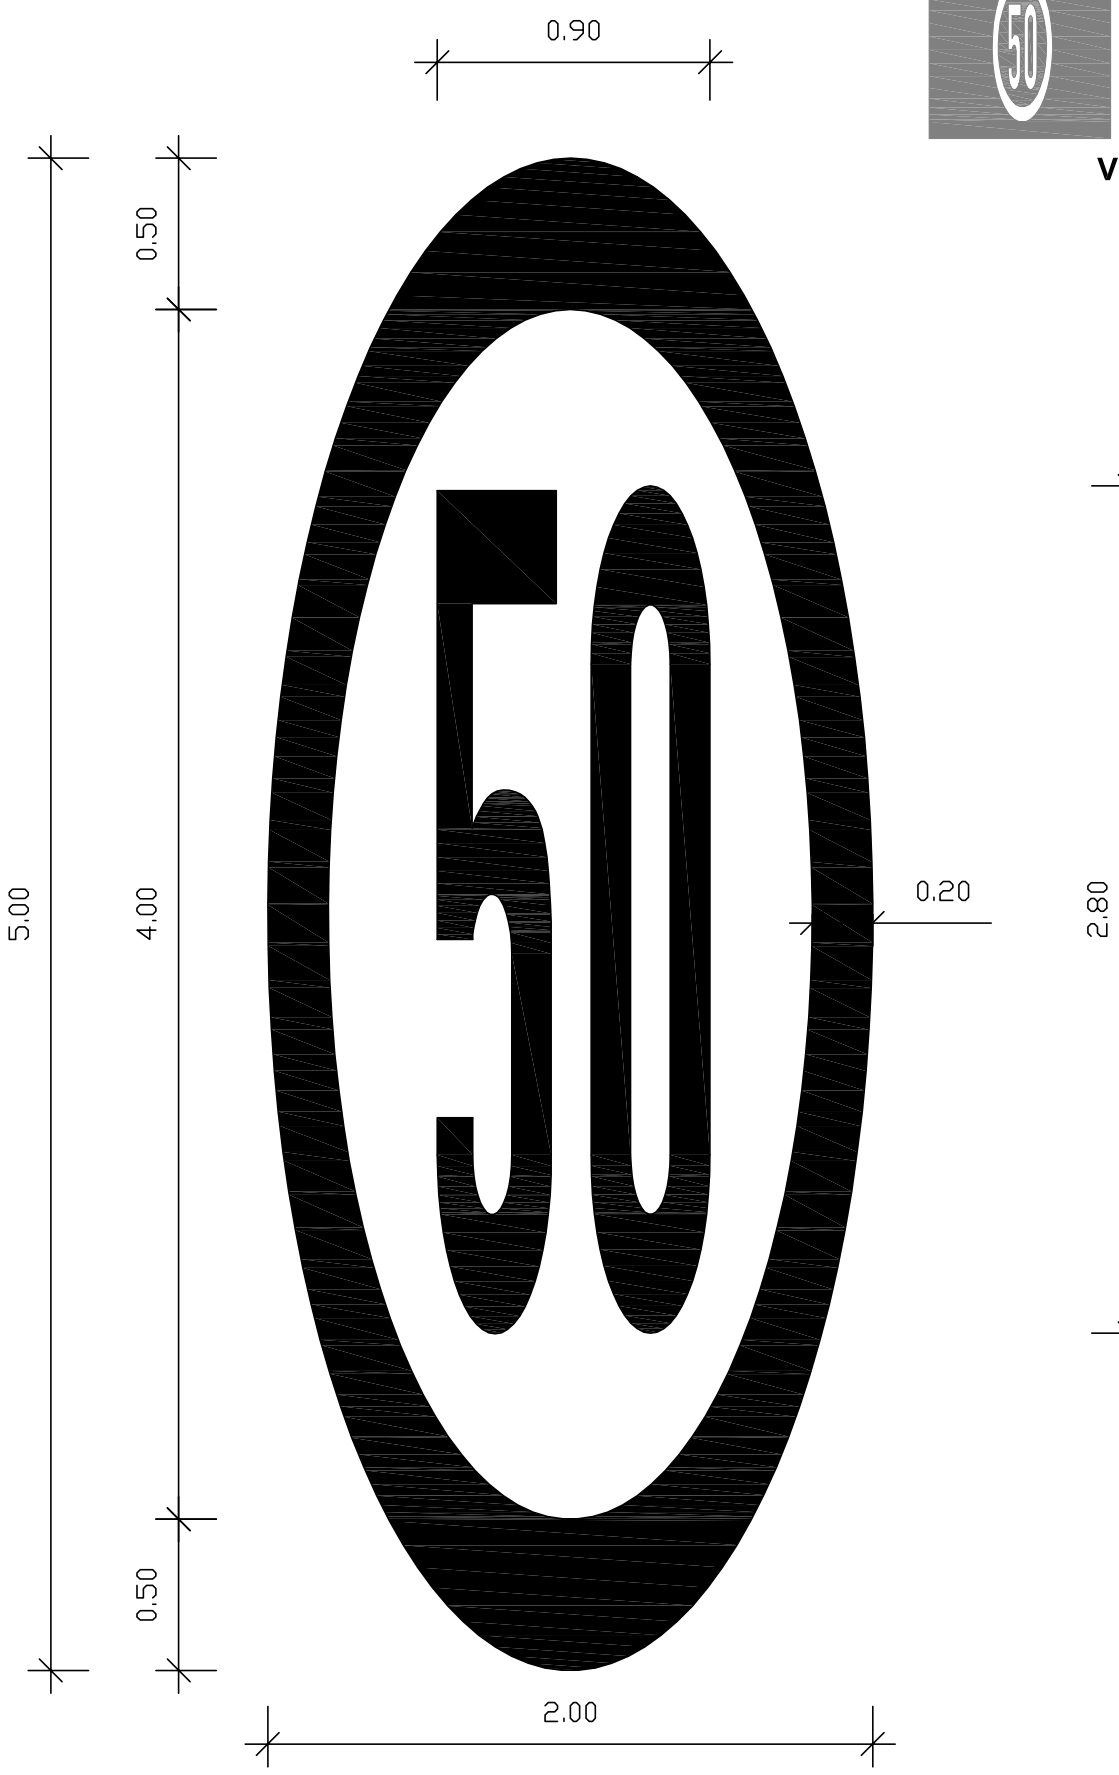

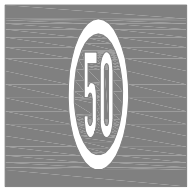


**V 15**


Písmo vychází z VL6.2: V 15-10 – V 15-13. Písmo je zmenšeno o 30%.

| | | | |
|---|---|---|---|
| **6** **VYBAVENÍ POZEMNÍCH KOMUNIKACÍ**<br>**6.2** **VODOROVNÉ DOPRAVNÍ ZNAČKY**<br>**č. V 15 Nápis na vozovce**<br>Symbol značky č. B 20a Nejvyšší dovolená rychlost | MINISTERSTVO DOPRAVY<br>ODBOR POZEMNÍCH KOMUNIKACÍ<br>**VZOROVÉ LISTY** | **VL 6**<br>**V 15 - 29**<br>**02.17** |

Pro rychlost > 50 km/h

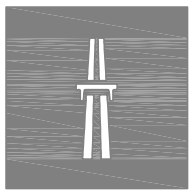


**V 15**

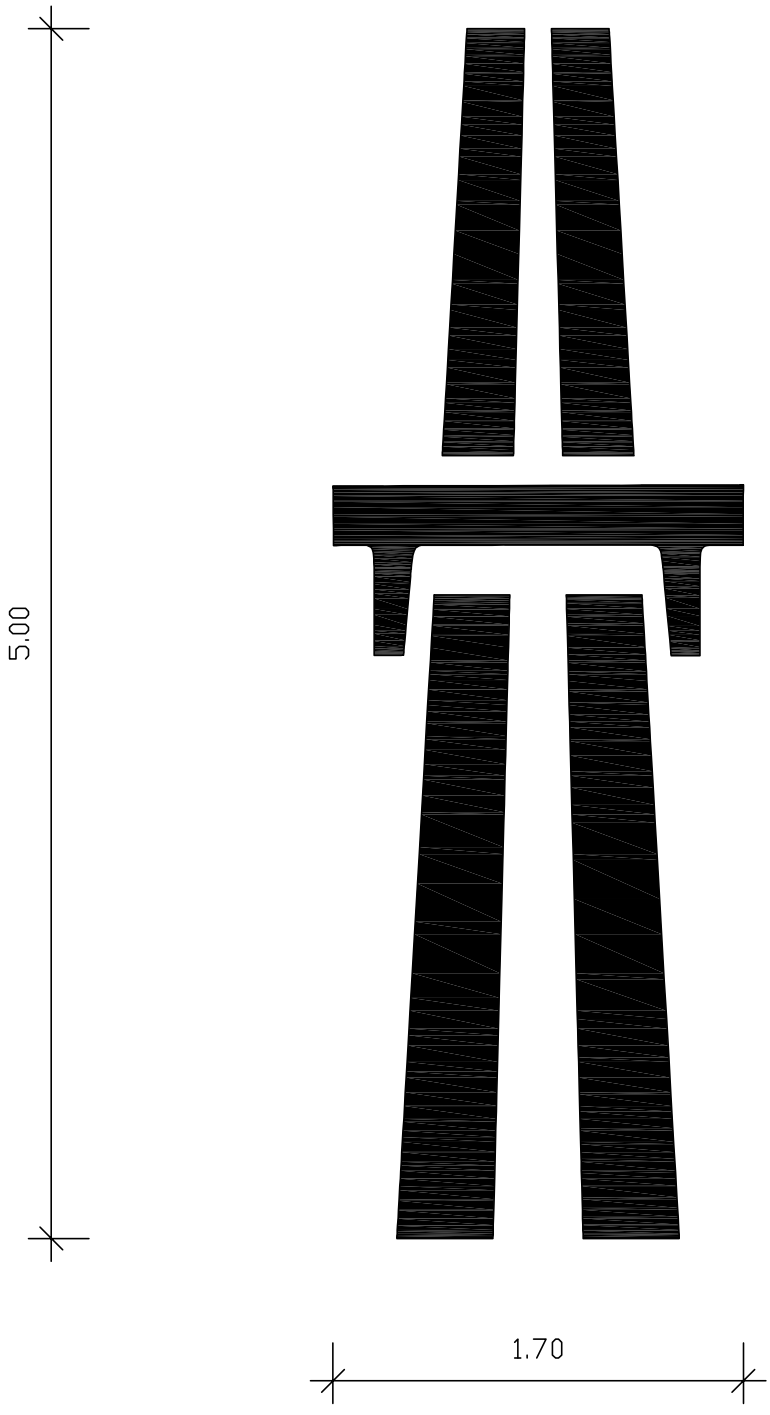



| | | | |
|---|---|---|---|
| **6** **VYBAVENÍ POZEMNÍCH KOMUNIKACÍ**<br>**6.2** **VODOROVNÉ DOPRAVNÍ ZNAČKY**<br>**č. V 15 Nápis na vozovce**<br>Symbol značky č. IZ 1a Dálnice | MINISTERSTVO DOPRAVY<br>ODBOR POZEMNÍCH KOMUNIKACÍ<br>**VZOROVÉ LISTY** | **VL 6**<br>**V 15 - 30**<br>**02.17** |

Pro rychlost > 50 km/h

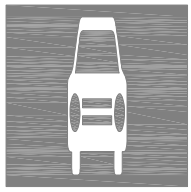

**V 15**

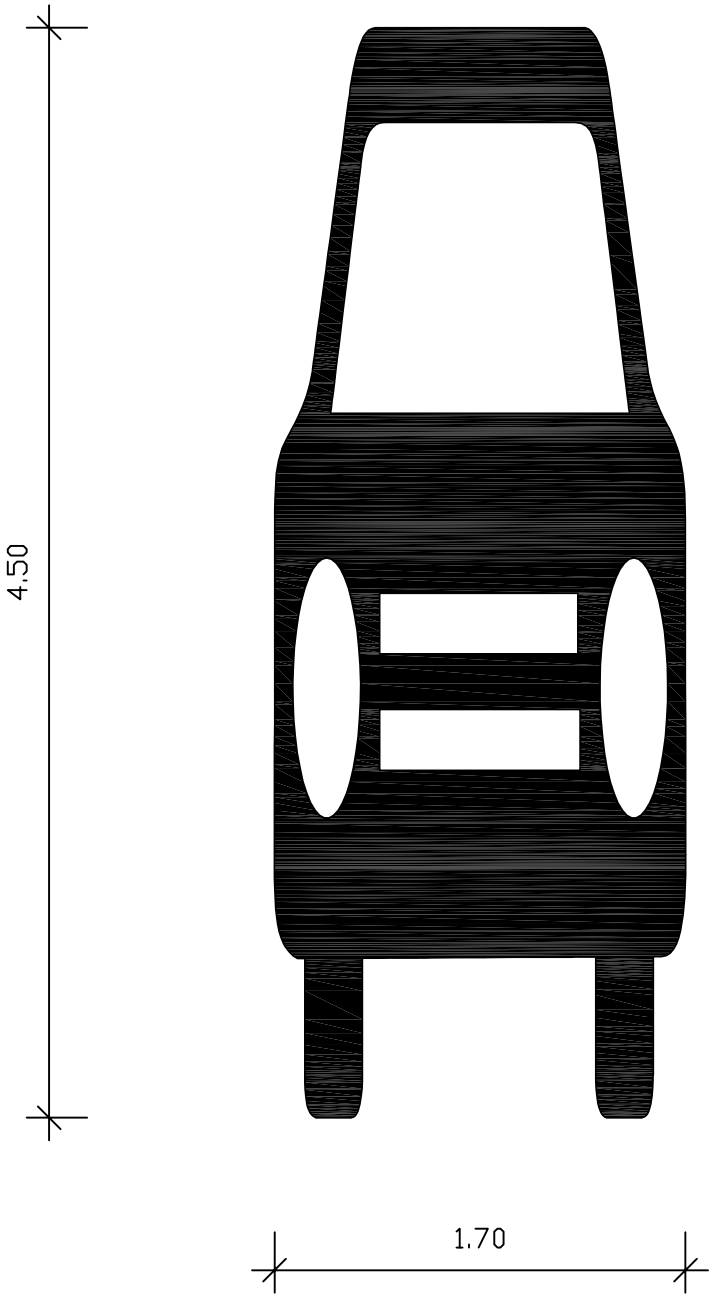


**6 VYBAVENÍ POZEMNÍCH KOMUNIKACÍ**

**6.2 VODOROVNÉ DOPRAVNÍ ZNAČKY**


**č. V 15 Nápis na vozovce**

Symbol značky č. IZ 2a Silnice pro motorová vozidla


MINISTERSTVO DOPRAVY
ODBOR POZEMNÍCH KOMUNIKACÍ
**VZOROVÉ LISTY**

**VL 6**
**V 15 - 31**
**02.17**

Pro rychlost > 50 km/h

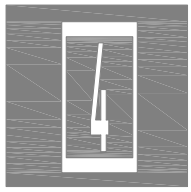


V 15

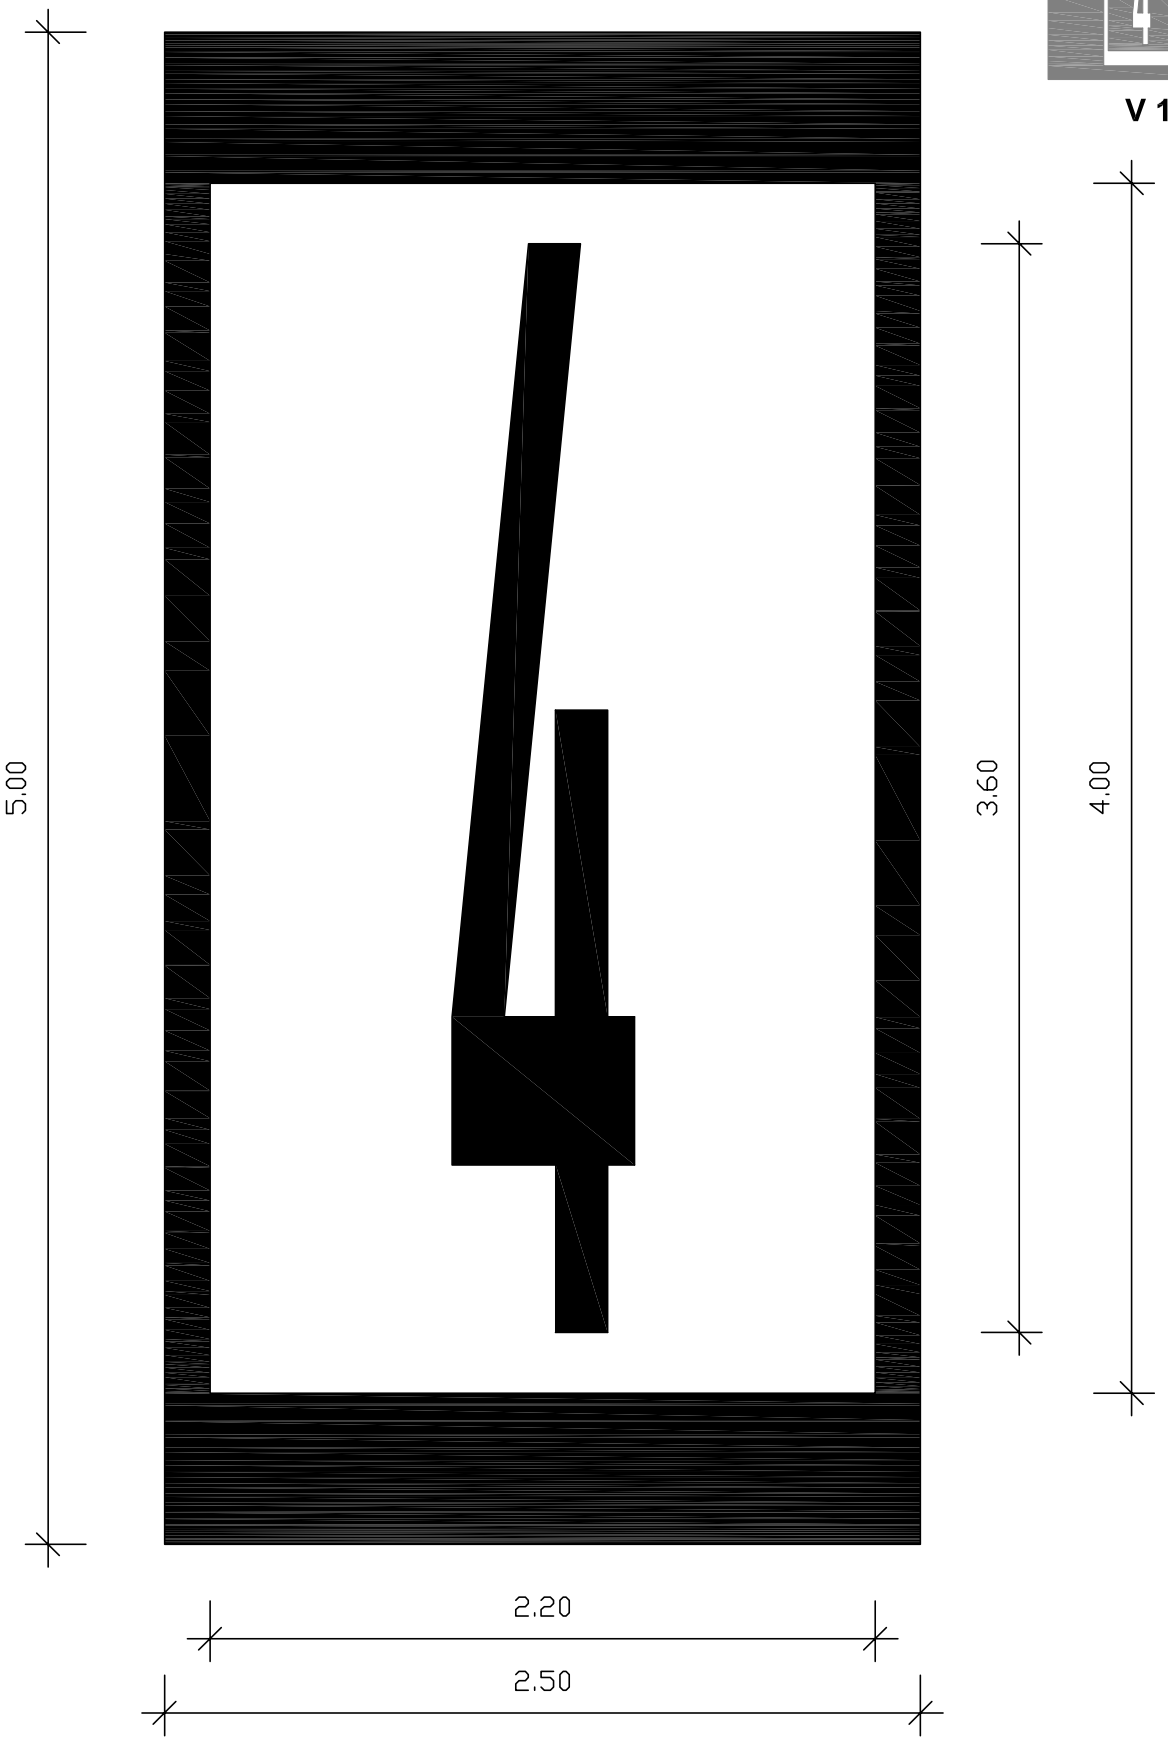


Písmo vychází z VL6.2: V 15-10 – V 15-13. Číselný údaj se umísťuje symetricky.

| | | | |
|---|---|---|---|
| **6** **VYBAVENÍ POZEMNÍCH KOMUNIKACÍ**<br>**6.2** **VODOROVNÉ DOPRAVNÍ ZNAČKY**<br>**č. V 15 Nápis na vozovce**<br>**Symbol značky č. IS 16b Číslo silnice** | **MINISTERSTVO DOPRAVY**<br>**ODBOR POZEMNÍCH KOMUNIKACÍ**<br>**VZOROVÉ LISTY** | **VL 6**<br>**V 15 - 32**<br>**02.17** |

Pro rychlost > 50 km/h

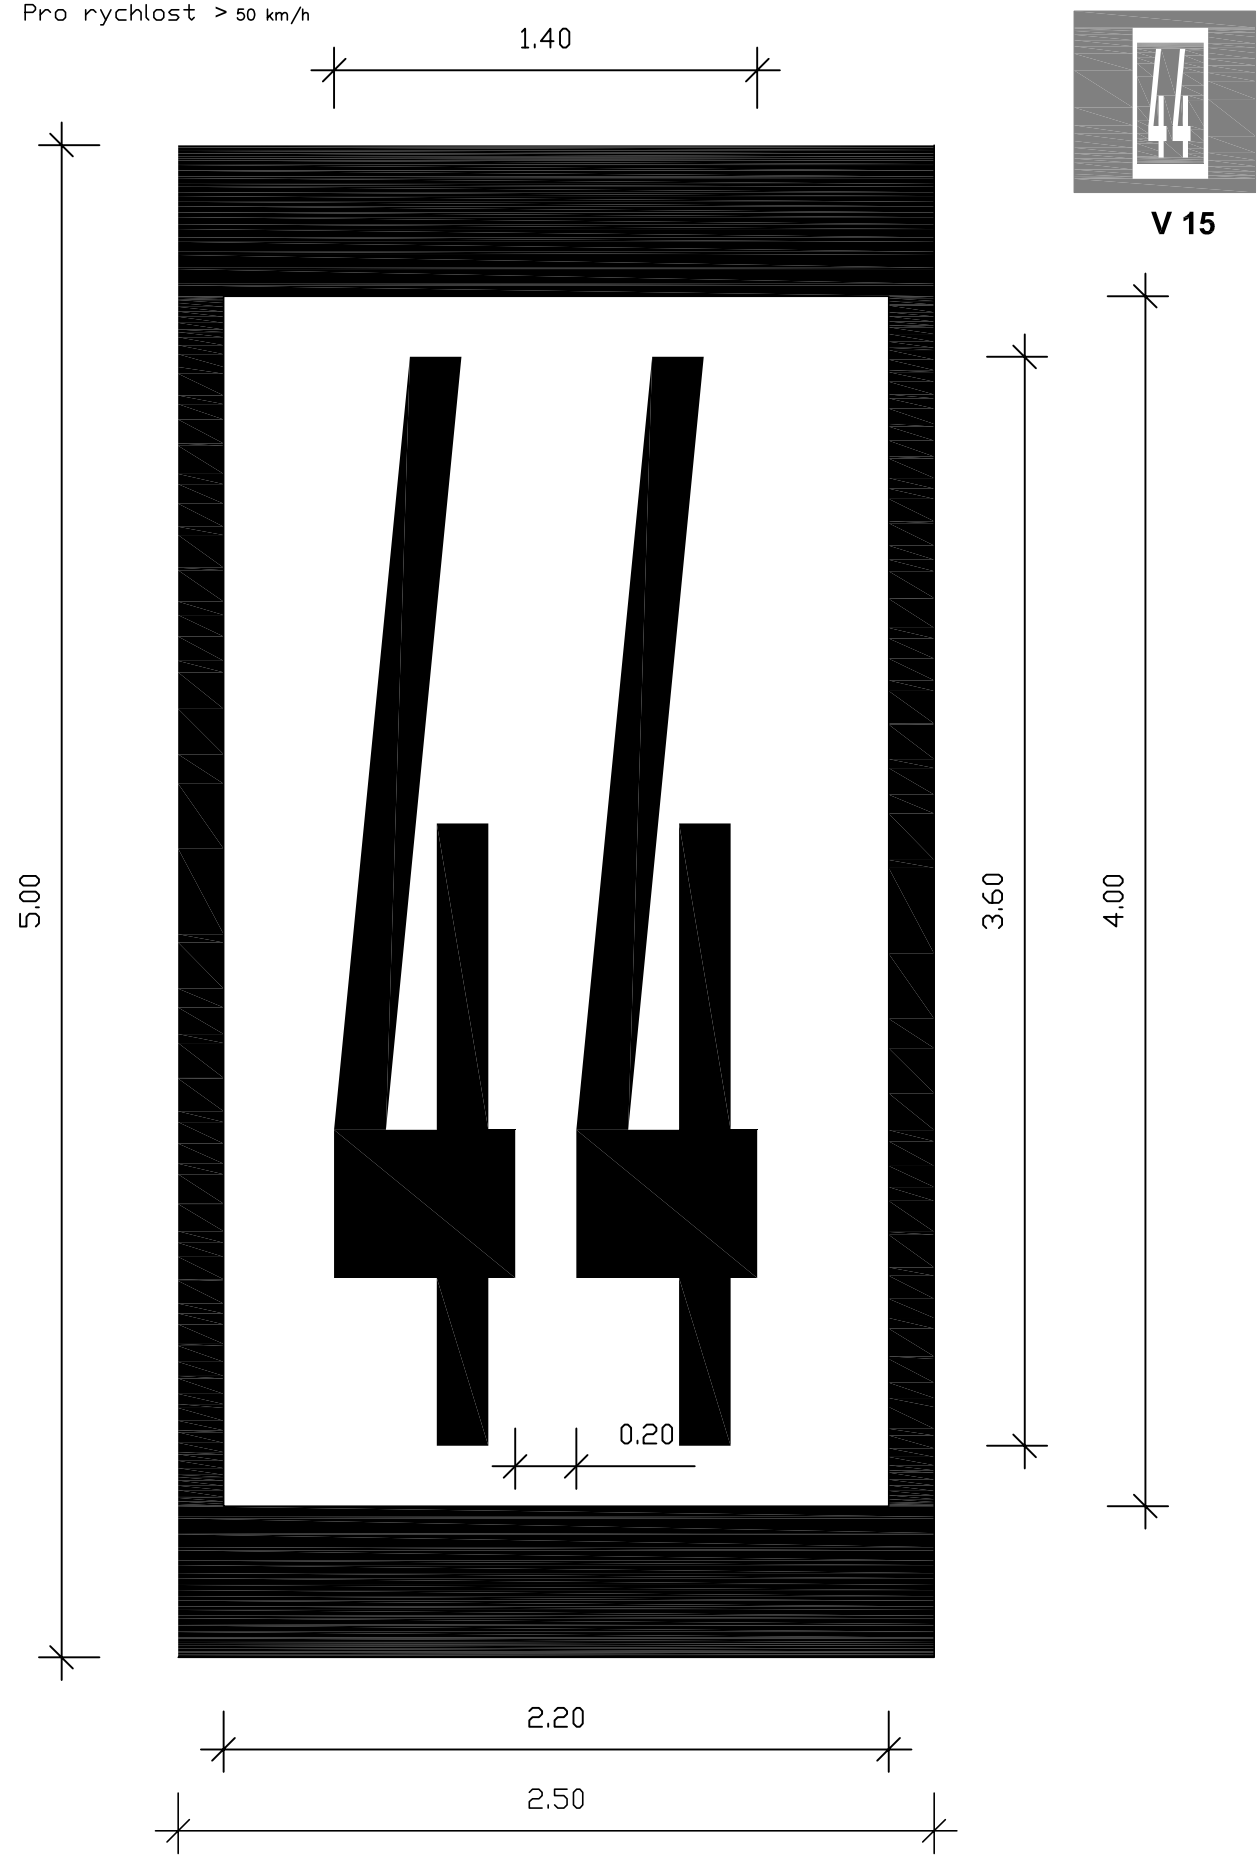



V 15


Písmo vychází z VL6: V 15-1 – V 15-13. Číselný údaj se umísťuje symetricky.

| | | | |
|---|---|---|---|
| **6** **VYBAVENÍ POZEMNÍCH KOMUNIKACÍ**<br>**6.2** **VODOROVNÉ DOPRAVNÍ ZNAČKY**<br>**č. V 15 Nápis na vozovce**<br>**Symbol značky č. IS 16b Číslo silnice** | **MINISTERSTVO DOPRAVY**<br>**ODBOR POZEMNÍCH KOMUNIKACÍ**<br>**VZOROVÉ LISTY** | **VL 6**<br>**V 15 - 33**<br>**02.17** |

Pro rychlost > 50 km/h

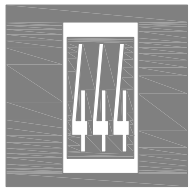

**V 15**

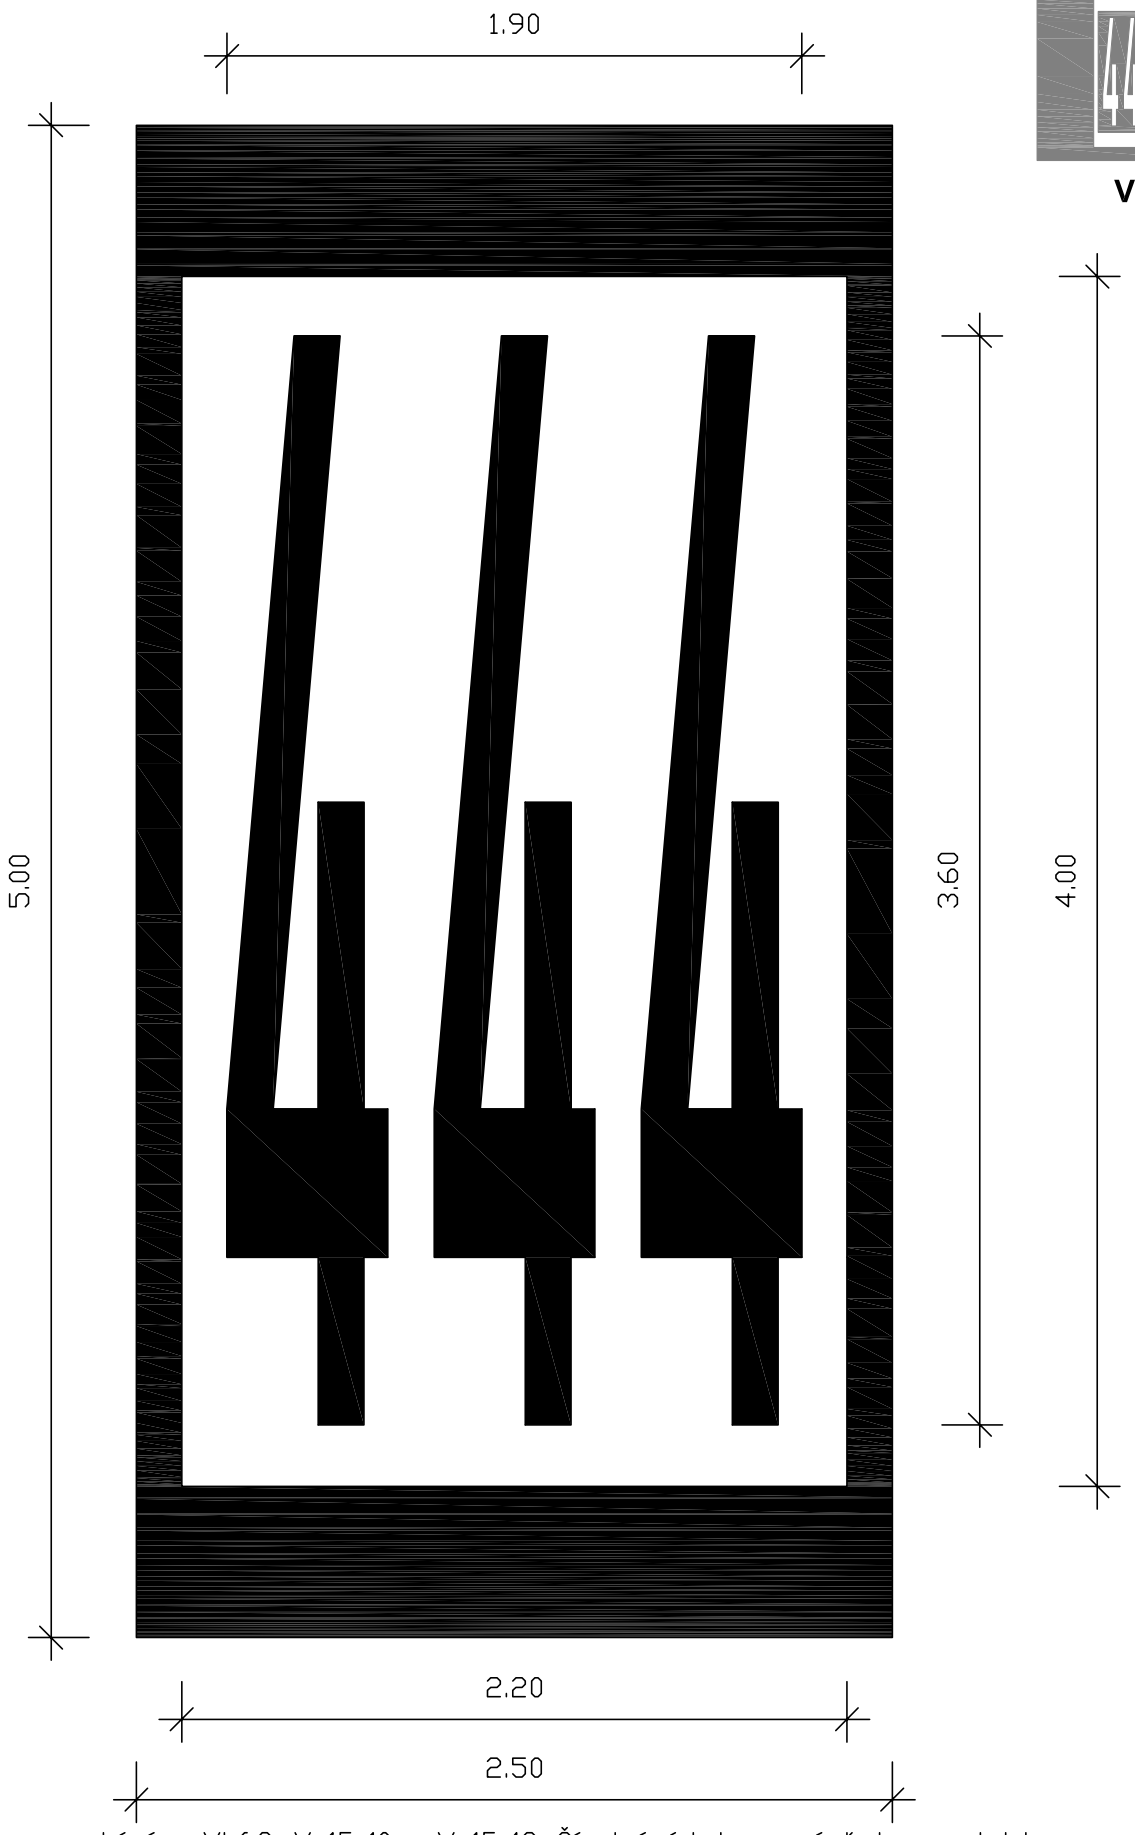



Písmo vychází z VL6.2: V 15-10 – V 15-13. Číselný údaj se umísťuje symetricky. Komprese v horizontálním směru 12 %.

| | | | |
|---|---|---|---|
| **6** **VYBAVENÍ POZEMNÍCH KOMUNIKACÍ**<br>**6.2** **VODOROVNÉ DOPRAVNÍ ZNAČKY**<br>**č. V 15 Nápis na vozovce**<br>**Symbol značky č. IS 16b Číslo silnice** | **MINISTERSTVO DOPRAVY**<br>**ODBOR POZEMNÍCH KOMUNIKACÍ**<br>**VZOROVÉ LISTY** | **VL 6**<br>**V 15 - 34**<br>**02.17** |

Pro rychlost > 50 km/h

V 15

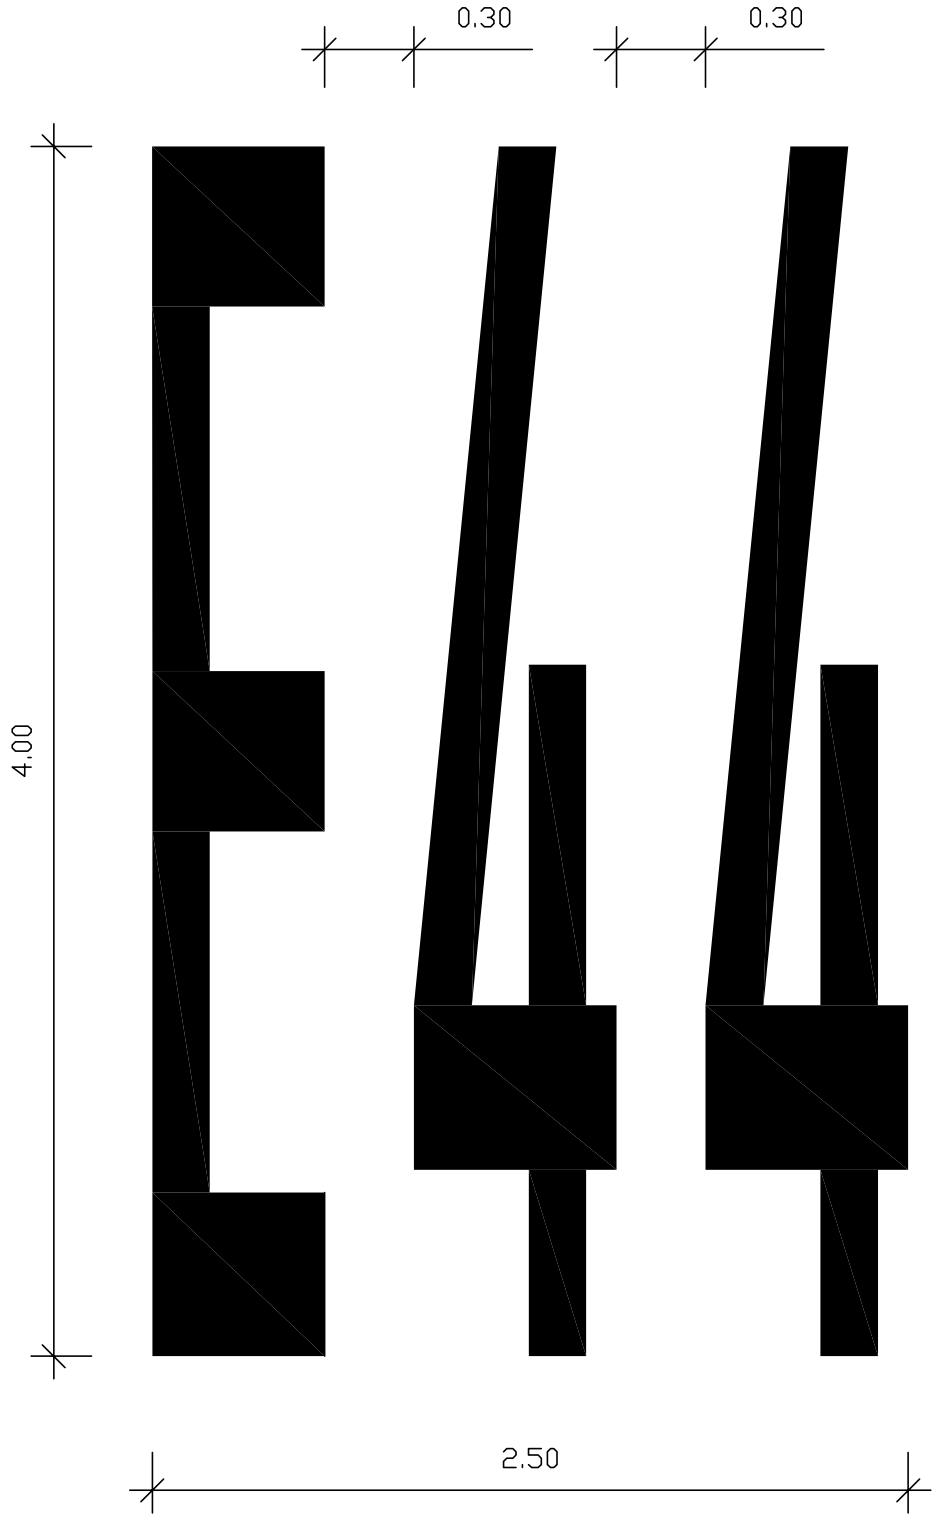



Písmo vychází z VL6.2: V 15-1 - V 15-13.

| | | | |
|---|---|---|---|
| **6** **VYBAVENÍ POZEMNÍCH KOMUNIKACÍ**<br>**6.2** **VODOROVNÉ DOPRAVNÍ ZNAČKY**<br>**č. V15 Nápis na vozovce**<br>**Symbol značky č. IS 17 Číslo silnice pro mezinárodní provoz** | **MINISTERSTVO DOPRAVY**<br>**ODBOR POZEMNÍCH KOMUNIKACÍ**<br>**VZOROVÉ LISTY** | **VL 6**<br>**V 15 - 35**<br>**02.17** |

Pro rychlost > 50 km/h

V 15

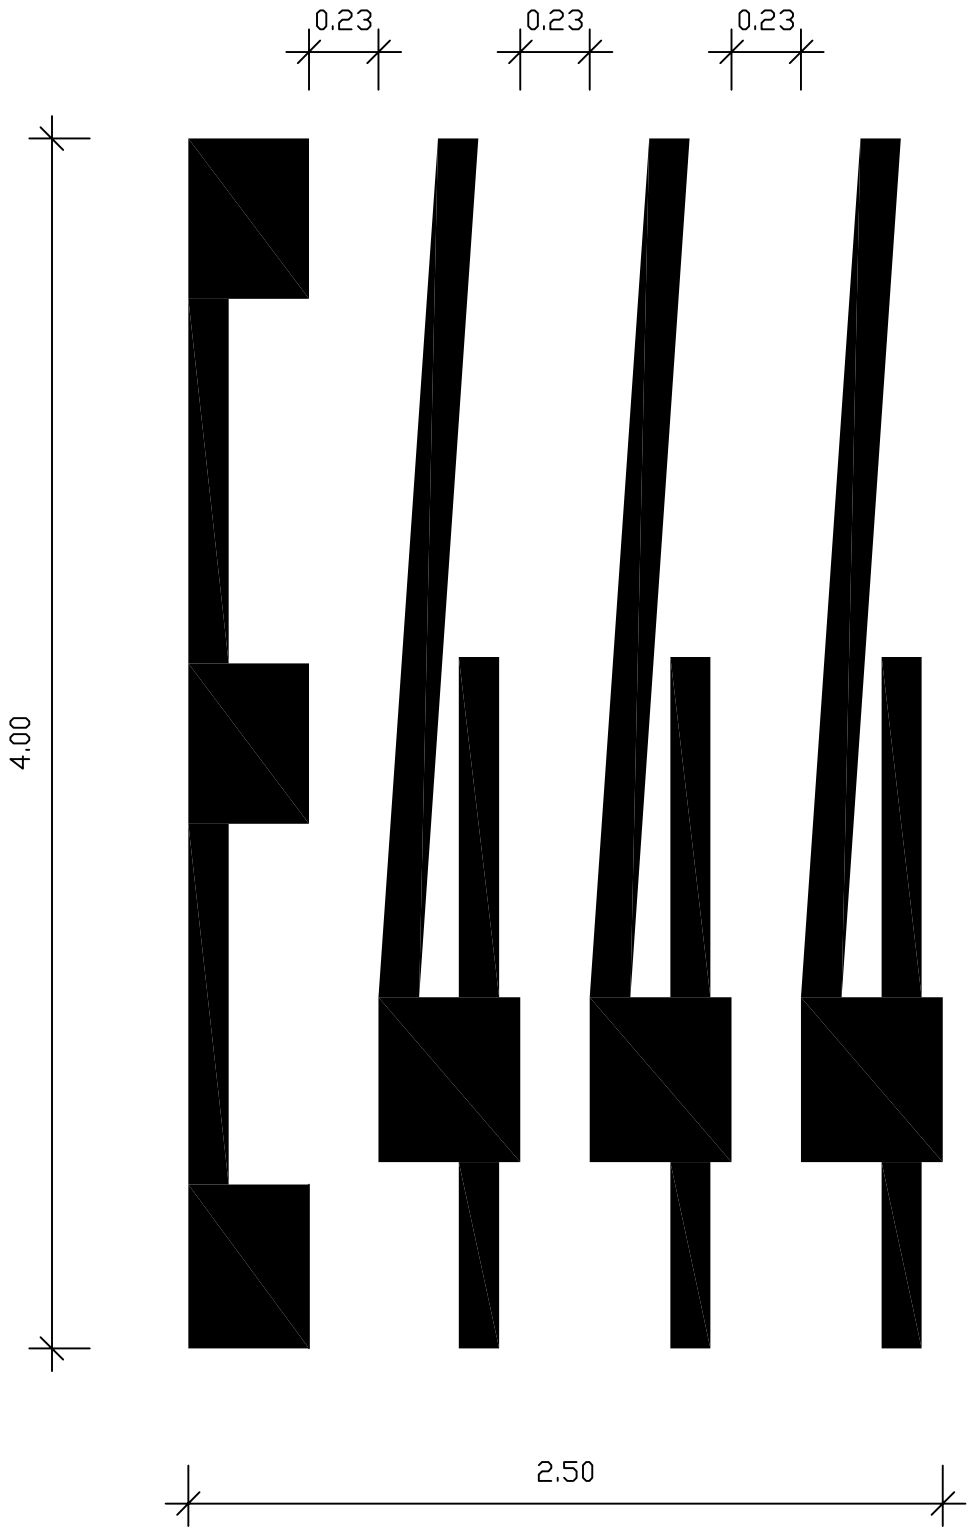



Písmo vychází z VL6.2: V 15-1 - V 15-13. Číselný údaj se umísťuje symetricky.
Komprese v horizontálním směru 30%.

| | | | |
|---|---|---|---|
| **6** **VYBAVENÍ POZEMNÍCH KOMUNIKACÍ**<br>**6.2** **VODOROVNÉ DOPRAVNÍ ZNAČKY**<br>**č. V 15 Nápis na vozovce**<br>**Symbol značky č. IS 17 Číslo silnice pro mezinárodní provoz** | **MINISTERSTVO DOPRAVY**<br>**ODBOR POZEMNÍCH KOMUNIKACÍ**<br>**VZOROVÉ LISTY** | **VL 6**<br>**V 15 - 36**<br>**02.17** |

TRAM
BUS


**V 15**

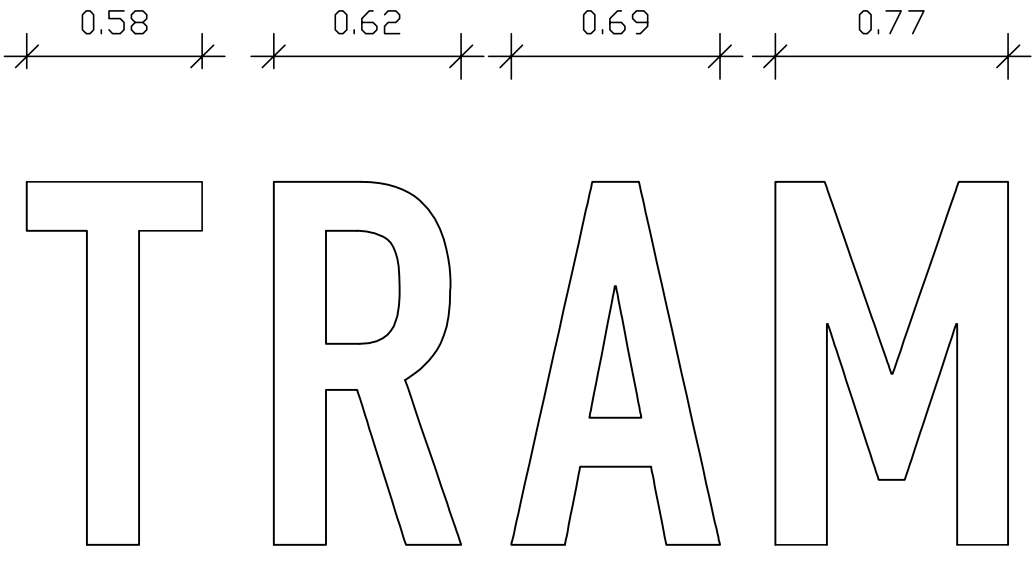




| | | | |
|---|---|---|---|
| **6** **VYBAVENÍ POZEMNÍCH KOMUNIKACÍ**<br>**6.2** **VODOROVNÉ DOPRAVNÍ ZNAČKY**<br>**č. V 15 Nápis na vozovce - BUS, TRAM** | **MINISTERSTVO DOPRAVY**<br>**ODBOR POZEMNÍCH KOMUNIKACÍ**<br>**VZOROVÉ LISTY** | **VL 6**<br>**V 15 - 37**<br>**02.17** |



V 15

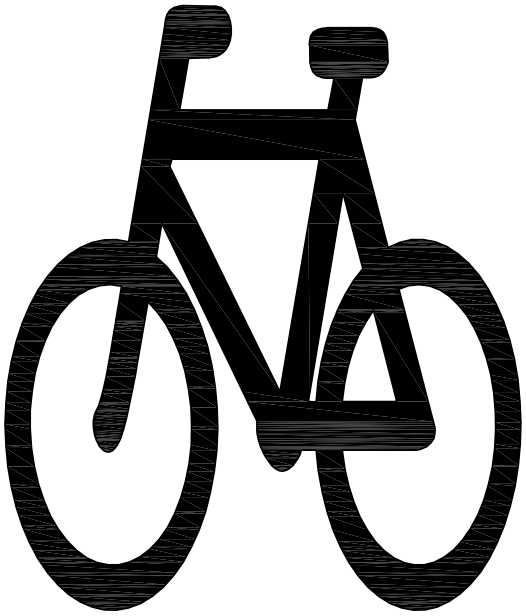

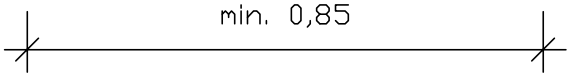


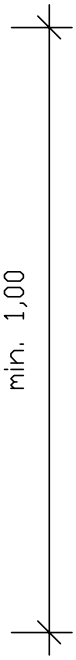

| | | | |
|---|---|---|---|
| 6<br>6.2 | **VYBAVENÍ POZEMNÍCH KOMUNIKACÍ**<br>**VODOROVNÉ DOPRAVNÍ ZNAČKY**<br>**č. V 15 Nápis na vozovce**<br>**Symbol ze značky č. V 14** | **MINISTERSTVO DOPRAVY**<br>**ODBOR POZEMNÍCH KOMUNIKACÍ**<br>**VZOROVÉ LISTY** | **VL 6**<br>**V 15 - 38**<br>**02.17** |




**V 15**

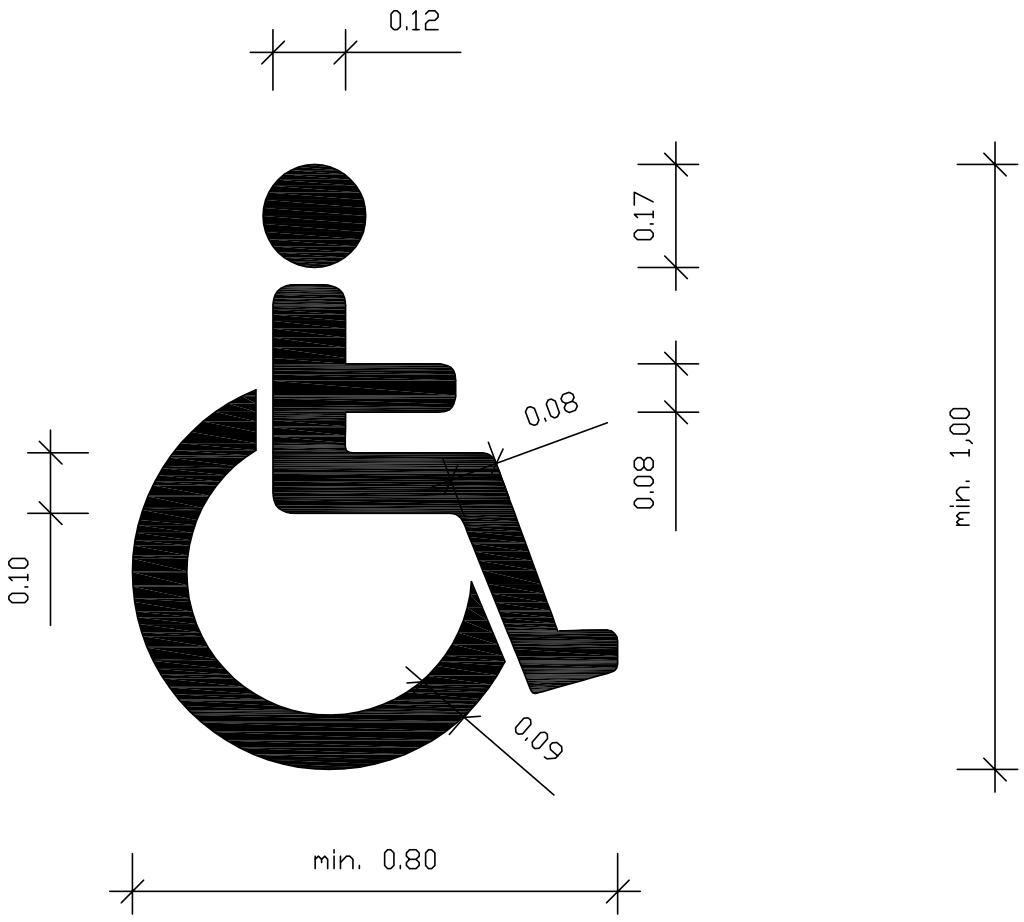



| | | | |
|---|---|---|---|
| **6** **VYBAVENÍ POZEMNÍCH KOMUNIKACÍ**<br>**6.2** **VODOROVNÉ DOPRAVNÍ ZNAČKY**<br>**č. V 15 Nápis na vozovce**<br>**Symbol ze značky č. V 10f** | **MINISTERSTVO DOPRAVY**<br>**ODBOR POZEMNÍCH KOMUNIKACÍ**<br>**VZOROVÉ LISTY** | **VL 6**<br>**V 15 - 39**<br>**02.17** |

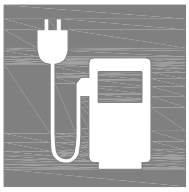


**V 15**

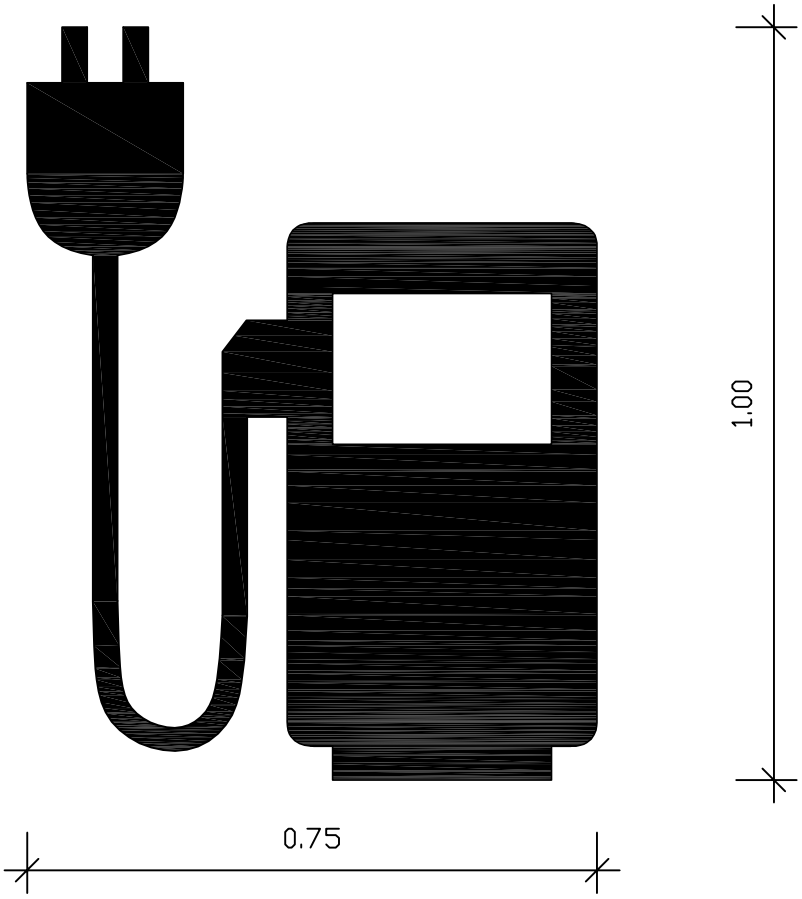


| | | | |
|---|---|---|---|
| **6** **VYBAVENÍ POZEMNÍCH KOMUNIKACÍ**<br>**6.2** **VODOROVNÉ DOPRAVNÍ ZNAČKY**<br>**č. V15 Nápis na vozovce**<br>**Symbol dobíjecí stanice elektromobilů** | **MINISTERSTVO DOPRAVY**<br>**ODBOR POZEMNÍCH KOMUNIKACÍ**<br>**VZOROVÉ LISTY** | **VL 6**<br>**V 15 - 40**<br>**02.17** |

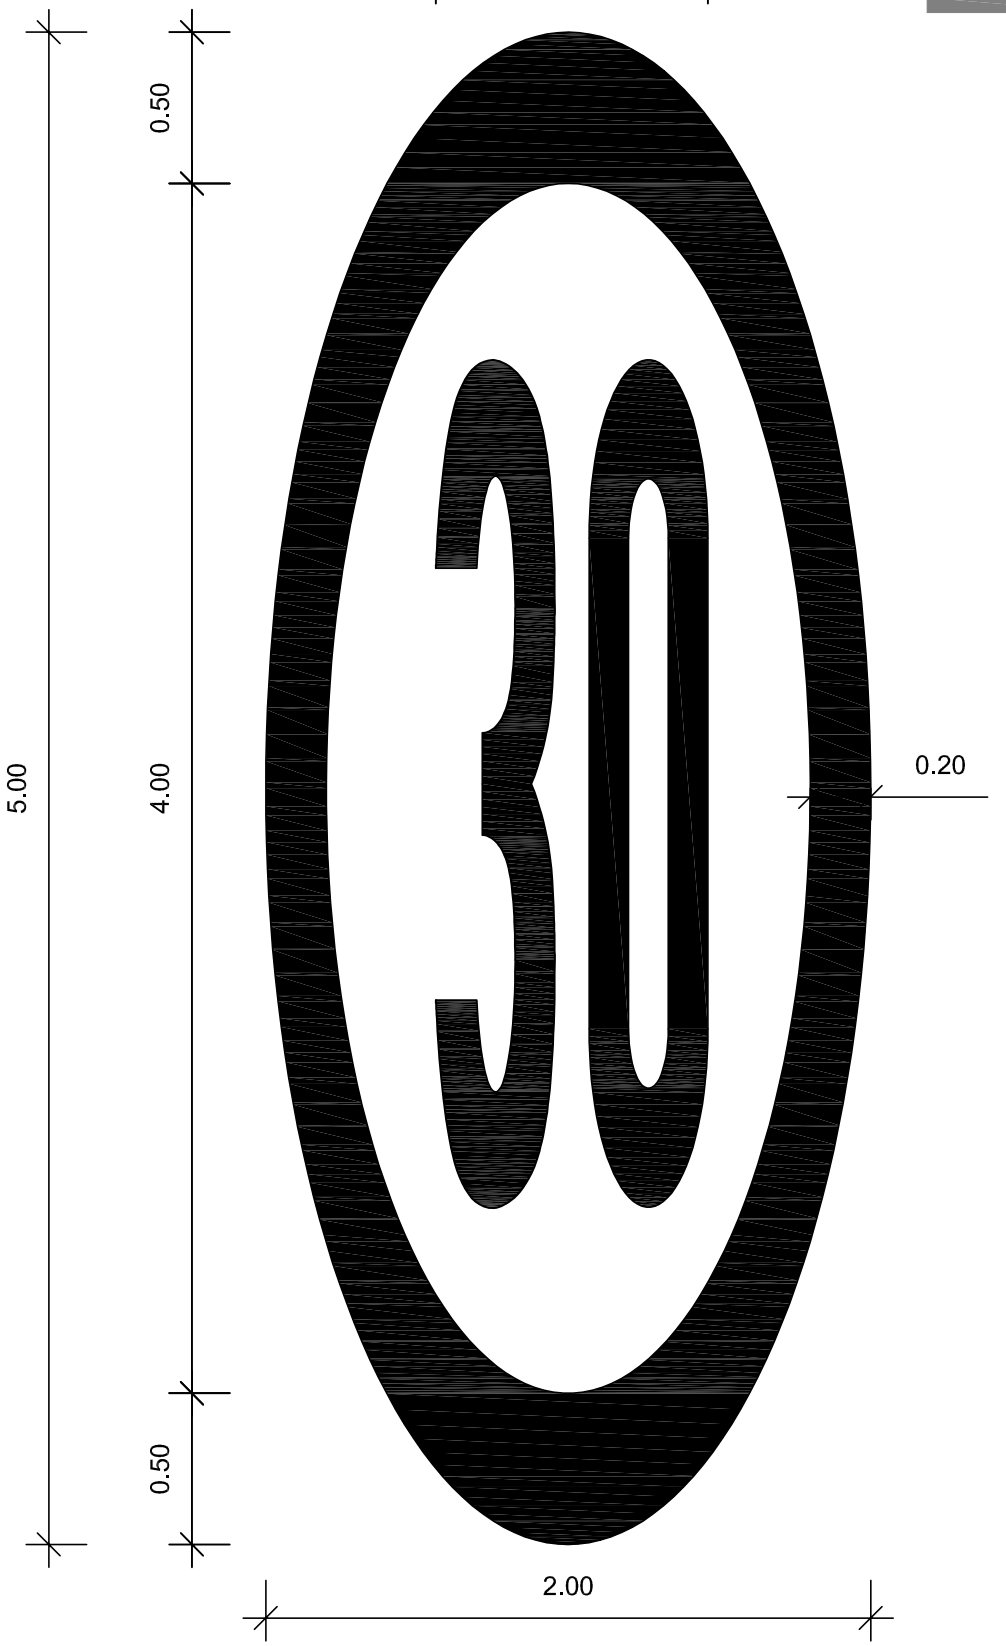

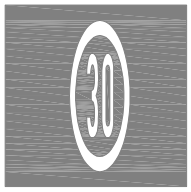




**V 15**

Písmo vychází z VL6.2: V 15-10 - V 15-13. Písmo je zmenšeno o 30%.


| | | | |
|---|---|---|---|
| **6** **VYBAVENÍ POZEMNÍCH KOMUNIKACÍ**<br>**6.2** **VODOROVNÉ DOPRAVNÍ ZNAČKY**<br>**č. V 15 Nápis na vozovce**<br>Symbol značky č. B 20a Nejvyšší dovolená rychlost | MINISTERSTVO DOPRAVY<br>ODBOR POZEMNÍCH KOMUNIKACÍ<br>**VZOROVÉ LISTY** | **VL 6**<br>**V 15 - 41**<br>**02.17** |

V 16

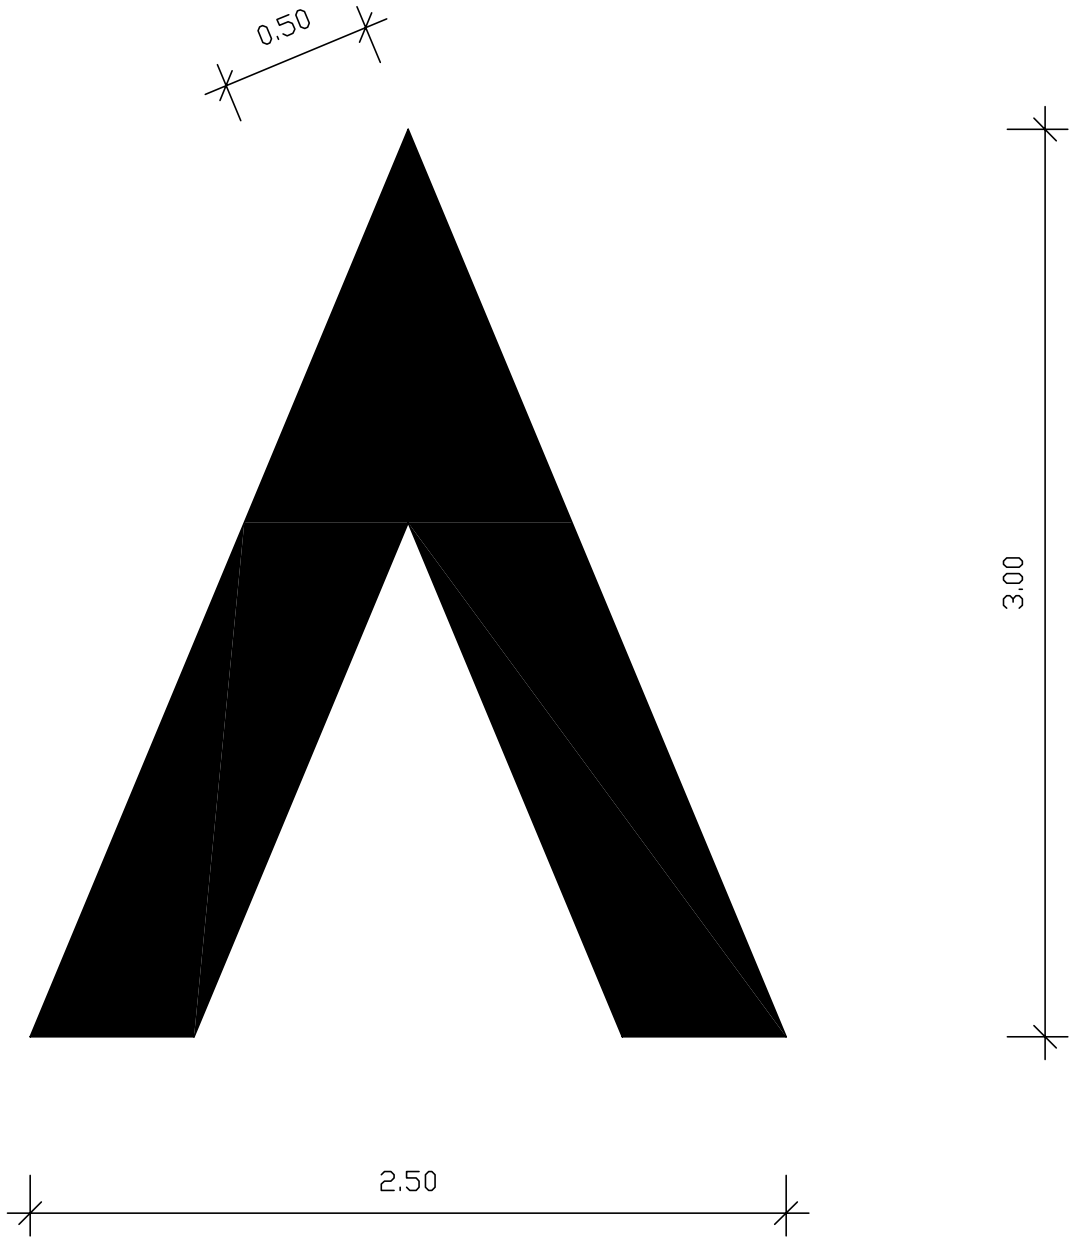



| | | | |
|---|---|---|---|
| 6<br>6.2 | VYBAVENÍ POZEMNÍCH KOMUNIKACÍ<br>VODOROVNÉ DOPRAVNÍ ZNAČKY<br>č. V 16 Bezpečný odstup | MINISTERSTVO DOPRAVY<br>ODBOR POZEMNÍCH KOMUNIKACÍ<br>VZOROVÉ LISTY | VL 6<br>V 16<br>02.17 |

V 17

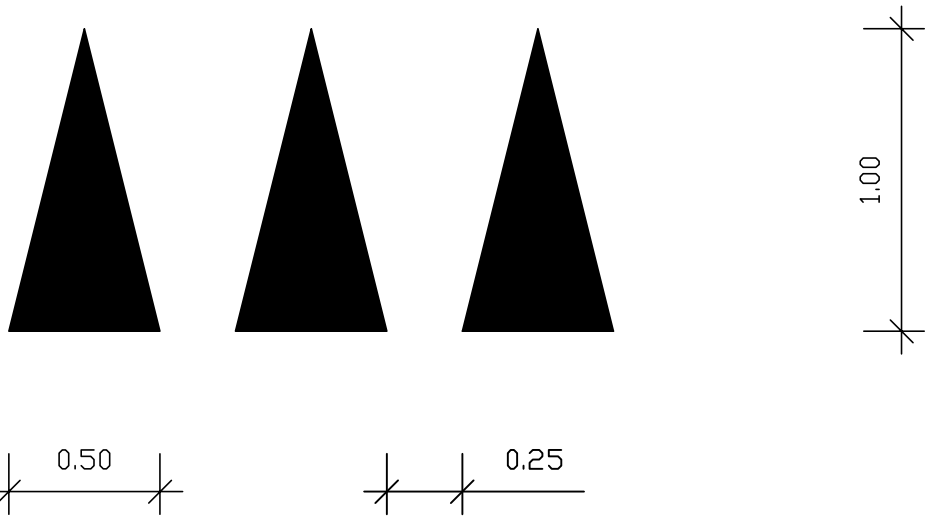



| | | | |
|---|---|---|---|
| 6<br>6.2 | VYBAVENÍ POZEMNÍCH KOMUNIKACÍ<br>VODOROVNÉ DOPRAVNÍ ZNAČKY<br>č. V 17 Trojúhelníky | MINISTERSTVO DOPRAVY<br>ODBOR POZEMNÍCH KOMUNIKACÍ<br>VZOROVÉ LISTY | VL 6<br>V 17<br>02.17 |

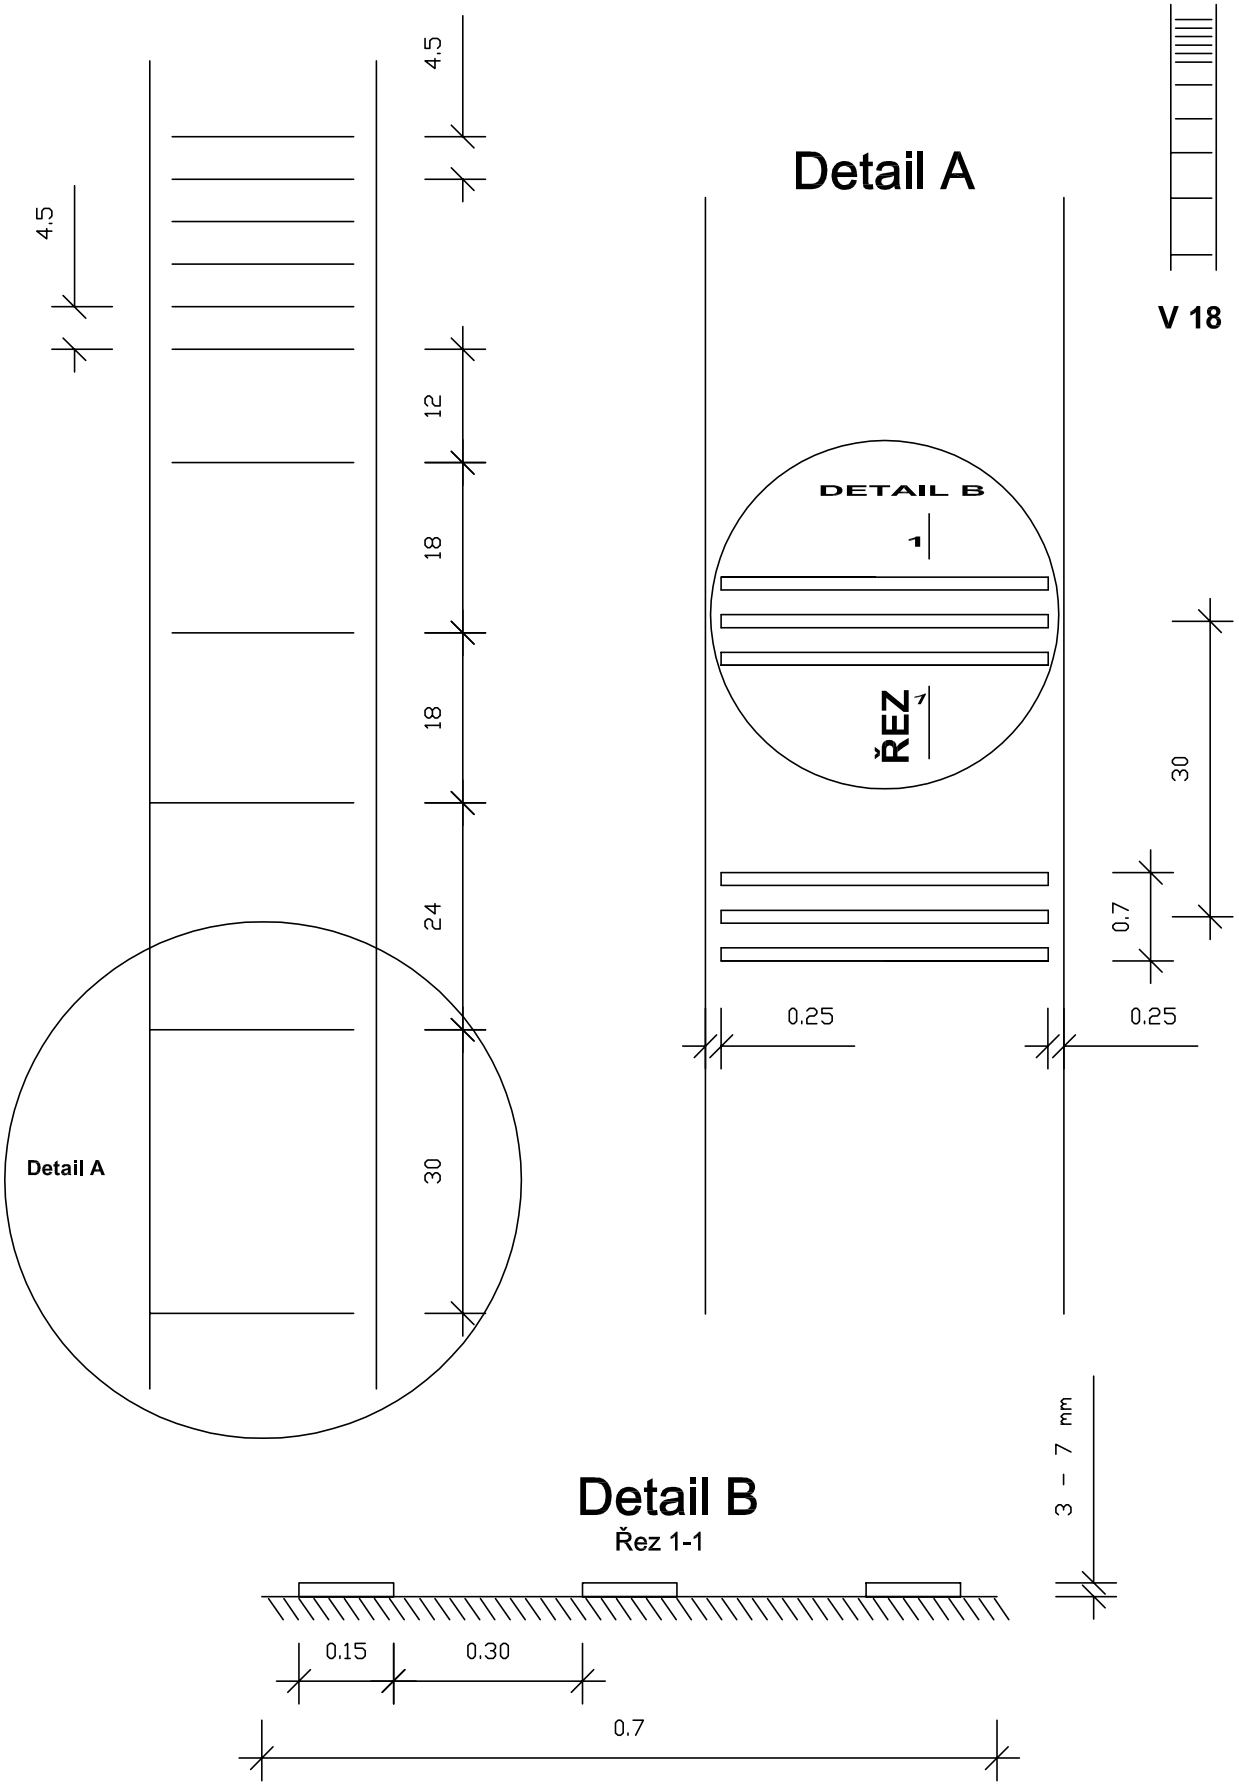


Pozn.: Kóty jsou uváděny v metrech.


| | | |
|---|---|---|
| **6 VYBAVENÍ POZEMNÍCH KOMUNIKACÍ**<br>**6.2 VODOROVNÉ DOPRAVNÍ ZNAČKY**<br>**č. V 18 Optická psychologická brzda** | **MINISTERSTVO DOPRAVY**<br>**ODBOR POZEMNÍCH KOMUNIKACÍ**<br>**VZOROVÉ LISTY** | **VL 6**<br>**V 18 - 1**<br>**02.17** |

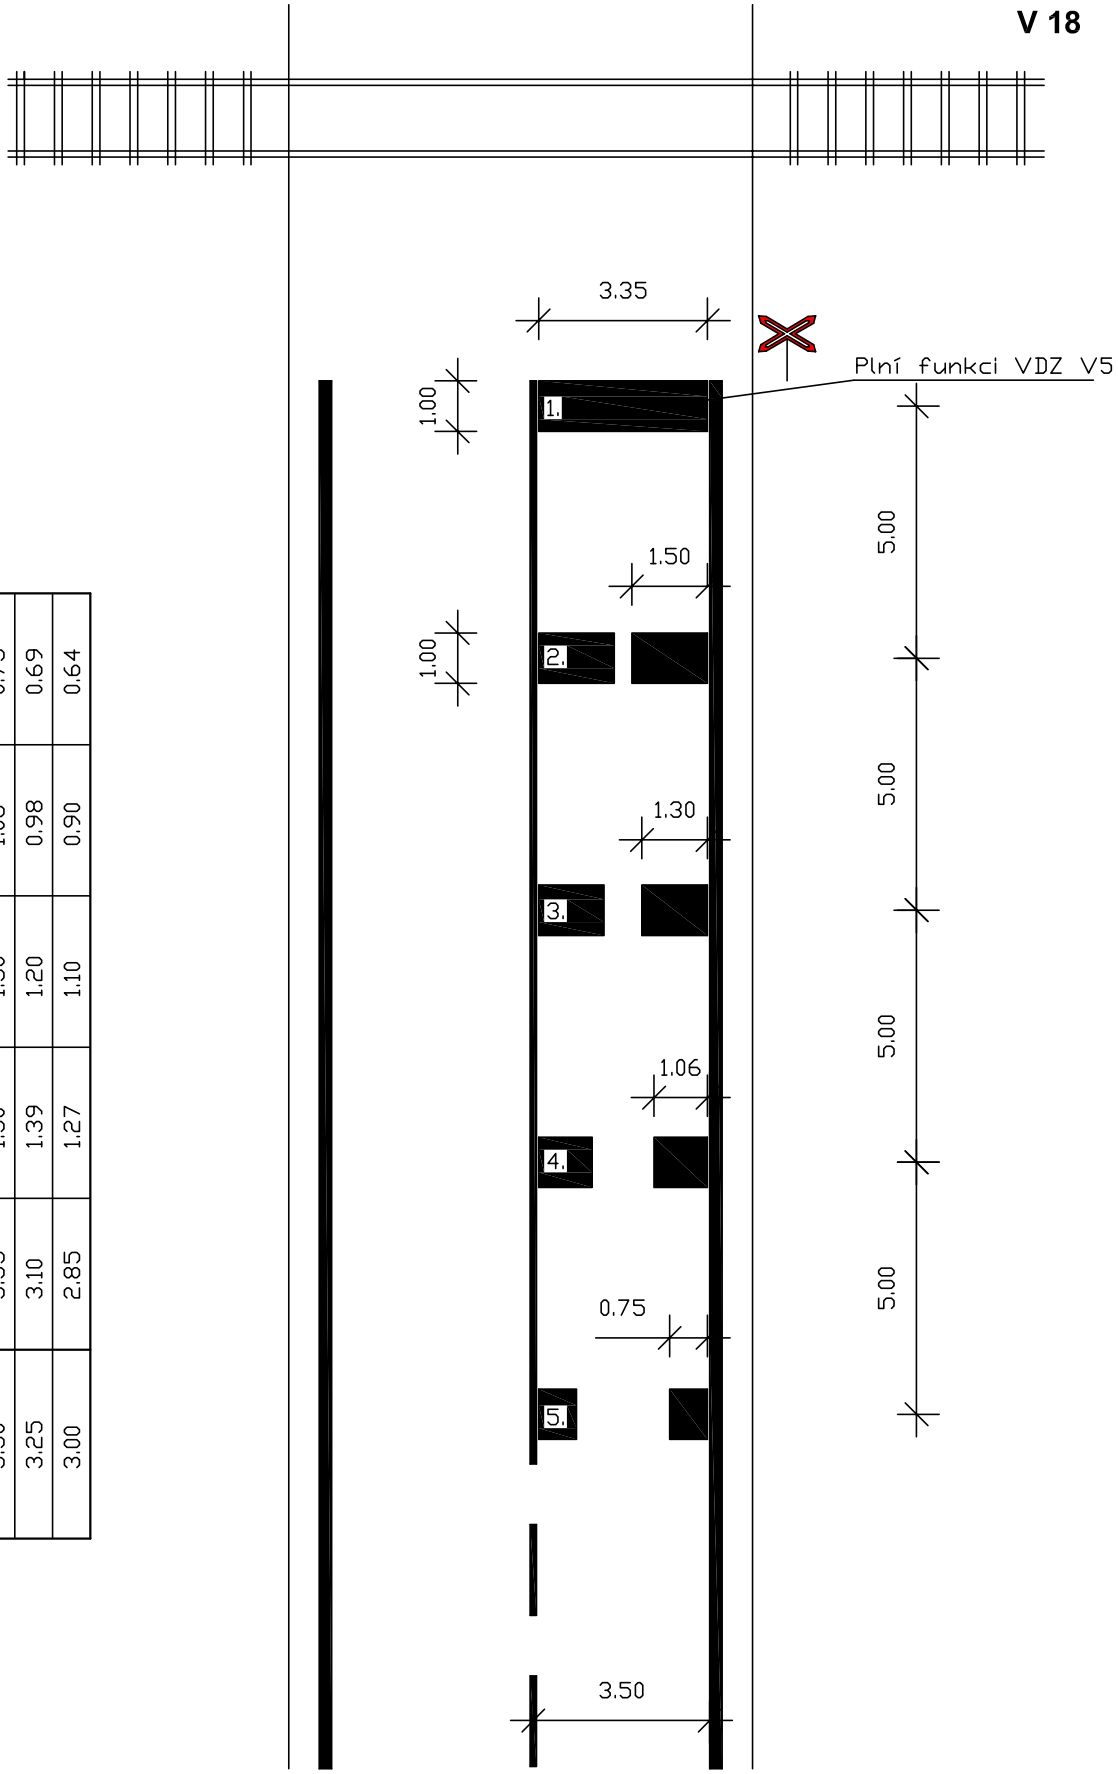



**Délky čar VDZ č. V 18 pro konkrétní šířku jízdního pruhu**

| šířka pruhu | 1. čára | 2. čára | 3. čára | 4. čára | 5. čára |
|---|---|---|---|---|---|
| 3.50 | 3.35 | 1.50 | 1.30 | 1.06 | 0.75 |
| 3.25 | 3.10 | 1.39 | 1.20 | 0.98 | 0.69 |
| 3.00 | 2.85 | 1.27 | 1.10 | 0.90 | 0.64 |

Pozn.: Příčné čáry trychtýřové brzdy jsou o 15 cm užší než je šířka jízdního pruhu a umisťuje se souměrně do prostoru mezi VDZ V 1 a V 4. Z délky 1. příčné čáry se odvozují délky ostatních příčných čar.

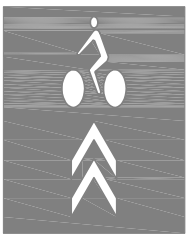

V 20

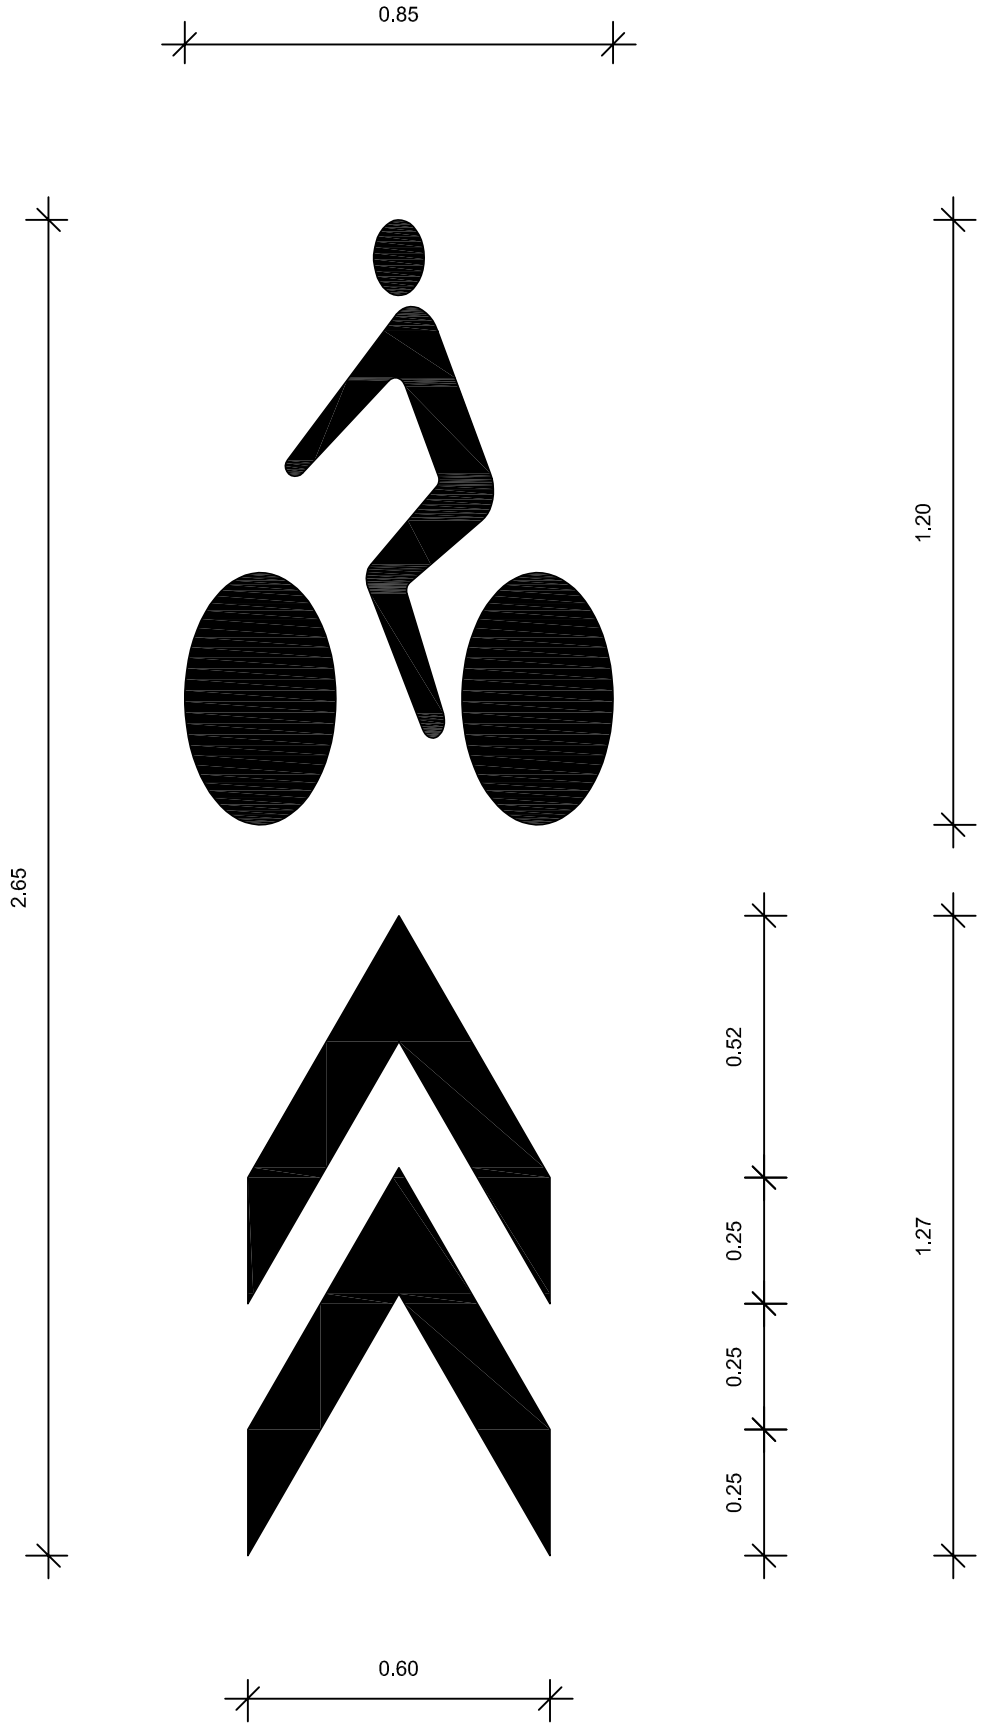


| | | | |
|---|---|---|---|
| **6** **VYBAVENÍ POZEMNÍCH KOMUNIKACÍ**<br>**6.2** **VODOROVNÉ DOPRAVNÍ ZNAČKY**<br>**č. V 20 Piktogramový koridor pro cyklisty** | **MINISTERSTVO DOPRAVY**<br>**ODBOR POZEMNÍCH KOMUNIKACÍ**<br>**VZOROVÉ LISTY** | **VL 6**<br>**V 20**<br>**02.17** |

**VZOROVÉ LISTY STAVEB POZEMNÍCH KOMUNIKACÍ – VL 6.2 – VODOROVNÉ DOPRAVNÍ ZNAČKY**


| | |
|---|---|
| **Vydalo:** | Ministerstvo dopravy |
| **Zpracovatel.:** | Ing. Pavel Tučka (Centrum dopravního výzkumu, v.v.i.) |
| **Tech. redakční rada:** | JUDr. Ladislav Decarli (Ministerstvo dopravy) |
| | Ing. Alena Stupková (Ministerstvo dopravy) |
| | Ing. Mikuláš Bureš (Ministerstvo vnitra ČR) |
| | Ing. Michal Caudr (ŘSD ČR) |
| | Michal Prášil (ŘSD ČR) |
| | Pplk. JUDr. Sabina Burdová (Policie ČR) |
| | Ing. Jan Cvetler (ČMADZ) |
| | Ing. Karel Hofman (ČMADZ) |
| | Ing. Pavel Znamenáček (Pragoprojekt) |
| | Ing. Michal Tóth |
| | Ing. Irena Šašinková (Silniční vývoj - ZDZ) |
| | Ing. Antonín Seidl (D.I.A.S.) |
| **Zástupce koordinátora:** | Ing. Pavel Skládaný (Centrum dopravního výzkumu, v.v.i.) |