
MINISTERSTVO DOPRAVY

VZOROVÉ LISTY

STAVEB POZEMNÍCH KOMUNIKACÍ

VL 6.3 – DOPRAVNÍ ZAŘÍZENÍ

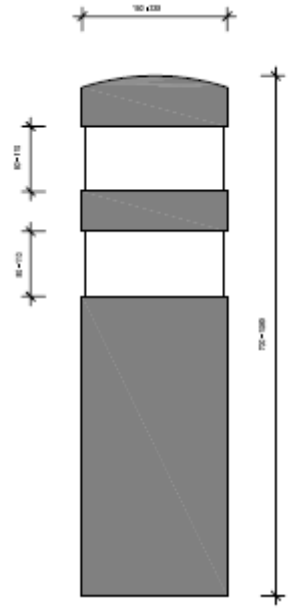

únor 2017





Schváleno Ministerstvem dopravy č. j. 44/2017-120-TN/1 ze dne 9. února 2017
s **účinností od 15. února 2017**.

Tento dokument se shoduje se schválenou verzí.

Současně se ruší a nahrazují v celém rozsahu vzorové listy VL 6.3 – Dopravní zařízení schválené Ministerstvem dopravy pod č. j. 354/2004-O120-STSP/2 s účinností od 1. července 2004.

Distribuce pouze v elektronické podobě na webu pjpk.cz.

VZOROVÉ LISTY STAVEB POZEMNÍCH KOMUNIKACÍ

CELKOVÝ PŘEHLED

VL 1 VOZOVKY A KRAJNICE

VL 2.1 SILNIČNÍ TĚLESO

VL 2.2 ODVODNĚNÍ

VL 3 KŘIŽOVATKY

VL 4 MOSTY

VL 5 TUNELY

VL 6.1 SVISLÉ DOPRAVNÍ ZNAČKY

VL 6.2 VODOROVNÉ DOPRAVNÍ ZNAČKY

VL 6.3 DOPRAVNÍ ZAŘÍZENÍ

TECHNICKÁ ZPRÁVA

SEZNAM VZOROVÝCH LISTŮ

DOPRAVNÍ ZAŘÍZENÍ

VL 6.4 PROMĚNNÉ DOPRAVNÍ ZNAČENÍ

VL 7 VYBRANÉ PRVKY MÍSTNÍCH KOMUNIKACÍ PRO ZKLIDŇOVÁNÍ DOPRAVY

VL 0 VZOROVÉ LISTY OPRAV MOSTNÍCH OBJEKTŮ

Technická zpráva

Obsah technické zprávy

1. ÚVOD 4

2. OZNAČENÍ VZOROVÝCH LISTŮ 4

3. TEXTOVÁ ČÁST 5

3.1. VŠEOBECNĚ 5

3.2. NÁZVOSLOVÍ 5

3.3. POŽADAVKY NA VÝROBKY 5

3.4. GEOMETRICKÁ PŘESNOST 5

4. GRAFICKÁ ČÁST 6

1. ÚVOD

Vzorové listy upravují provedení vybraných dopravních zařízení. Rozpracovávají ustanovení příslušných předpisů včetně mezinárodních do potřebných detailů, a tím vytvářejí předpoklady pro jednotné provedení dopravních zařízení, včetně jejich vybraných variant. Využití vzorových listů především ve výrobě dopravních zařízení sleduje zájem zvýšení kvality dopravního značení.

Vzorové listy věcně navazují na:

(1) zákon č. 361/2000 Sb., o provozu na pozemních komunikacích a o změnách některých zákonů (zákon o silničním provozu), ve znění pozdějších předpisů,

(2) vyhlášku č. 294/2015 Sb., kterou se provádějí pravidla provozu na pozemních komunikacích, ve znění pozdějších předpisů.

Význam jednotlivých dopravních zařízení a podmínky pro jejich užití a umístění upravují:

(1) vyhláška č. 294/2015 Sb., kterou se provádějí pravidla provozu na pozemních komunikacích, ve znění pozdějších předpisů,

(2) TP 65 Zásady pro dopravní značení na pozemních komunikacích,

(3) TP 66 Zásady pro označování pracovních míst na pozemních komunikacích,

2. OZNAČENÍ VZOROVÝCH LISTŮ

Dosud užívaný systém značení VL byl pro lepší přehlednost změněn. Označení skupin a podskupin bylo nahrazeno číslem vodorovné dopravní značky.

Členění vzorových listů:

Pro označení vzorových listů byla určena zkratka VL a dále třídění, které má následují formu a obsah:

VL X

X XXX – XX

XX.XX

X	označuje VL podle základního obsahu
X XXX – XX	označuje číslo vodorovné dopravní značky a pořadí vzorového listu této značky
XX.XX	první dvě číslice označují měsíc, další dvě číslice označují rok

Kompletní jednoznačné označení zní například: VL 6.3 Z 1 – 1 02.17

VL 6.3 Z 1 – 2 02.17

VL jsou zpracovány ve formě otevřeného souboru, který je možno průběžně upravovat nebo doplňovat.

Obsahem textové části jsou základní zásady provedení vybraných dopravních zařízení. Obsahem obrazové části jsou výkresy jednotlivých dopravních zařízení, včetně vybraných variant. Rozdělení dopravních zařízení vychází z vyhlášky č. 294/2015 Sb.

Všechny rozměry jsou uvedeny v mm.

3. TEXTOVÁ ČÁST

3.1. VŠEOBECNĚ

Provedení a tvary symbolů dopravních zařízení provedených podle prováděcího právního předpisu se nesmějí měnit; to neplatí pro dopravní zařízení se symboly, které mohou být obráceny, a se symboly, které jsou uvedeny jen jako vzory.

3.2. NÁZVOSLOVÍ

VL 6.3 upravují požadavky na činnou plochu dopravních zařízení. Činnou plochou se rozumí plocha, kterou řidič vidí.

3.3. POŽADAVKY NA VÝROBKY

Požadavky na výrobky jsou uvedeny v konkrétních technických předpisech, např. ČSN, ČSN EN, TP, TKP.


3.4. GEOMETRICKÁ PŘESNOST

Všechny rozměry dopravních zařízení musejí odpovídat stanoveným hodnotám s plusovou i minusovou tolerancí, která se odvozuje z výchozího rozměru. Povolené tolerance uvádí následující tabulka, nejmenší tolerance je 2 mm.


Rozměr	Tolerance
< 50	$\pm$ 10 %
50–400	$\pm$ 5 %
> 400	$\pm$ 1 %
Poloměr zaoblení rohu	$\pm$ 10 %

4. GRAFICKÁ ČÁST

DOPRAVNÍ ZAŘÍZENÍ		Datum
6.3 Z 1 – 1	Dopravní kužel	02.2017
6.3 Z 1 – 2	Dopravní kužel	02.2017
6.3 Z 2	Zábrana pro označení uzavírky	02.2017
6.3 Z 3 – 1	Vodicí tabule	02.2017
6.3 Z 3 – 2	Vodicí tabule	02.2017
6.3 Z 3 – 3	Vodicí tabule	02.2017
6.3 Z 3 – 4	Vodicí tabule	02.2017
6.3 Z 3 – 5	Vodicí tabule	02.2017
6.3 Z 4a,b	Směrovací deska se šikmými pruhy	02.2017
6.3 Z 4c – 1	Směrovací deska středová	02.2017
6.3 Z 4c – 2	Směrovací deska středová	02.2017
6.3 Z 4c – 3	Směrovací deska středová	02.2017
6.3 Z 4d	Směrovací deska se šipkou doleva	02.2017
6.3 Z 4e	Směrovací deska se šipkou doprava	02.2017
6.3 Z 5a,b - 1	Vodicí deska se šikmými pruhy	02.2017
6.3 Z 5a,b - 2	Vodicí deska se šikmými pruhy	02.2017
6.3 Z 5a,b - 3	Vodicí deska se šikmými pruhy	02.2017
6.3 Z 5a,b - 4	Vodicí deska se šikmými pruhy	02.2017
6.3 Z 5c - 1	Vodicí deska středová se šikmými pruhy	02.2017
6.3 Z 5c - 2	Vodicí deska středová se šikmými pruhy	02.2017
6.3 Z 5c - 3	Vodicí deska středová se šikmými pruhy	02.2017
6.3 Z 6a	Velká zvýrazňující deska	02.2017
6.3 Z 7 – 1	Pojízdná uzavírková tabule – Typ II	02.2017
6.3 Z 7 – 2	Pojízdná uzavírková tabule	02.2017
6.3 Z 8b	Zastavovací terč pro jiné osoby	02.2017
6.3 Z 11a,b	Směrový sloupek bílý	02.2017
6.3 Z 11c,d	Směrový sloupek červený	02.2017
6.3 Z 11e,f	Směrový sloupek modrý	02.2017
6.3 Z 11g	Směrový sloupek červený kulatý	02.2017
6.3 Z 11h	Směrový sloupek zelený kulatý - baliseta	02.2017

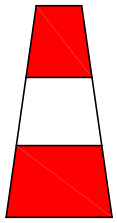


Z1

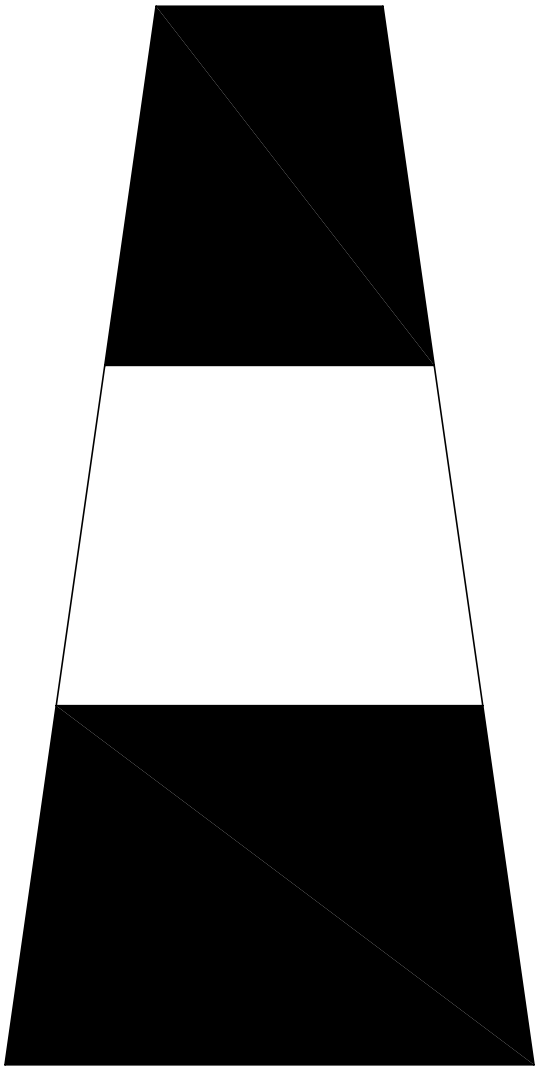


Pozn.: Dopravní kužel do výšky 45 cm je rozdělen třemi střídavě červenými a bílými pruhy tak, aby horní a spodní části byly červené. Výšky pruhů jsou v poměru cca 1:1. Další podrobnosti jsou uvedeny v ČSN EN 13422+A1.

6 6.3	VYBAVENÍ POZEMNÍCH KOMUNIKACÍ DOPRAVNÍ ZAŘÍZENÍ Z 1 Dopravní kužel	MINISTERSTVO DOPRAVY ODBOR POZEMNÍCH KOMUNIKACÍ VZOROVÉ LISTY	VL 6 Z1 - 1 02.17

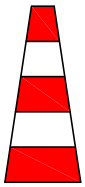



Z1

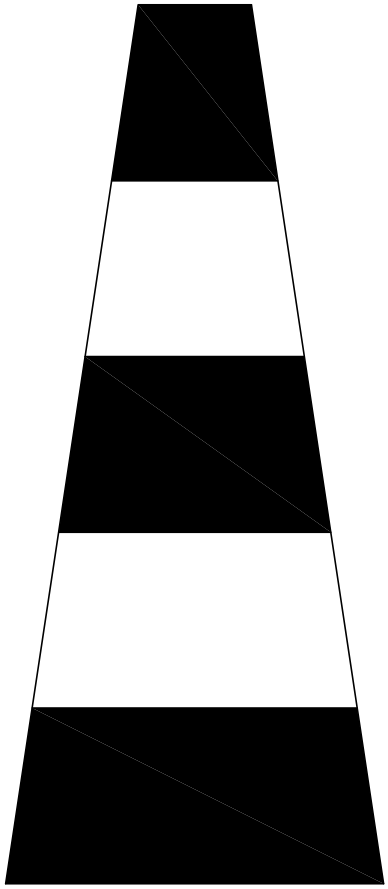

Pozn.: Dopravní kužel výšky větší než 45 cm je rozdělen pěti střídavě červenými a bílými pruhy tak, aby horní a spodní části byly červené. Výška pruhů je v poměru cca 1:1. Další podrobnosti jsou uvedeny v ČSN EN 13422+A1.

6 6.3	VYBAVENÍ POZEMNÍCH KOMUNIKACÍ DOPRAVNÍ ZAŘÍZENÍ Z 1 Dopravní kužel	MINISTERSTVO DOPRAVY ODBOR POZEMNÍCH KOMUNIKACÍ VZOROVÉ LISTY	VL 6 Z1 - 2 02.17

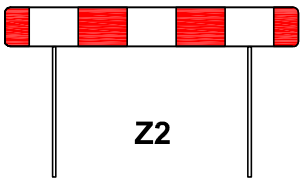

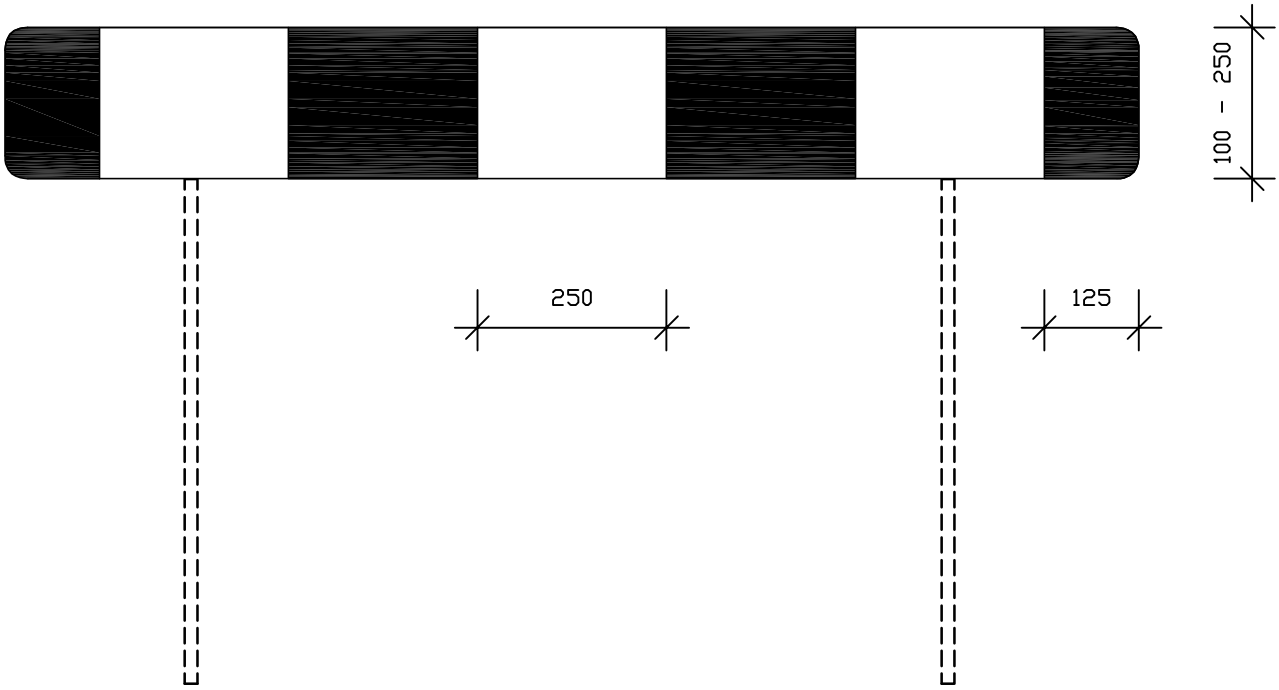


délka zábrany	1000	1500	2000	2500	3000

Pozn. Zaoblení rohů činné plochy se provádí dle podkladu.




Z3

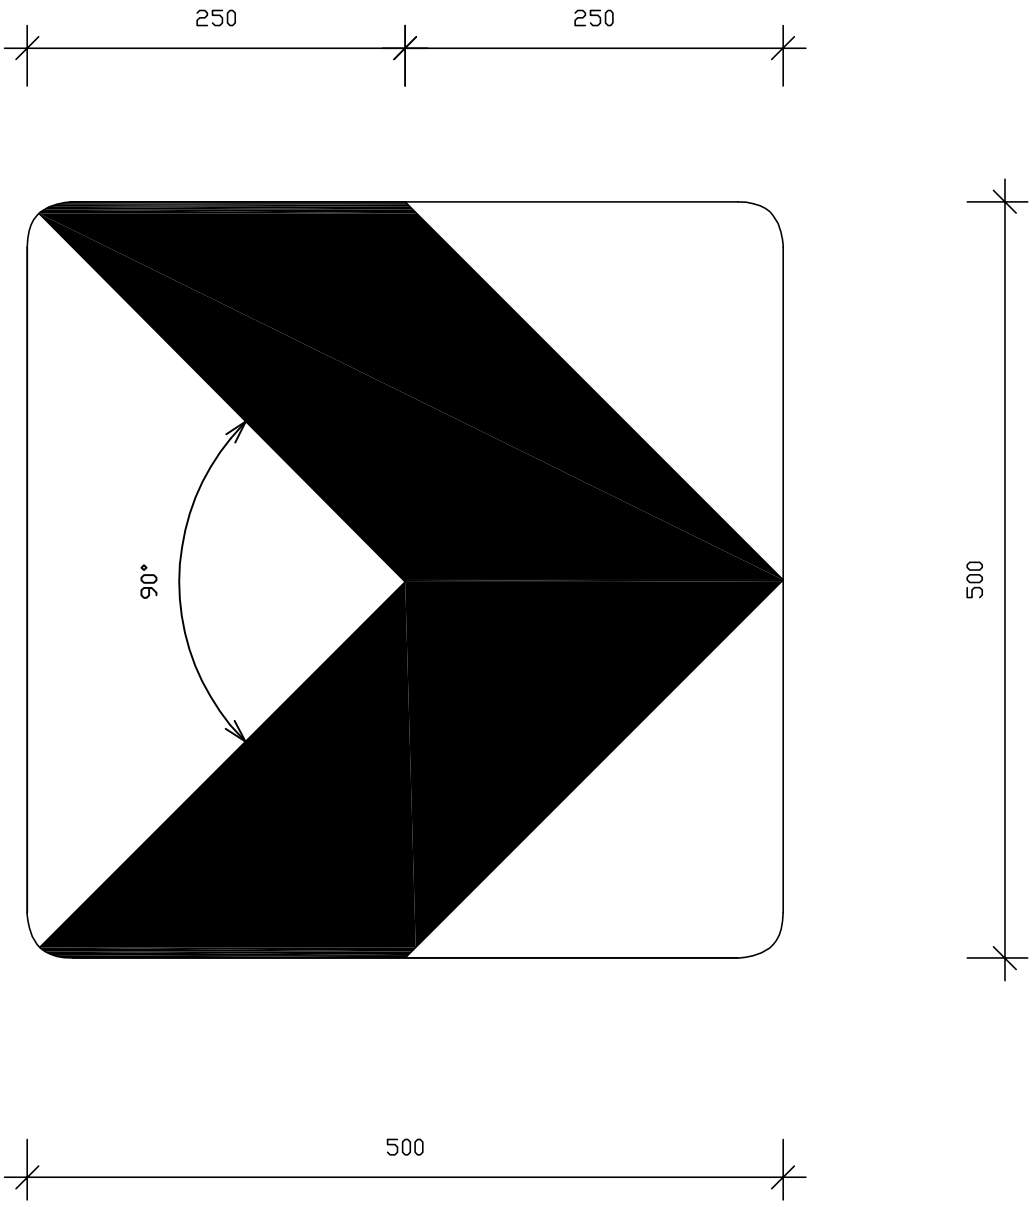


Pozn. Zaoblení rohů dle štítu min. však poloměrem R20.

6 6.3 **VYBAVENÍ POZEMNÍCH KOMUNIKACÍ** **DOPRAVNÍ ZAŘÍZENÍ** **Z 3 Vodicí tabule**	**MINISTERSTVO DOPRAVY** **ODBOR POZEMNÍCH KOMUNIKACÍ** **VZOROVÉ LISTY**	**VL 6** **Z3 - 1** **02.17**

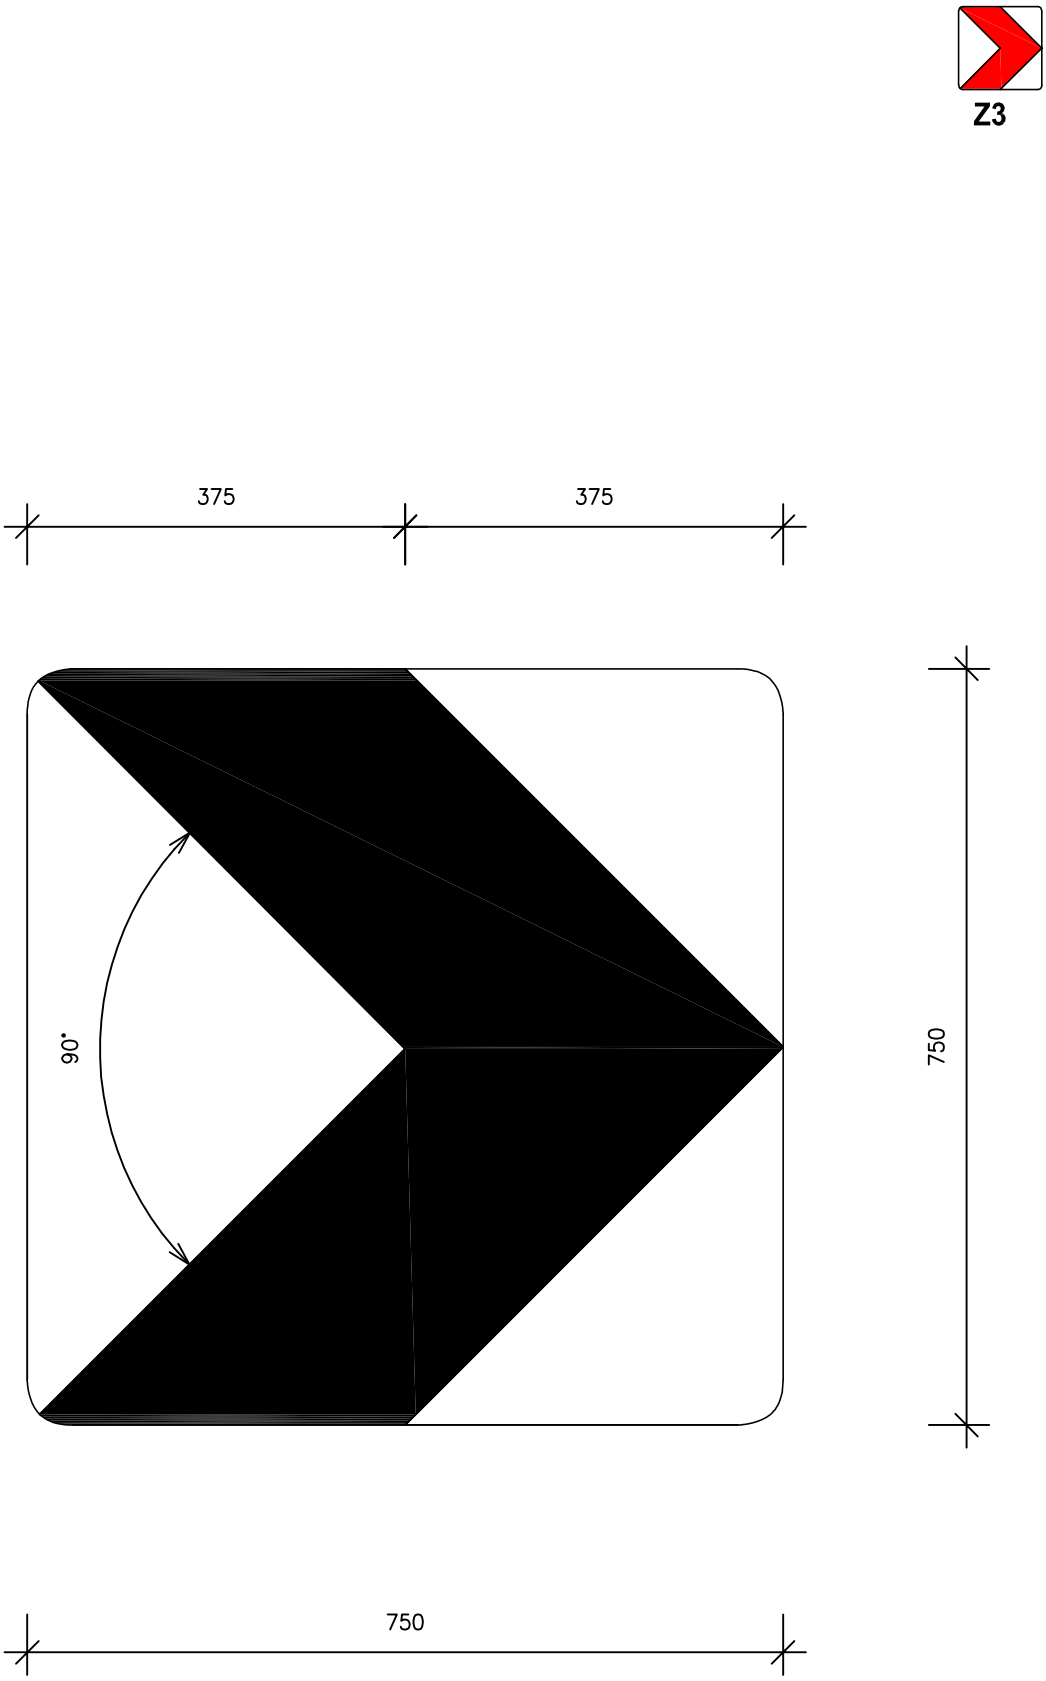


Pozn. Zaoblení rohů dle štítu min. však poloměrem R20.

6 6.3 **VYBAVENÍ POZEMNÍCH KOMUNIKACÍ** **DOPRAVNÍ ZAŘÍZENÍ** **Z 3 Vodicí tabule**	**MINISTERSTVO DOPRAVY** **ODBOR POZEMNÍCH KOMUNIKACÍ** **VZOROVÉ LISTY**	**VL 6** **Z3 - 2** **02.17**

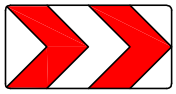


Z3

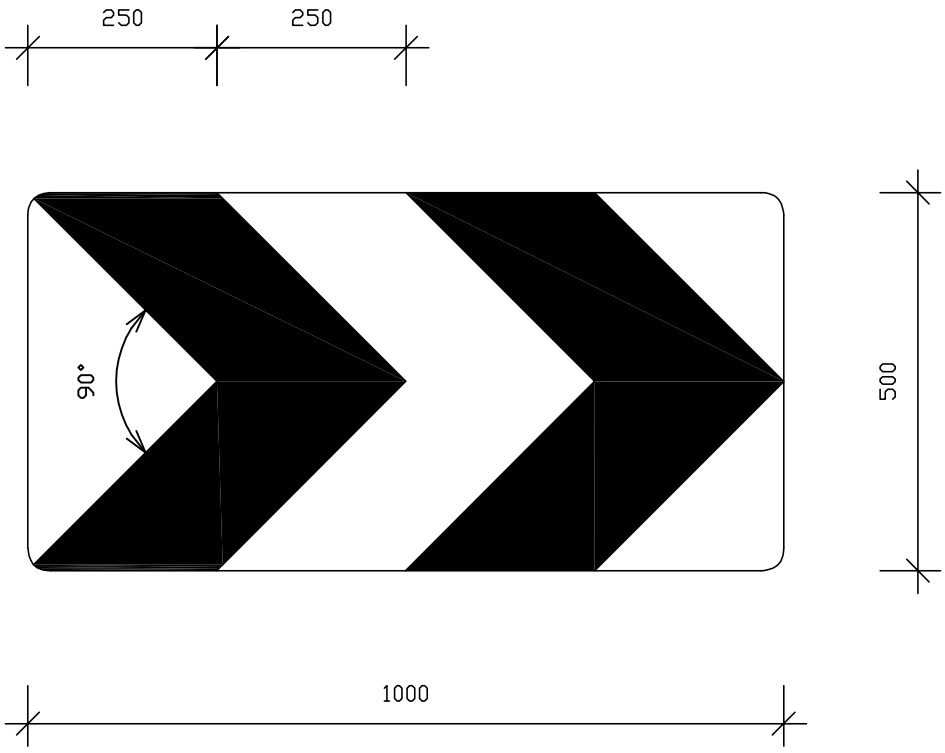


Pozn. Zaoblení rohů dle štítu min. však poloměrem R20.

6 6.3 **VYBAVENÍ POZEMNÍCH KOMUNIKACÍ** **DOPRAVNÍ ZAŘÍZENÍ** **Z 3 Vodicí tabule**	**MINISTERSTVO DOPRAVY** **ODBOR POZEMNÍCH KOMUNIKACÍ** **VZOROVÉ LISTY**	**VL 6** **Z3 - 3** **02.17**

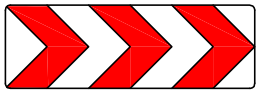

Z3

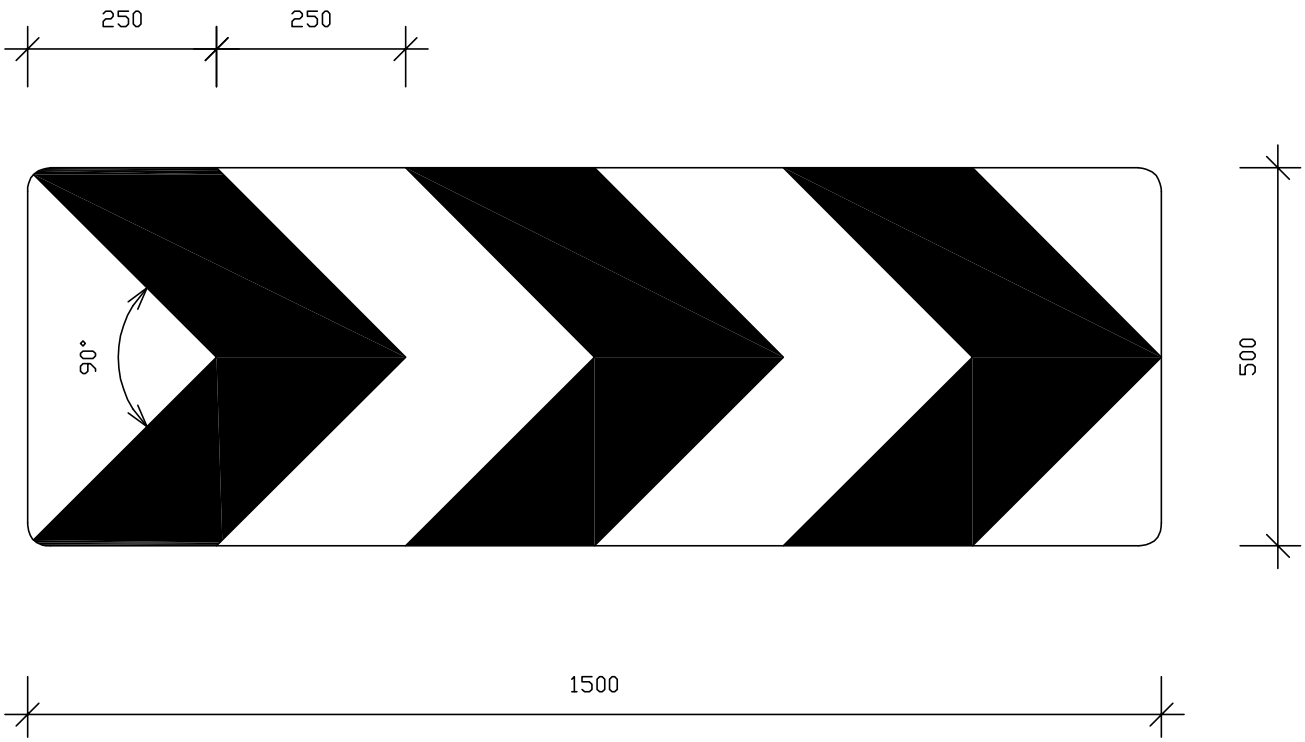


Pozn. Zaoblení rohů dle štítu min. však poloměrem R20.

6 VYBAVENÍ POZEMNÍCH KOMUNIKACÍ 6.3 DOPRAVNÍ ZAŘÍZENÍ Z 3 Vodicí tabule	MINISTERSTVO DOPRAVY ODBOR POZEMNÍCH KOMUNIKACÍ VZOROVÉ LISTY	VL 6 Z3 - 4 02.17





Z3

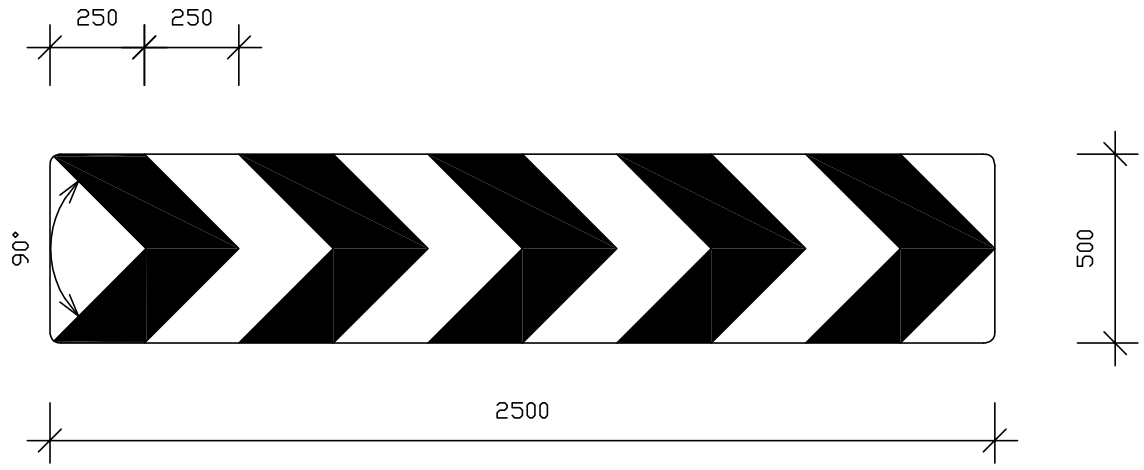

Pozn. Zaoblení rohů dle štítu min. však poloměrem R20.

6 6.3 **VYBAVENÍ POZEMNÍCH KOMUNIKACÍ** **DOPRAVNÍ ZAŘÍZENÍ** **Z 3 Vodicí tabule**	**MINISTERSTVO DOPRAVY** **ODBOR POZEMNÍCH KOMUNIKACÍ** **VZOROVÉ LISTY**	**VL 6** **Z 3 - 5** **02.17**

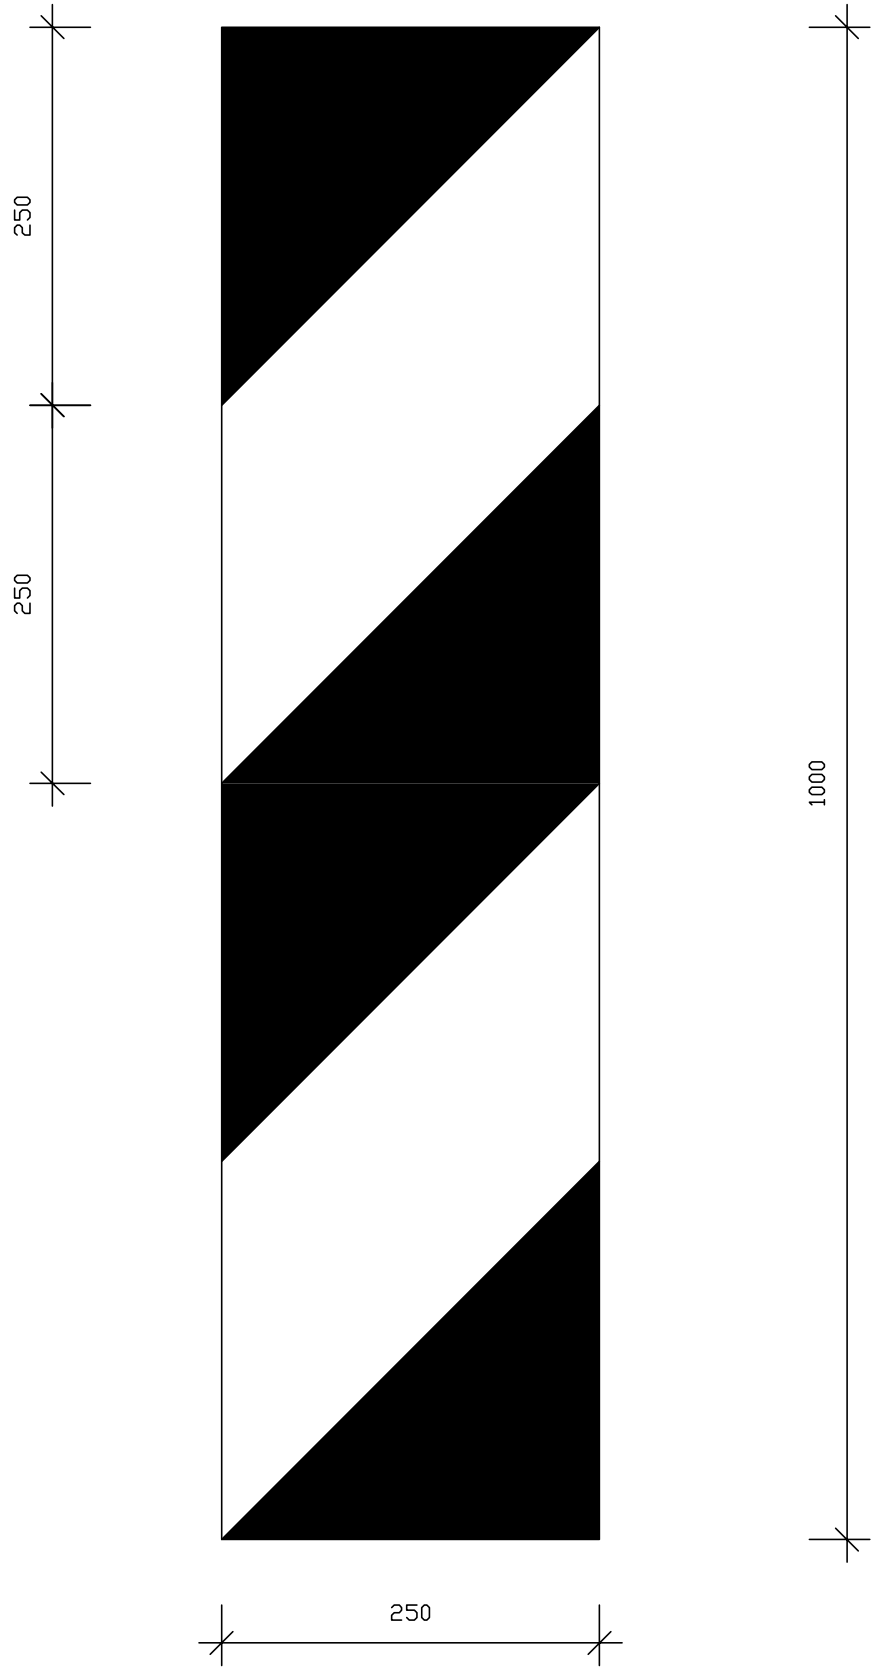


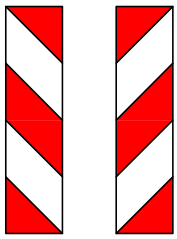


Z 4b Z 4a

Pozn. Při užití jako stále dopravní zařízení se zaoblení rohů provádí dle podkladu. V případě plastového podkladu se zaoblení rohů činné plochy neprovádí.

6 VYBAVENÍ POZEMNÍCH KOMUNIKACÍ 6.3 DOPRAVNÍ ZAŘÍZENÍ Z 4a,b Směrovací deska se šikmými pruhy	MINISTERSTVO DOPRAVY ODBOR POZEMNÍCH KOMUNIKACÍ VZOROVÉ LISTY	VL 6 Z 4a,b 02.17

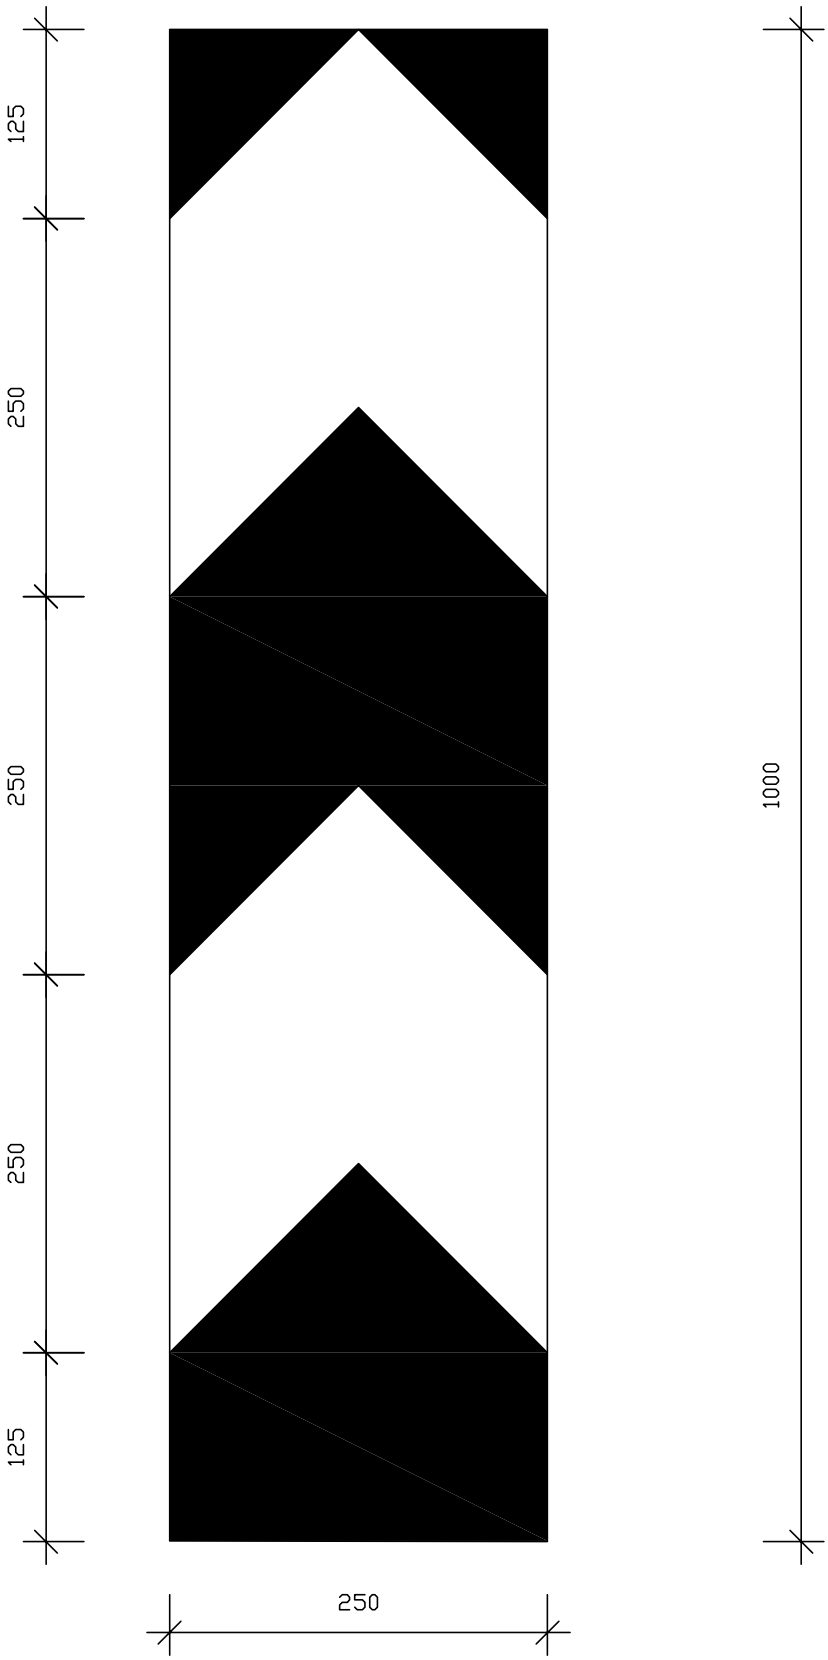

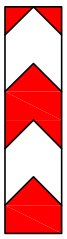


Z 4c

Pozn. Při užití jako stále dopravní zařízení se zaoblení rohů provádí dle podkladu. V případě plastového podkladu se zaoblení rohů činné plochy neprovádí.

6 VYBAVENÍ POZEMNÍCH KOMUNIKACÍ **6.3 DOPRAVNÍ ZAŘÍZENÍ** **Z 4c Směrovací deska středová**	**MINISTERSTVO DOPRAVY** **ODBOR POZEMNÍCH KOMUNIKACÍ** **VZOROVÉ LISTY**	**VL 6** **Z 4c - 1** **02.17**




Z 4c

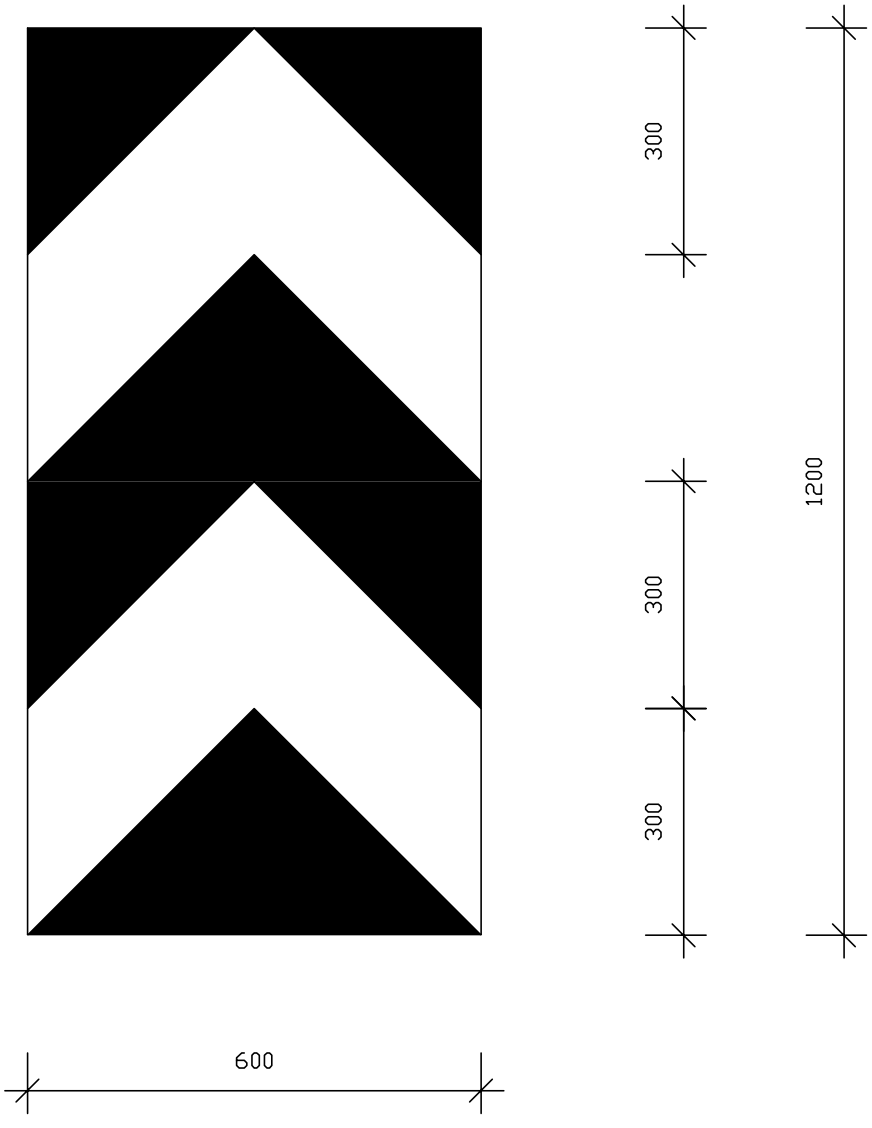

Pozn. Při užití jako stále dopravní zařízení se zaoblení rohů provádí dle podkladu. V případě plastového podkladu se zaoblení rohů činné plochy neprovádí.

6 VYBAVENÍ POZEMNÍCH KOMUNIKACÍ 6.3 DOPRAVNÍ ZAŘÍZENÍ Z 4c Směrovací deska středová	MINISTERSTVO DOPRAVY ODBOR POZEMNÍCH KOMUNIKACÍ VZOROVÉ LISTY	VL 6 Z 4c - 2 02.17

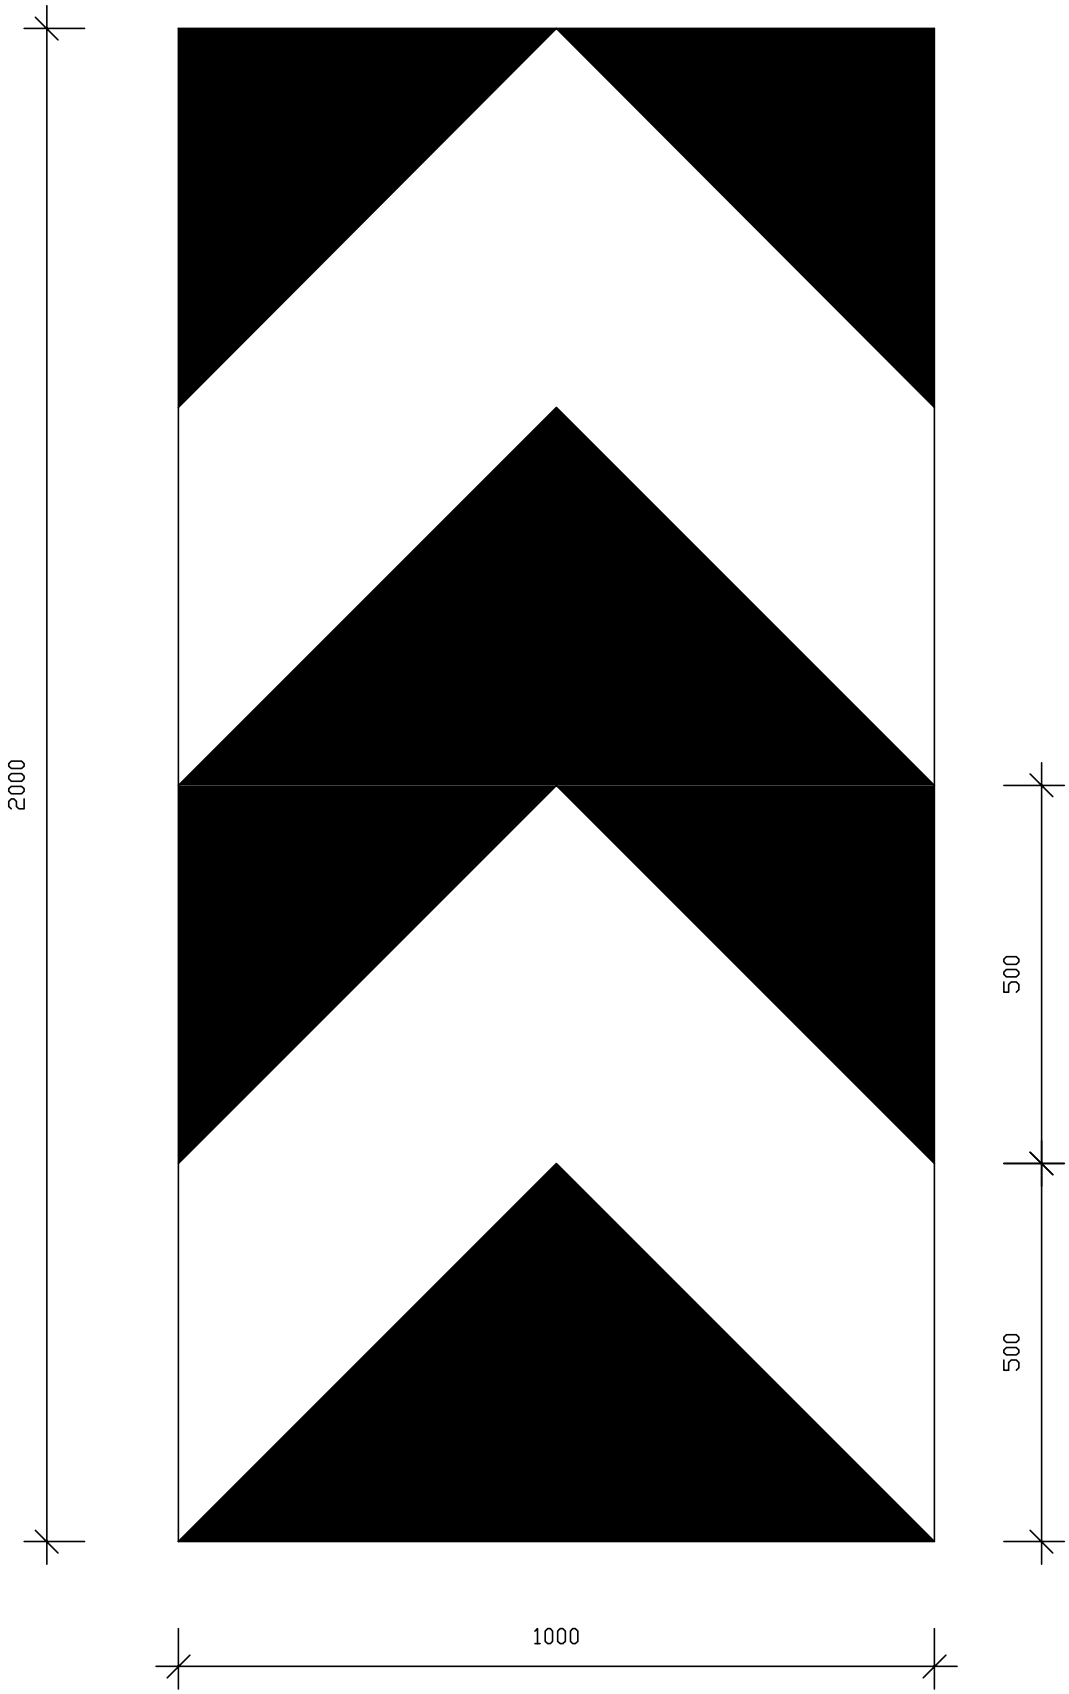





Z 4c

Pozn. Při užití jako stále dopravní zařízení se zaoblení rohů provádí dle podkladu. V případě plastového podkladu se zaoblení rohů činné plochy neprovádí.

6 VYBAVENÍ POZEMNÍCH KOMUNIKACÍ **6.3 DOPRAVNÍ ZAŘÍZENÍ** **Z 4c Směrovací deska středová**	**MINISTERSTVO DOPRAVY** **ODBOR POZEMNÍCH KOMUNIKACÍ** **VZOROVÉ LISTY**	**VL 6** **Z 4c - 3** **02.17**

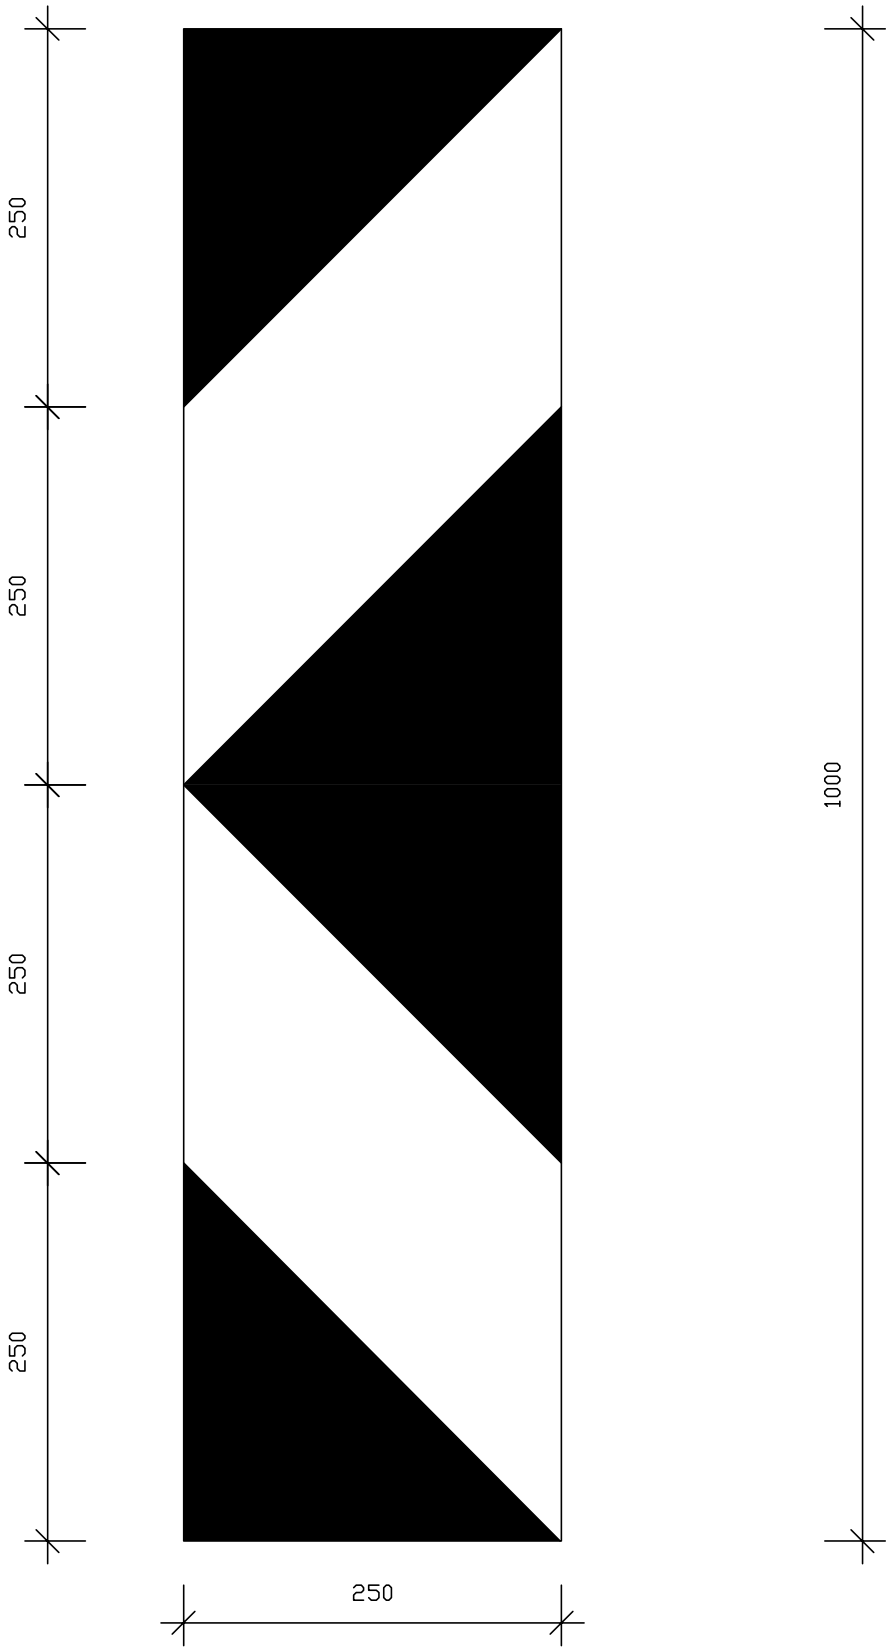


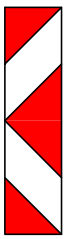


Z 4d

Pozn. Při užití jako stále dopravní zařízení se zaoblení rohů provádí dle podkladu. V případě plastového podkladu se zaoblení rohů činné plochy neprovádí.

6 VYBAVENÍ POZEMNÍCH KOMUNIKACÍ **6.3 DOPRAVNÍ ZAŘÍZENÍ** **Z 4d Směrovací deska se šipkou doleva**	**MINISTERSTVO DOPRAVY** **ODBOR POZEMNÍCH KOMUNIKACÍ** **VZOROVÉ LISTY**	**VL 6** **Z 4d** **02.17**

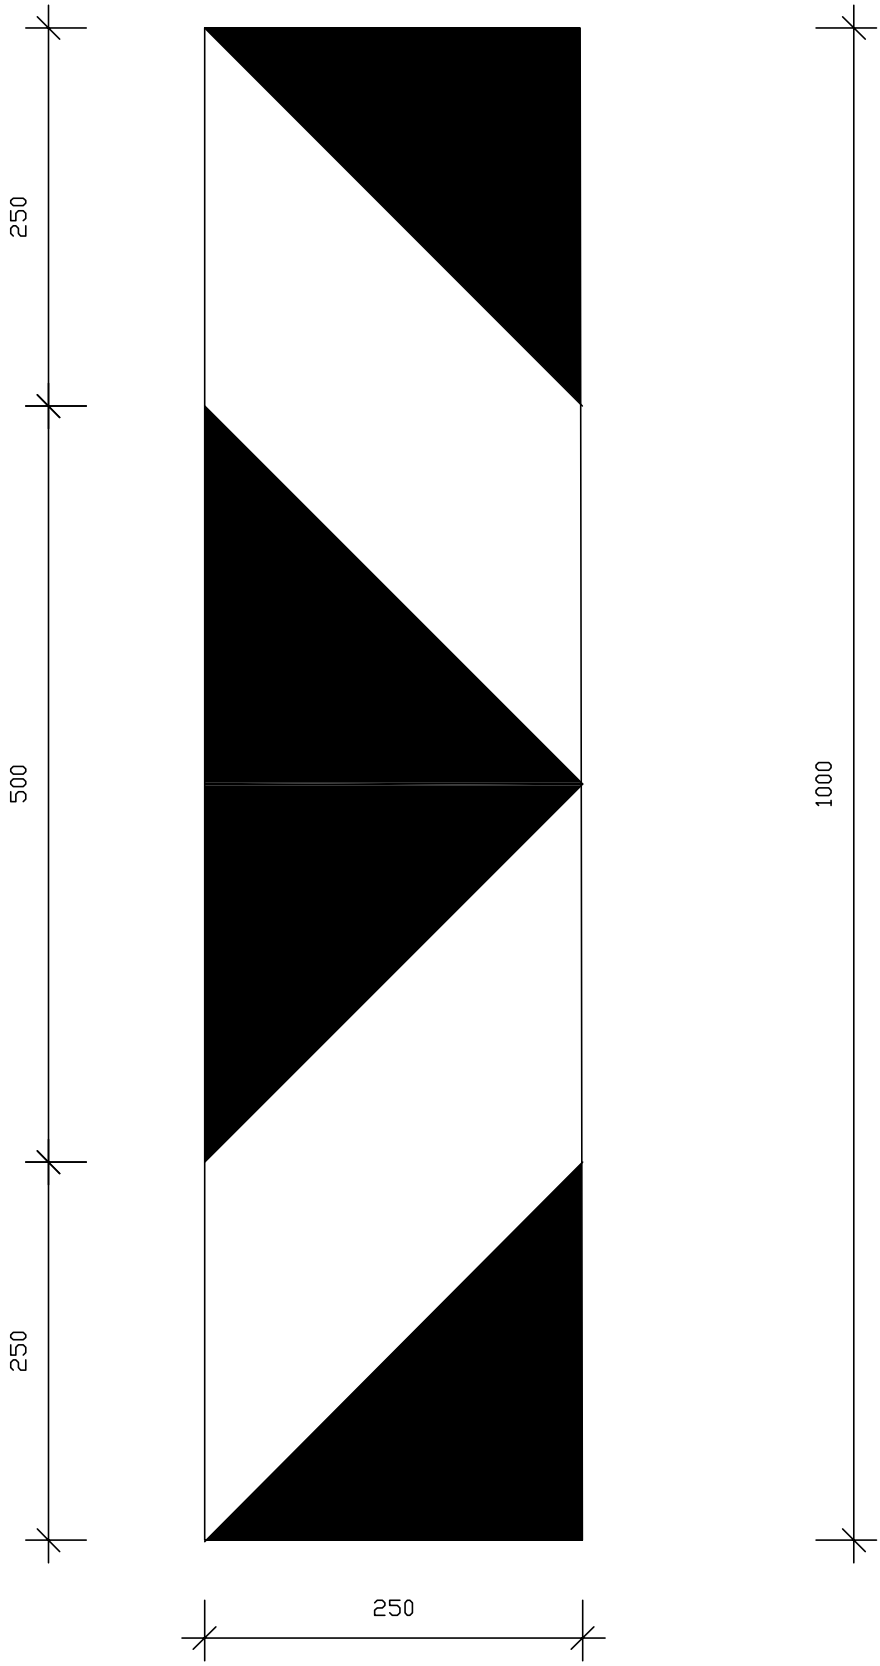


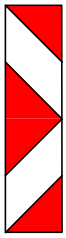


Z 4e

Pozn. Při užití jako stále dopravní zařízení se zaoblení rohů provádí dle podkladu. V případě plastového podkladu se zaoblení rohů činné plochy neprovádí.

6 VYBAVENÍ POZEMNÍCH KOMUNIKACÍ 6.3 DOPRAVNÍ ZAŘÍZENÍ Z 4e Směrovací deska se šipkou doprava	MINISTERSTVO DOPRAVY ODBOR POZEMNÍCH KOMUNIKACÍ VZOROVÉ LISTY	VL 6 Z 4e 02.17

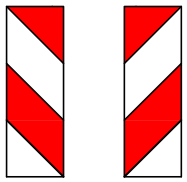



Z 5b Z 5a

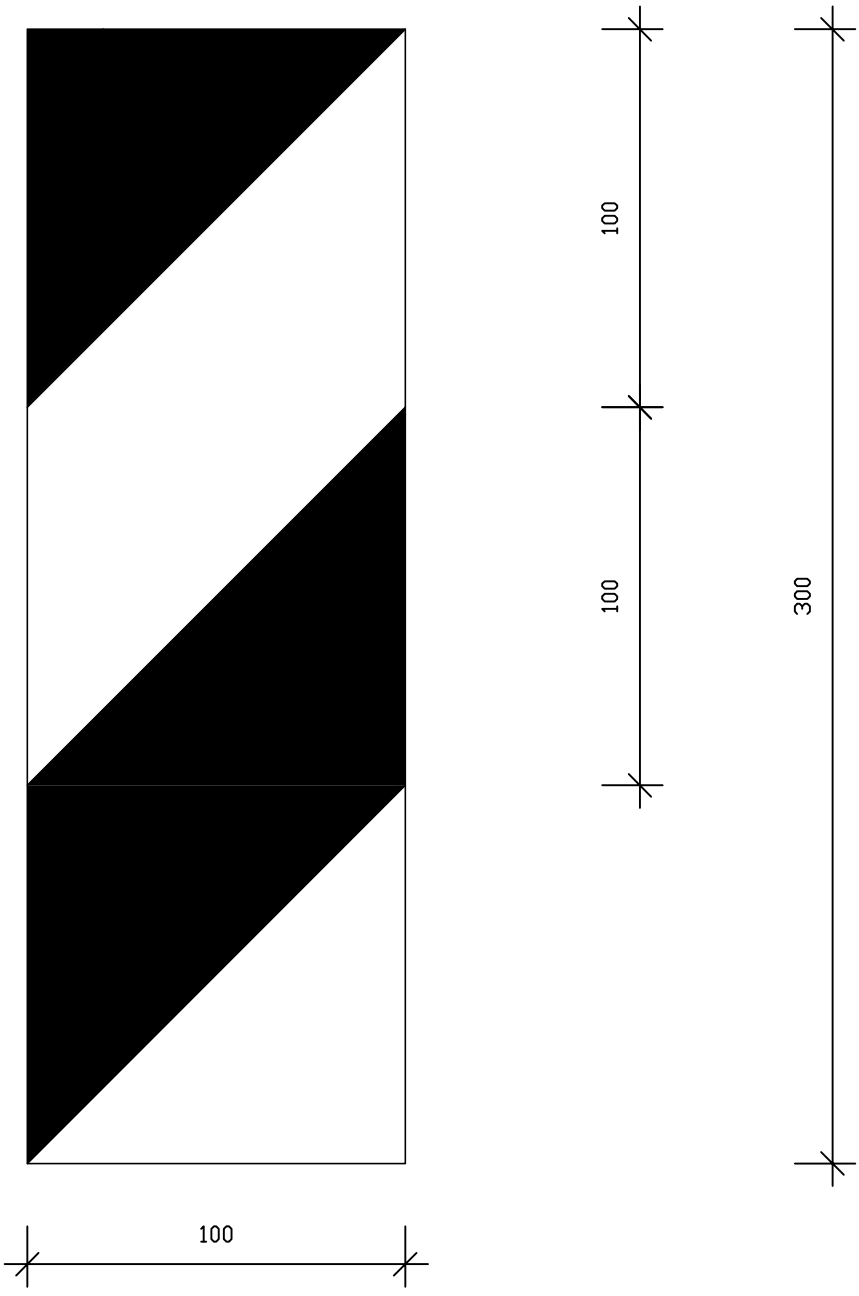

Pozn. Při užití jako stále dopravní zařízení se zaoblení rohů provádí dle podkladu. V případě plastového podkladu se zaoblení rohů činné plochy neprovádí.

6 VYBAVENÍ POZEMNÍCH KOMUNIKACÍ 6.3 DOPRAVNÍ ZAŘÍZENÍ Z 5a,b Vodicí deska se šikmými pruhy	MINISTERSTVO DOPRAVY ODBOR POZEMNÍCH KOMUNIKACÍ VZOROVÉ LISTY	VL 6 Z 5a,b - 1 02.17

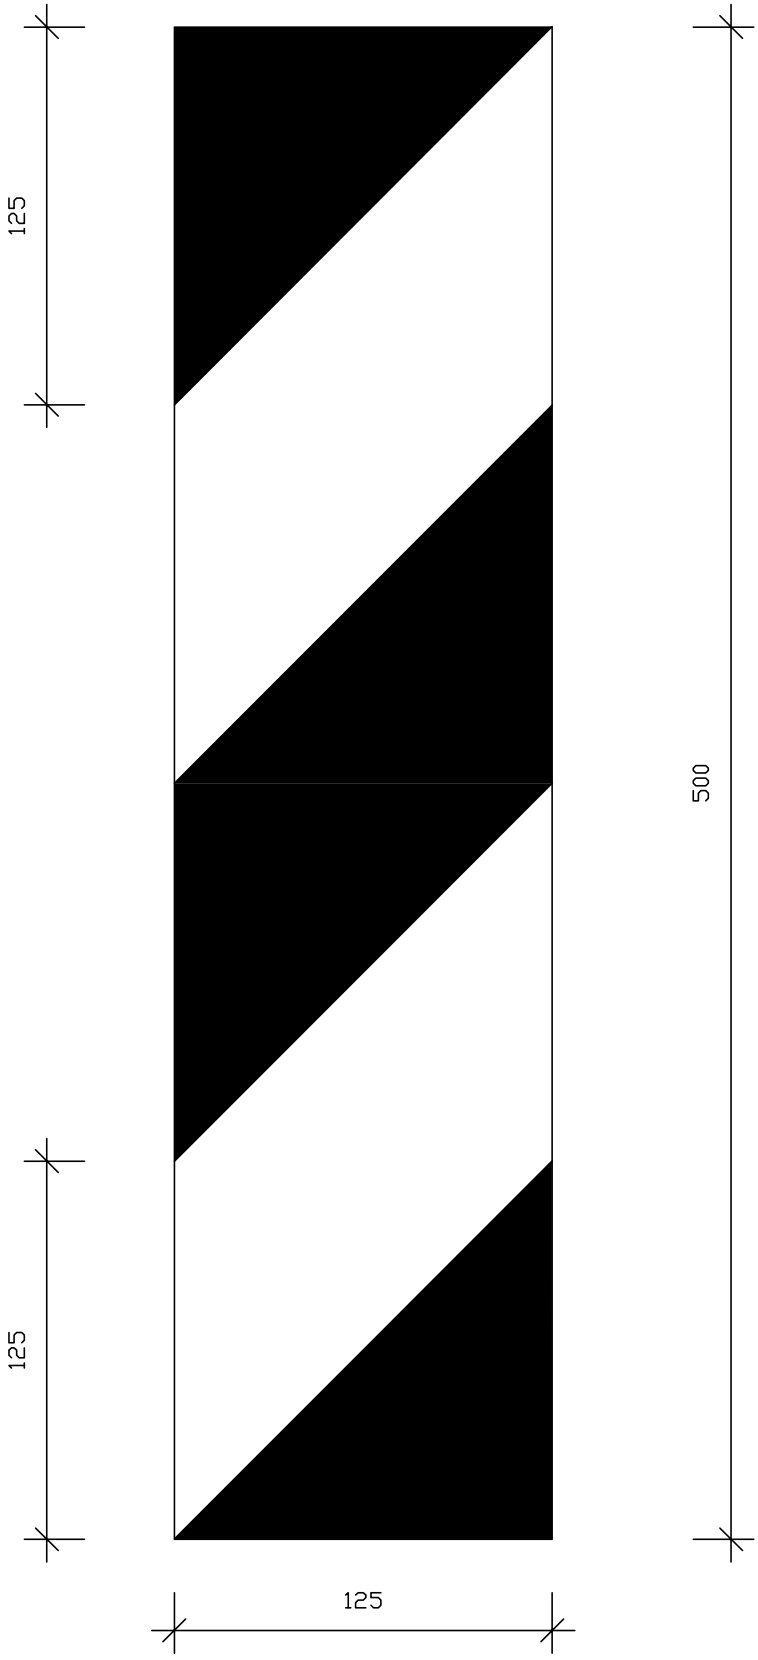


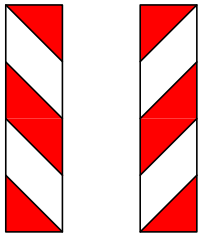


Z 5b Z 5a

Pozn. Při užití jako stále dopravní zařízení se zaoblení rohů provádí dle podkladu. V případě plastového podkladu se zaoblení rohů činné plochy neprovádí.

6 VYBAVENÍ POZEMNÍCH KOMUNIKACÍ 6.3 DOPRAVNÍ ZAŘÍZENÍ Z 5a,b Vodicí deska se šikmými pruhy	MINISTERSTVO DOPRAVY ODBOR POZEMNÍCH KOMUNIKACÍ VZOROVÉ LISTY	VL 6 Z 5a,b - 2 02.17

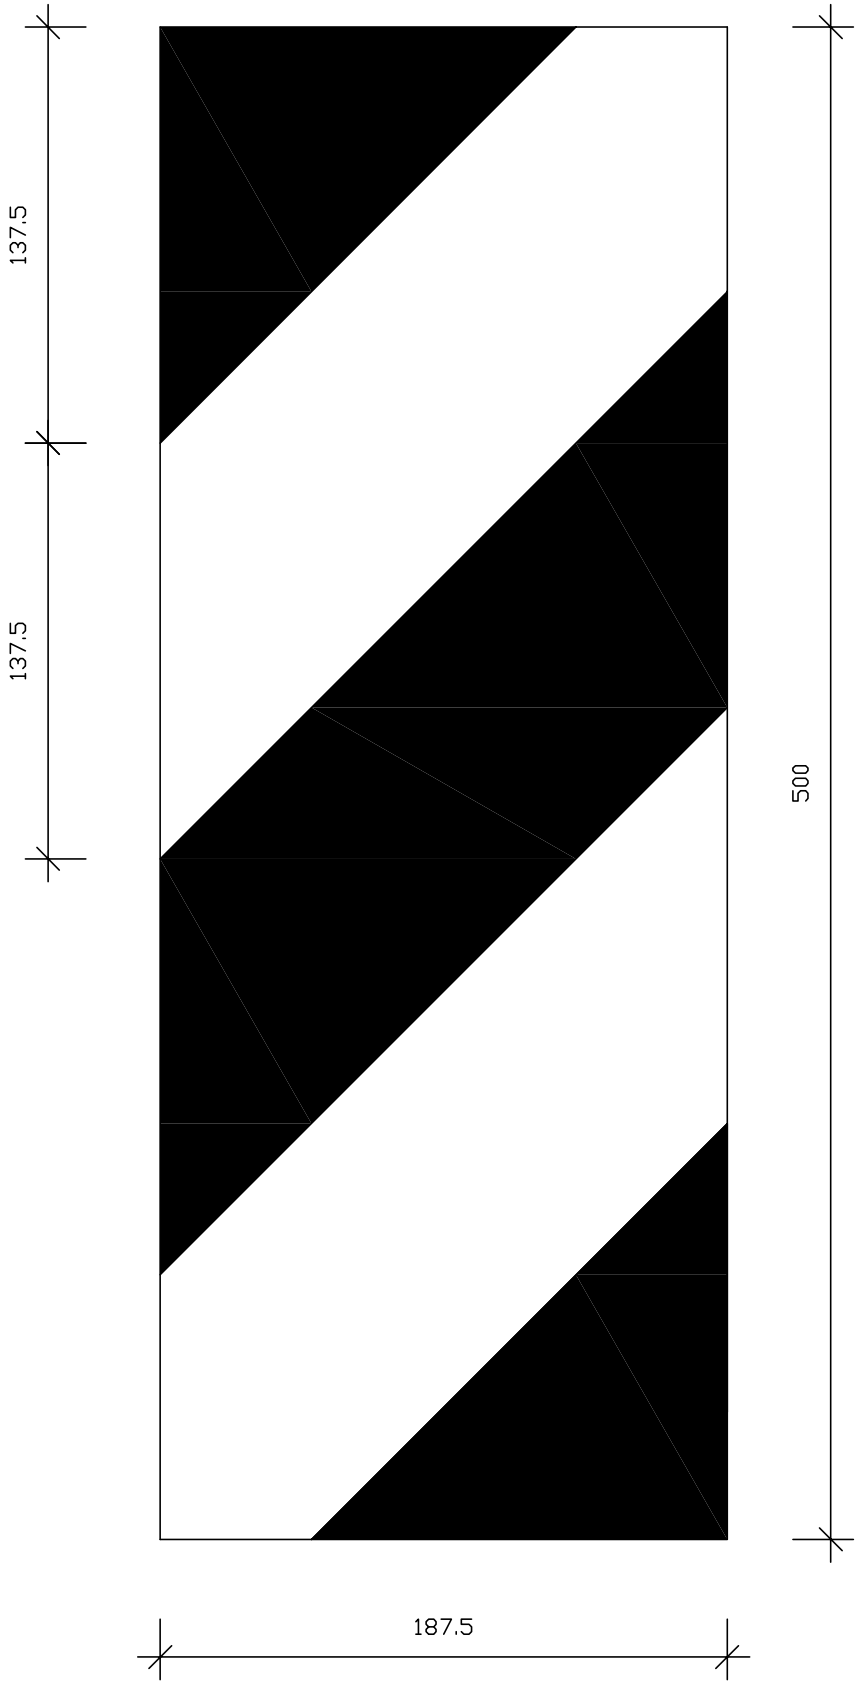


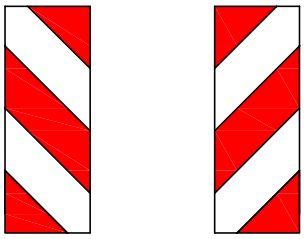


Z 5b Z 5a

Pozn. Při užití jako stále dopravní zařízení se zaoblení rohů provádí dle podkladu. V případě plastového podkladu se zaoblení rohů činné plochy neprovádí.

6 VYBAVENÍ POZEMNÍCH KOMUNIKACÍ 6.3 DOPRAVNÍ ZAŘÍZENÍ Z 5a,b Vodicí deska se šikmými pruhy	MINISTERSTVO DOPRAVY ODBOR POZEMNÍCH KOMUNIKACÍ VZOROVÉ LISTY	VL 6 Z 5a,b - 3 02.17

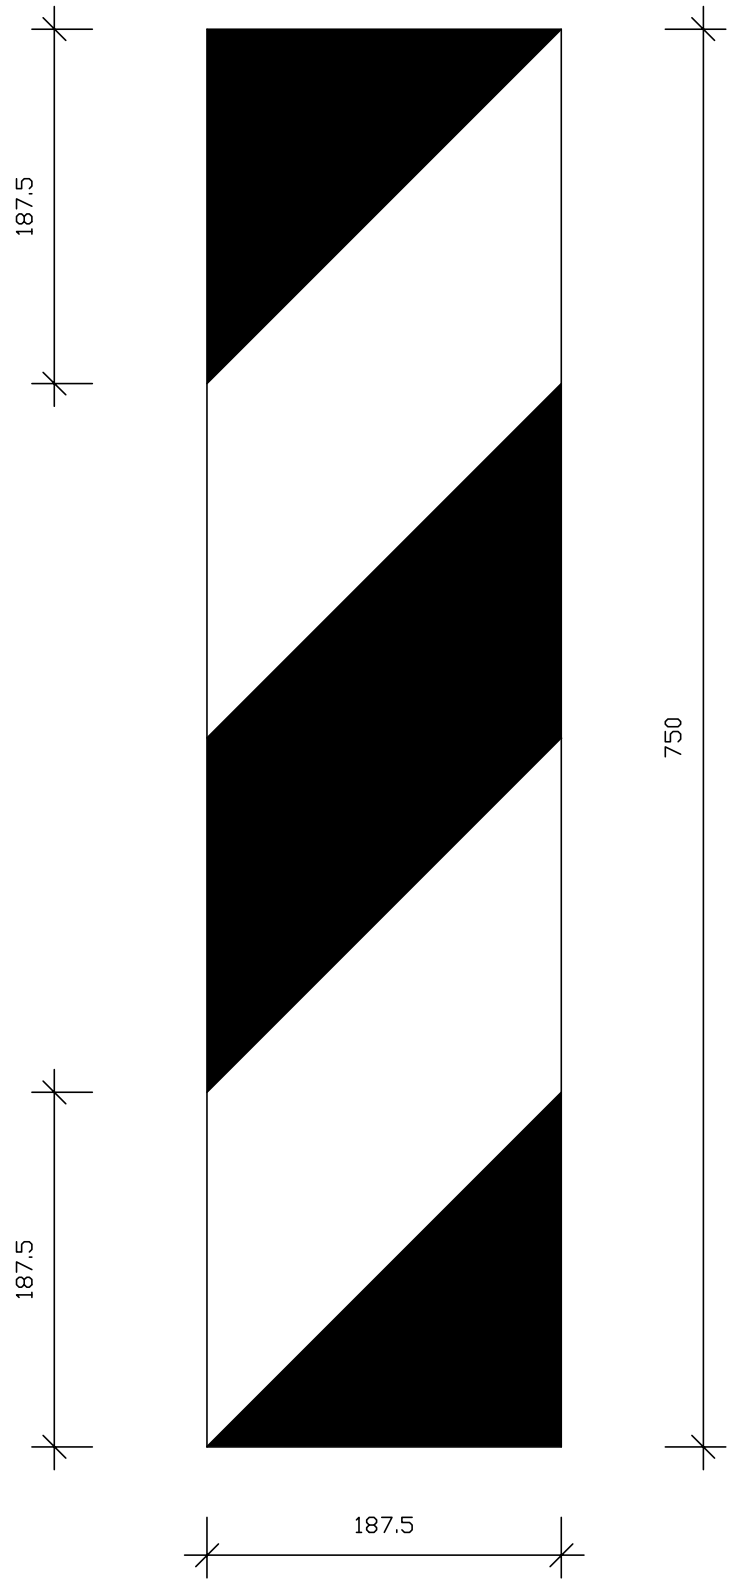


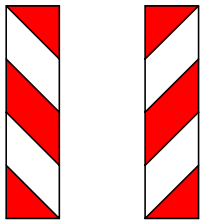


Z 5b Z 5a

Pozn. Při užití jako stále dopravní zařízení se zaoblení rohů provádí dle podkladu. V případě plastového podkladu se zaoblení rohů činné plochy neprovádí.

6 VYBAVENÍ POZEMNÍCH KOMUNIKACÍ 6.3 DOPRAVNÍ ZAŘÍZENÍ Z 5a,b Vodicí deska se šikmými pruhy	MINISTERSTVO DOPRAVY ODBOR POZEMNÍCH KOMUNIKACÍ VZOROVÉ LISTY	VL 6 Z 5a,b - 4 02.17

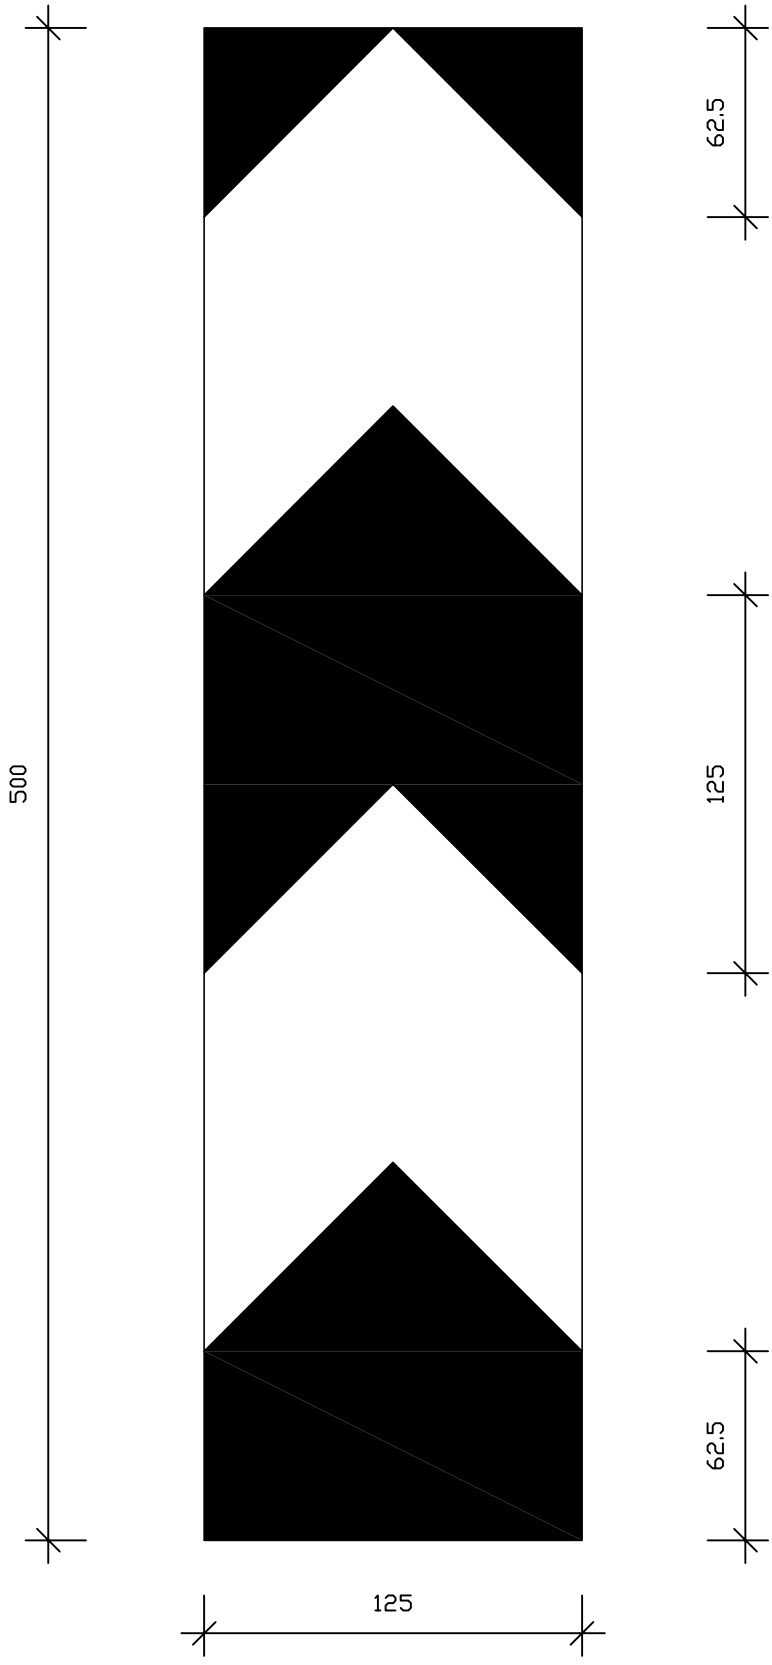


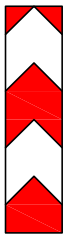


Z 5c

Pozn. Při užití jako stále dopravní zařízení se zaoblení rohů provádí dle podkladu. V případě plastového podkladu se zaoblení rohů činné plochy neprovádí.

6 VYBAVENÍ POZEMNÍCH KOMUNIKACÍ **6.3 DOPRAVNÍ ZAŘÍZENÍ** **Z 5c Vodicí deska středová se šikmými pruhy**	**MINISTERSTVO DOPRAVY** **ODBOR POZEMNÍCH KOMUNIKACÍ** **VZOROVÉ LISTY**	**VL 6** **Z 5c - 1** **02.17**

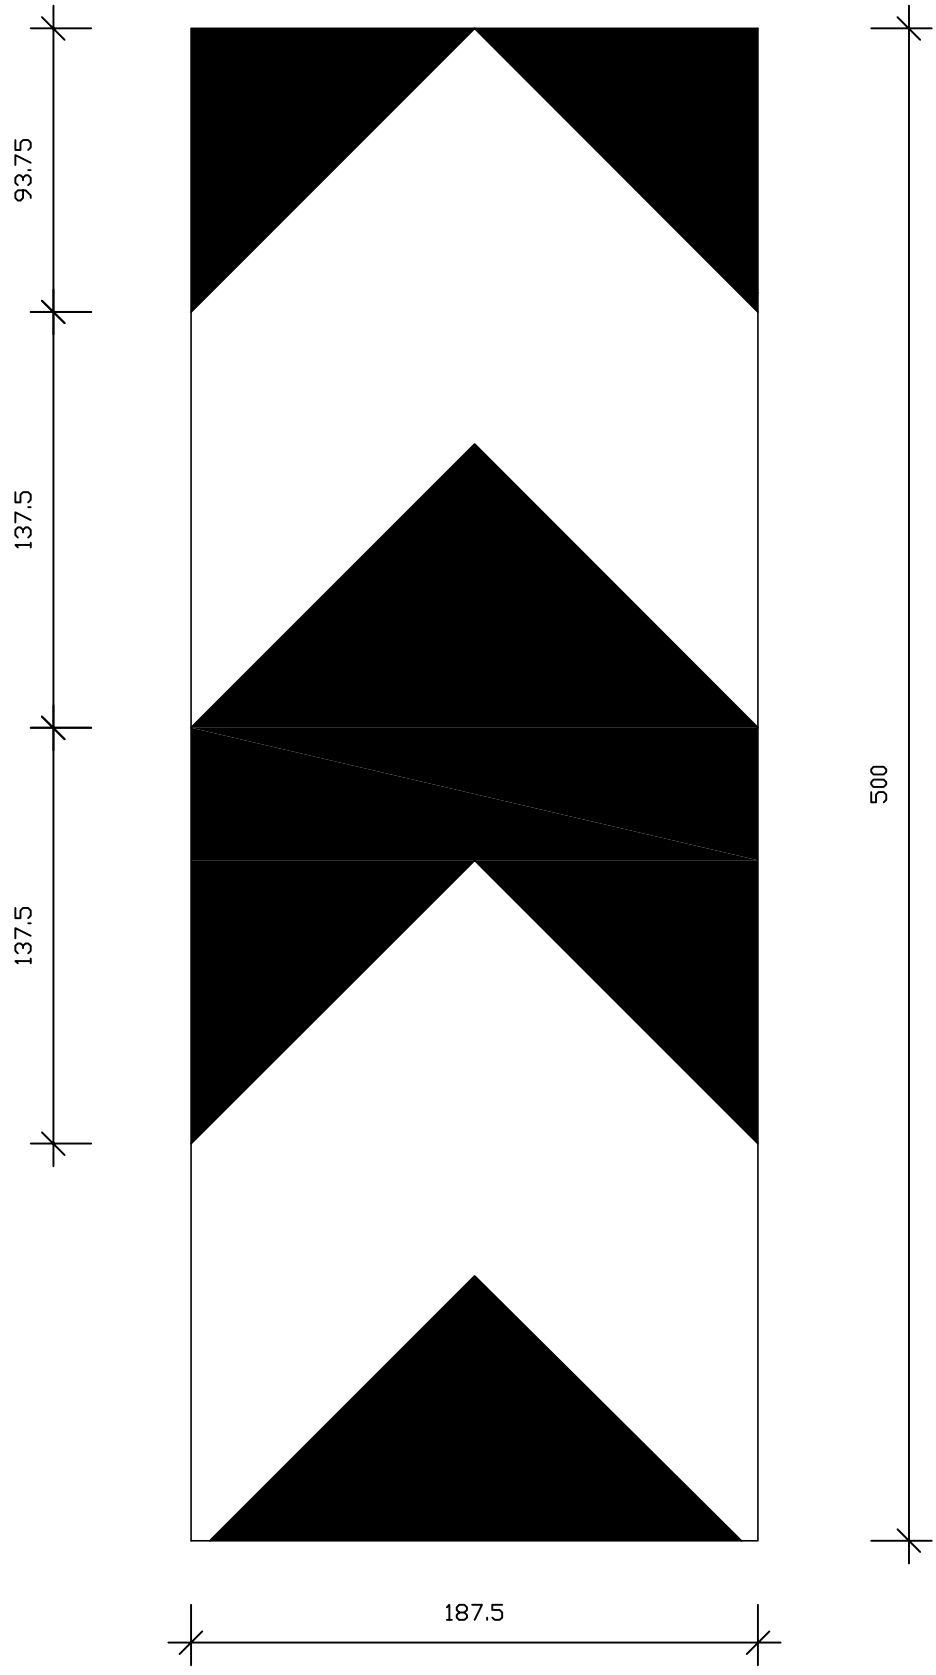


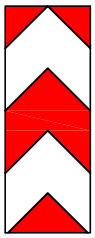

Z 5c

Pozn. Při užití jako stále dopravní zařízení se zaoblení rohů provádí dle podkladu. V případě plastového podkladu se zaoblení rohů činné plochy neprovádí.

6 VYBAVENÍ POZEMNÍCH KOMUNIKACÍ 6.3 DOPRAVNÍ ZAŘÍZENÍ Z 5c Vodicí deska středová se šikmými pruhy	MINISTERSTVO DOPRAVY ODBOR POZEMNÍCH KOMUNIKACÍ VZOROVÉ LISTY	VL 6 Z 5c - 2 02.17

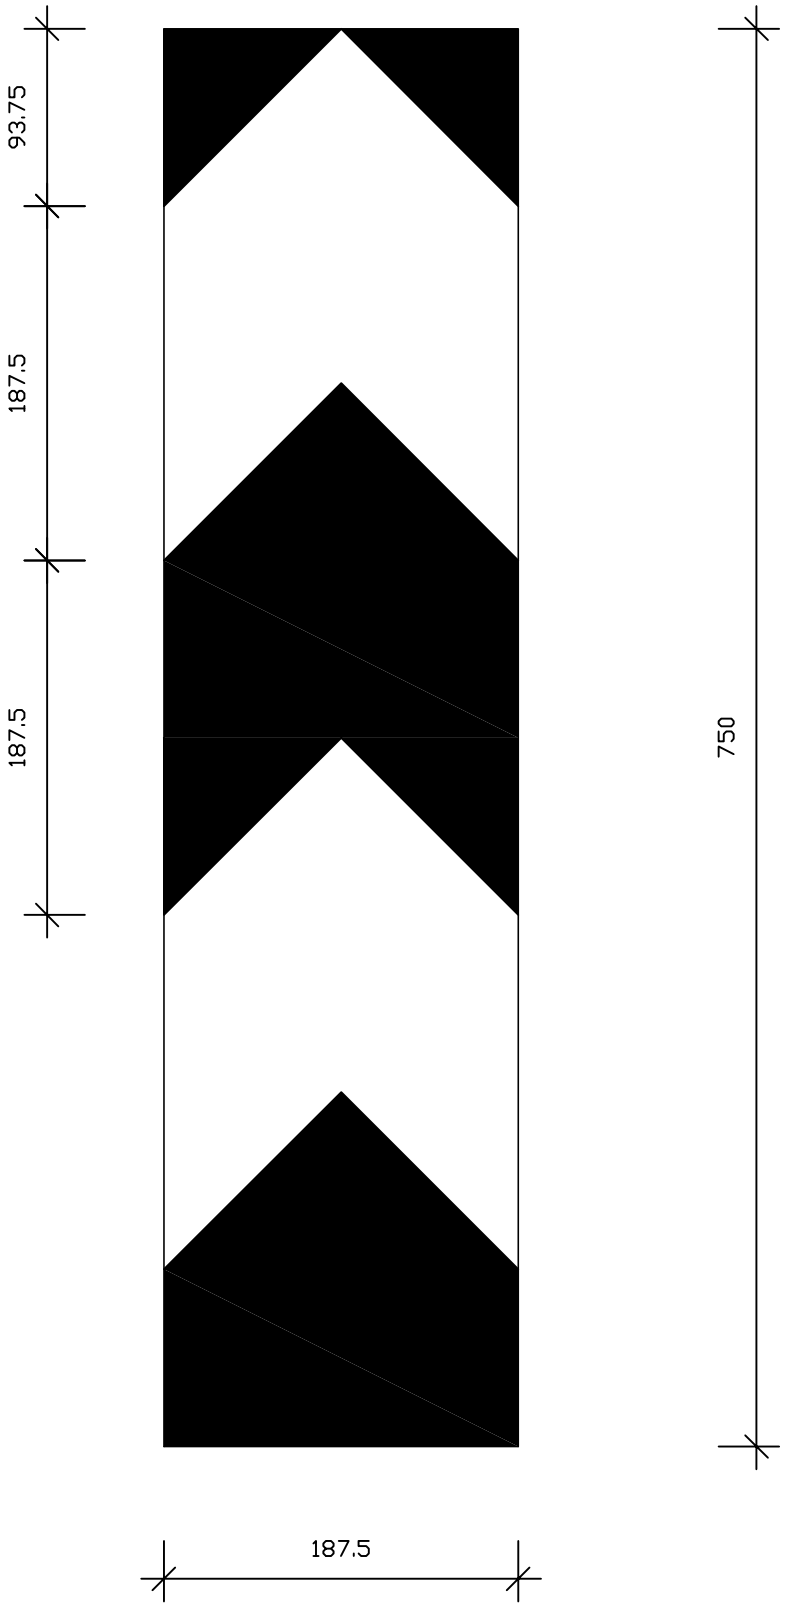




Z 5c

Pozn. Při užití jako stále dopravní zařízení se zaoblení rohů provádí dle podkladu. V případě plastového podkladu se zaoblení rohů činné plochy neprovádí.

6 VYBAVENÍ POZEMNÍCH KOMUNIKACÍ 6.3 DOPRAVNÍ ZAŘÍZENÍ Z 5c Vodicí deska středová se šikmými pruhy	MINISTERSTVO DOPRAVY ODBOR POZEMNÍCH KOMUNIKACÍ VZOROVÉ LISTY	VL 6 Z 5c - 3 02.17




Z 6a

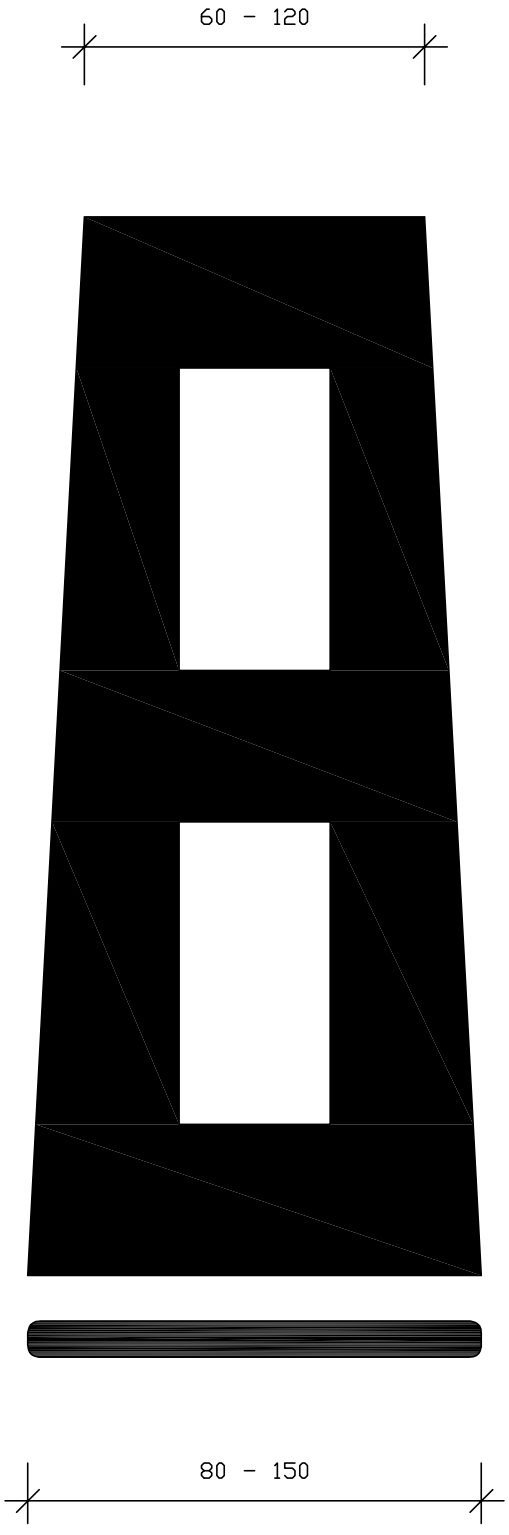


Pozn. Musí být doplněno plochou z retroreflexního materiálu min. o ploše 10 cm².

6 VYBAVENÍ POZEMNÍCH KOMUNIKACÍ 6.3 DOPRAVNÍ ZAŘÍZENÍ Z 6a Velká zvýrazňující deska	MINISTERSTVO DOPRAVY ODBOR POZEMNÍCH KOMUNIKACÍ VZOROVÉ LISTY	VL 6 Z 6a 02.17

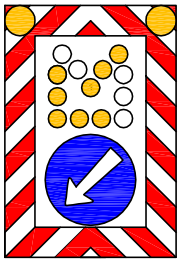


Z 7

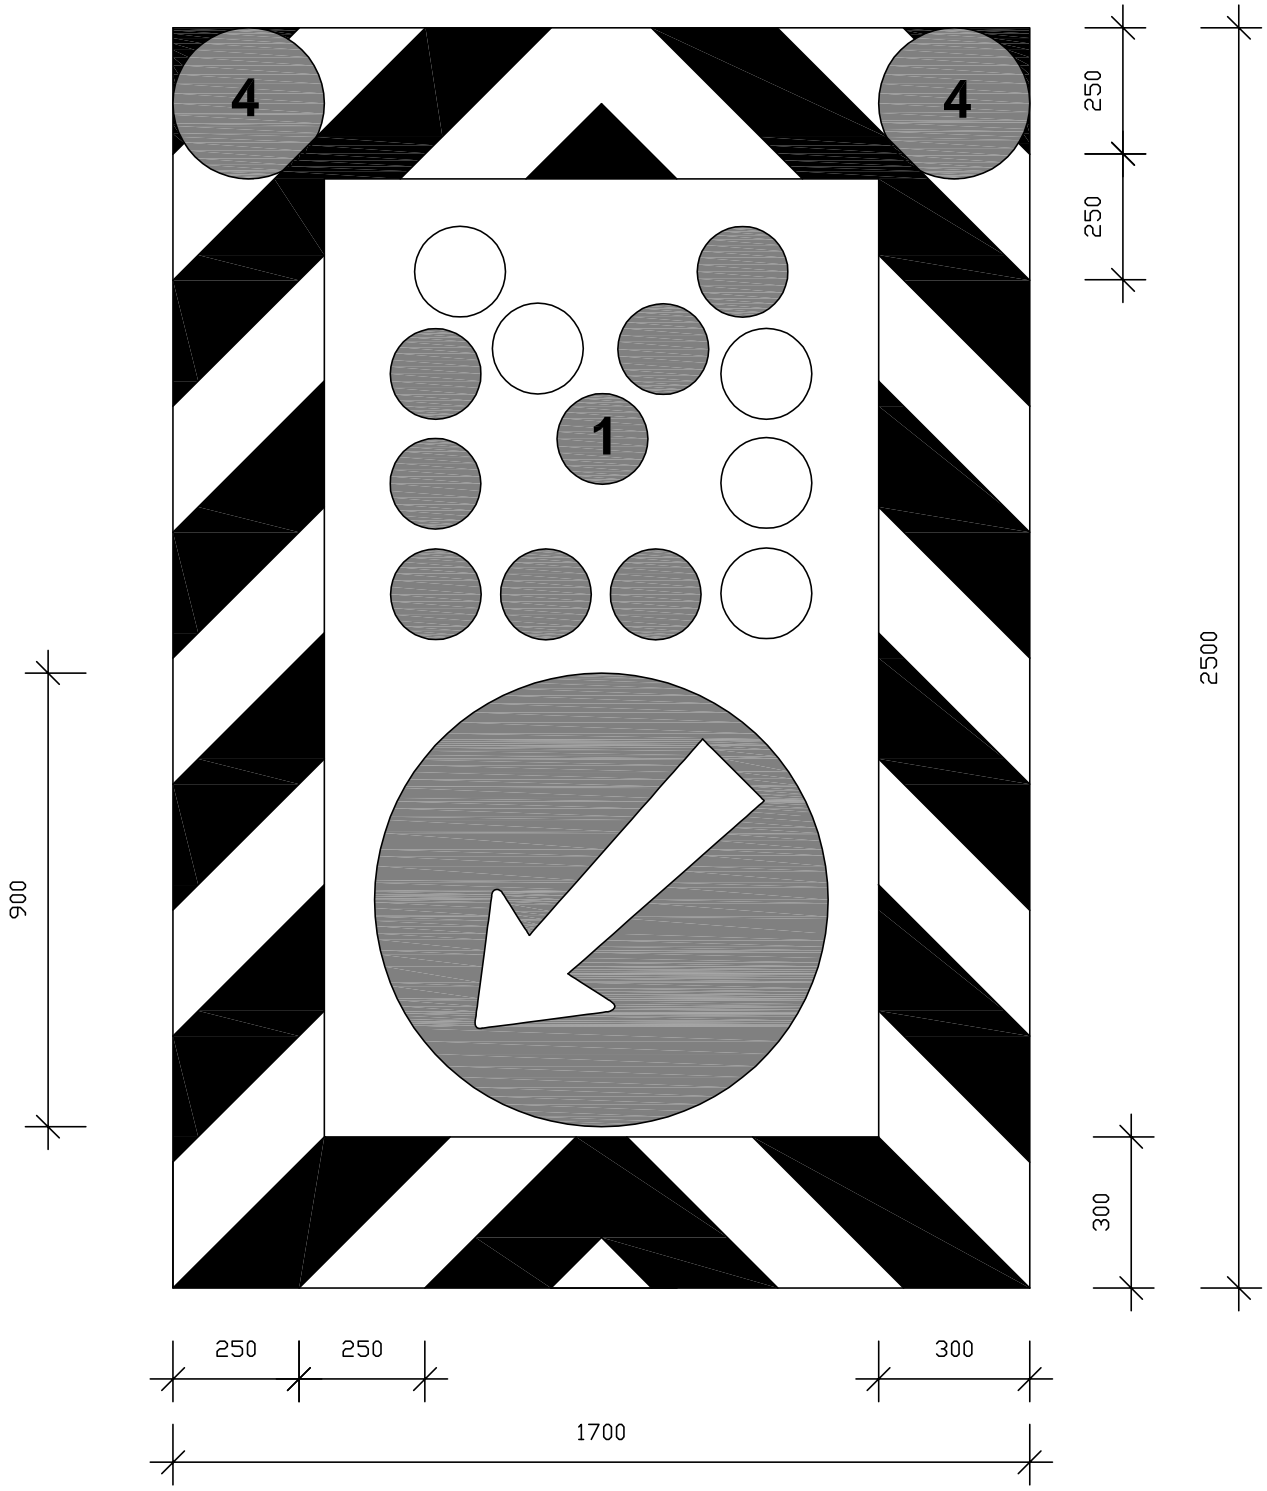


Pozn.: 1 – výstražné světlo typ 1 (L8H), 4 – výstražné světlo typ 4 (L9H).

6 VYBAVENÍ POZEMNÍCH KOMUNIKACÍ 6.3 DOPRAVNÍ ZAŘÍZENÍ Z 7 Pojízdná uzavírková tabule - Typ II	MINISTERSTVO DOPRAVY ODBOR POZEMNÍCH KOMUNIKACÍ VZOROVÉ LISTY	VL 6 Z 7 - 1 02.17

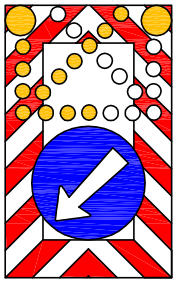


Z 7

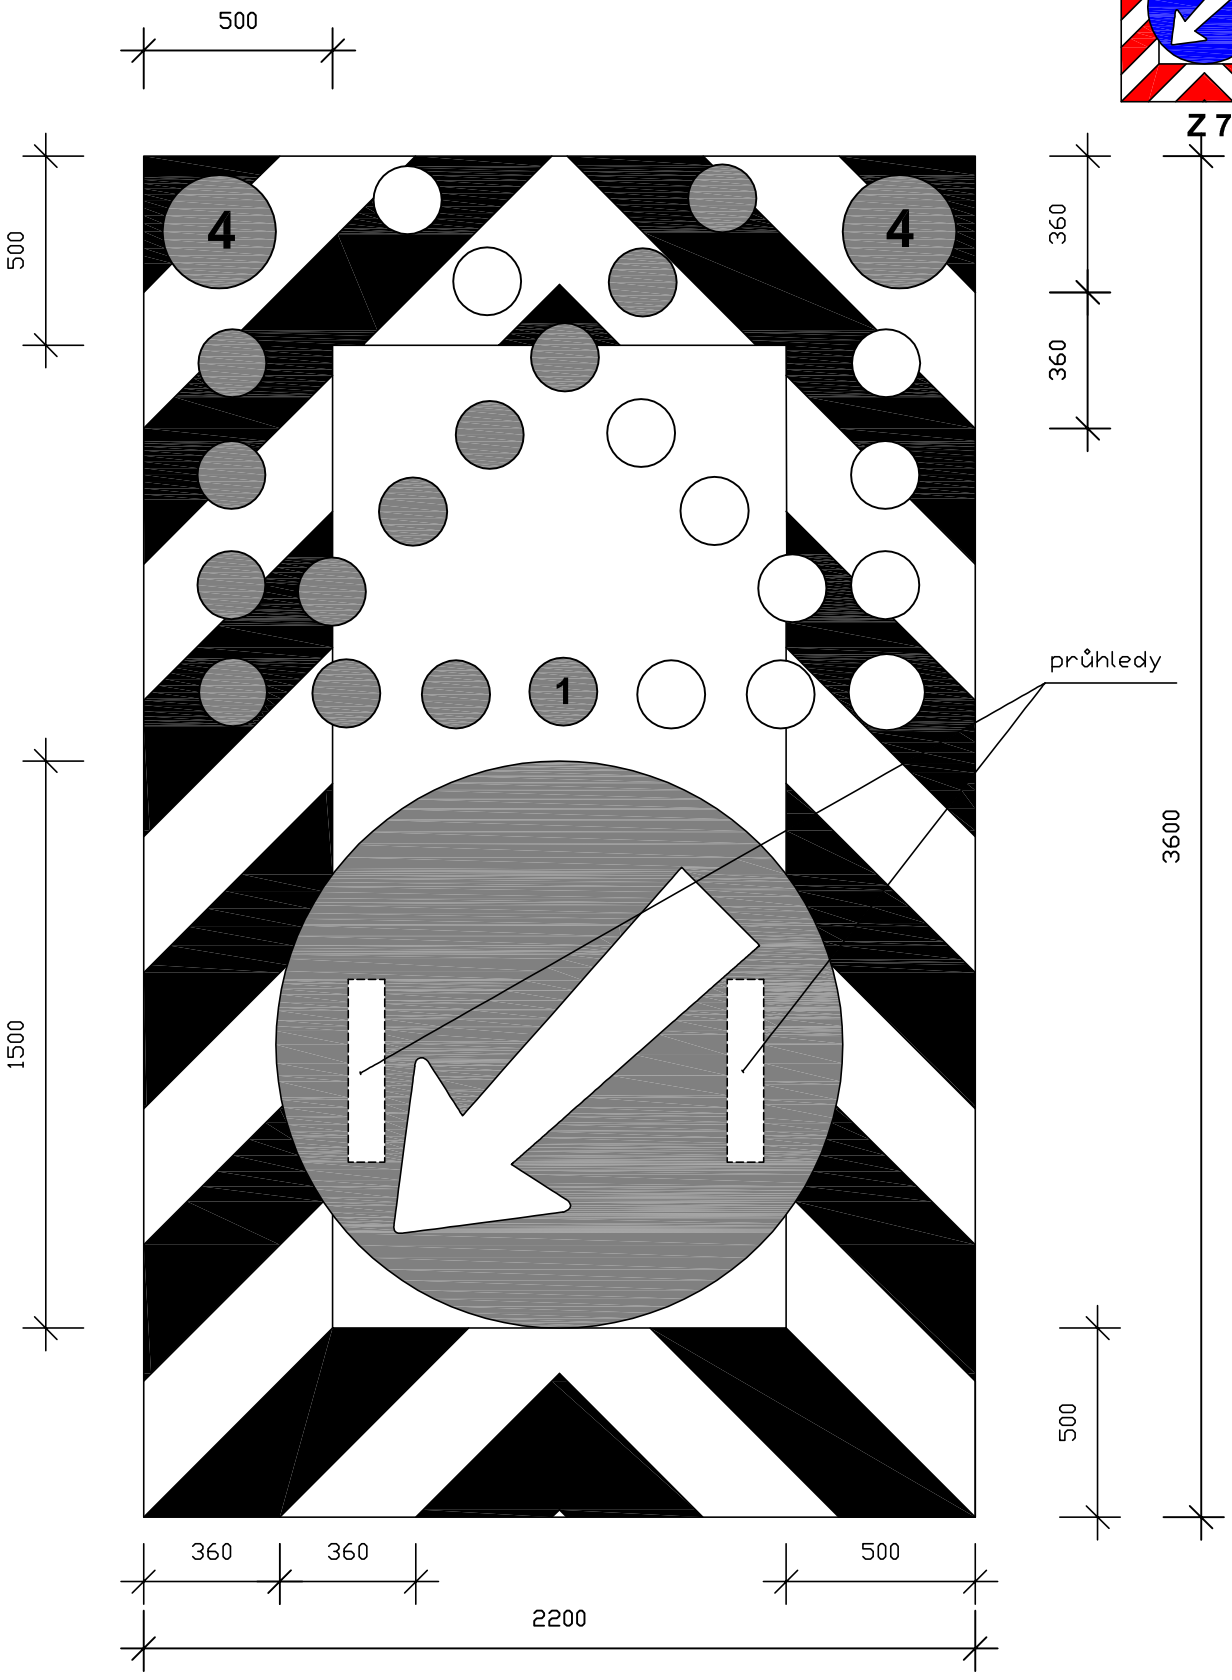



Pozn.: 1 – výstražné světlo typ 1 (L8H), 4 – výstražné světlo typ 4 (L9H)
Velikost průhledu min. 0,1 m².

6 VYBAVENÍ POZEMNÍCH KOMUNIKACÍ 6.3 DOPRAVNÍ ZAŘÍZENÍ Z 7 Pojízdná uzavírková tabule	MINISTERSTVO DOPRAVY ODBOR POZEMNÍCH KOMUNIKACÍ VZOROVÉ LISTY	VL 6 Z 7 - 2 02.17

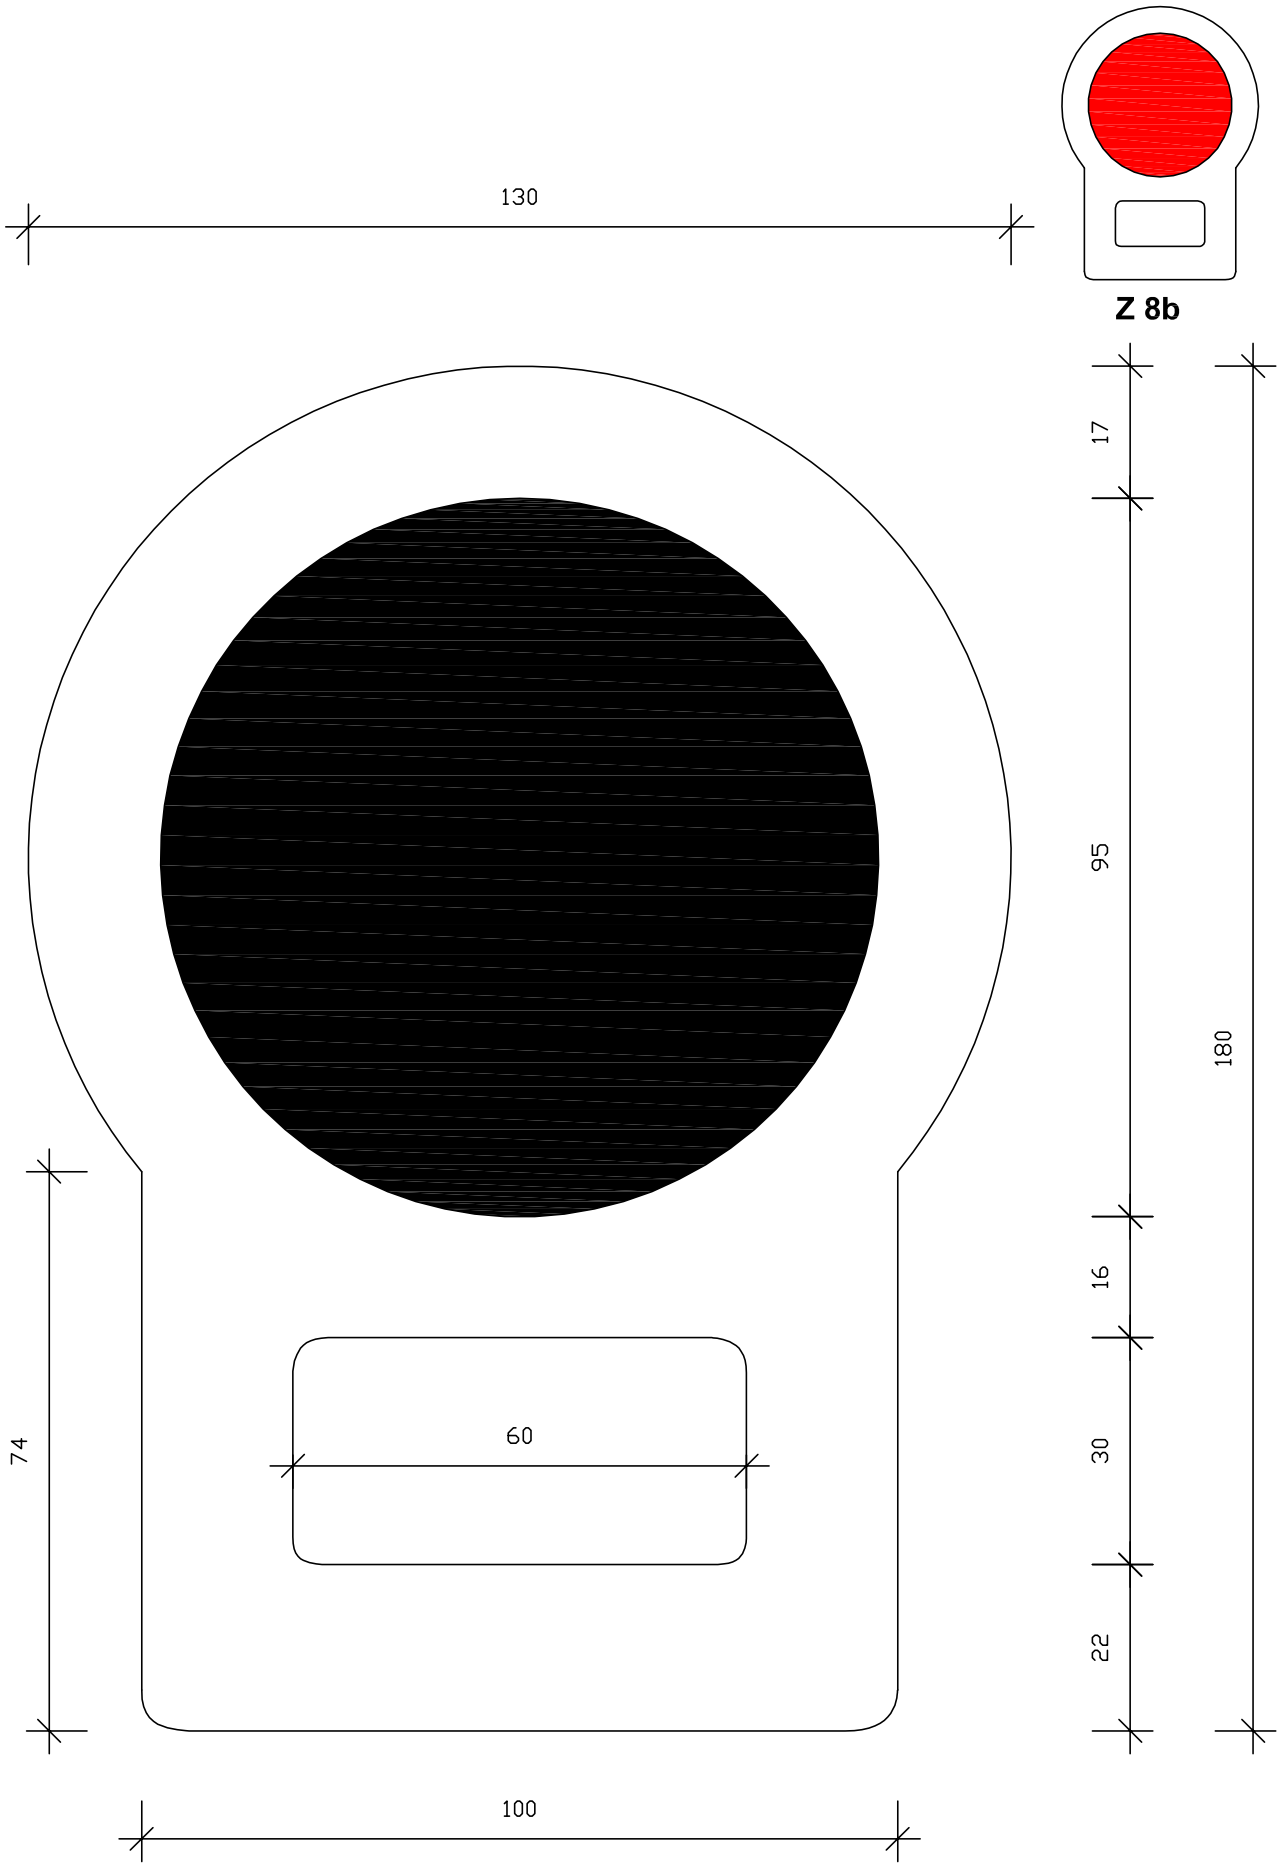


6 6.3 Z 8b Zastavovací terč pro jiné osoby	VYBAVENÍ POZEMNÍCH KOMUNIKACÍ DOPRAVNÍ ZAŘÍZENÍ	MINISTERSTVO DOPRAVY ODBOR POZEMNÍCH KOMUNIKACÍ VZOROVÉ LISTY	VL 6 Z 8b 02.17

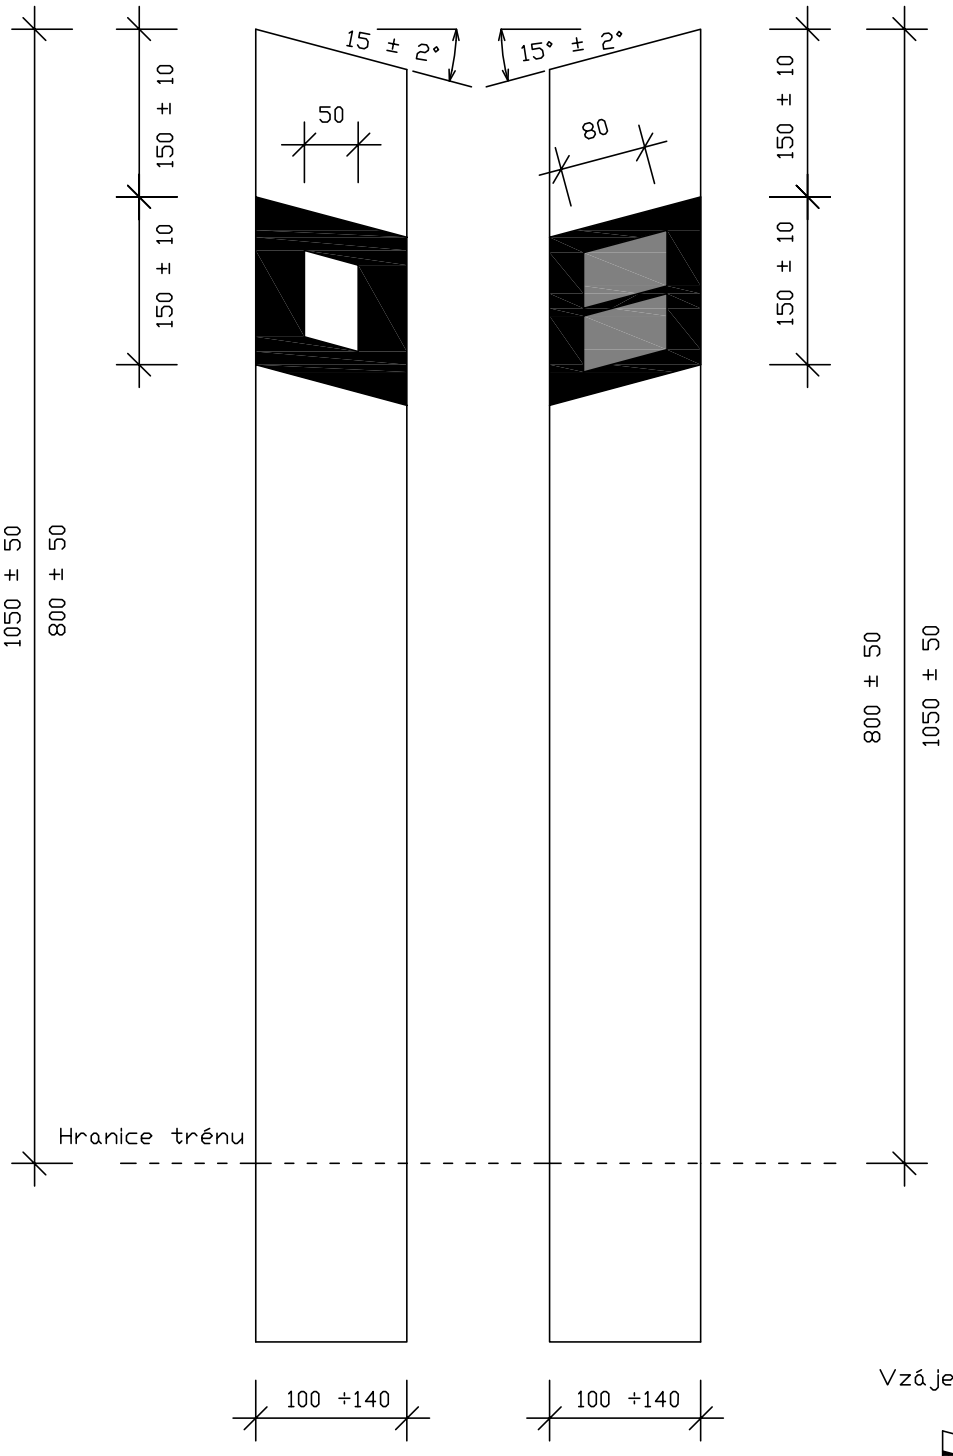

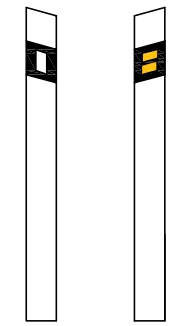


Z 11a **Z 11b**


Vzájemná poloha Z 11a – Z 11b

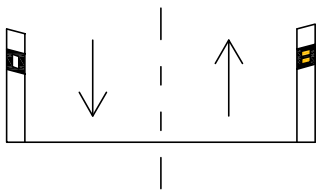

Pozn.: Další podrobnosti viz TP 58.


6 **6.3**	**VYBAVENÍ POZEMNÍCH KOMUNIKACÍ** **DOPRAVNÍ ZAŘÍZENÍ** **Z 11a,b Směrový sloupek bílý**	**MINISTERSTVO DOPRAVY** **ODBOR POZEMNÍCH KOMUNIKACÍ** **VZOROVÉ LISTY**	**VL 6** **Z 11a,b** **02.17**

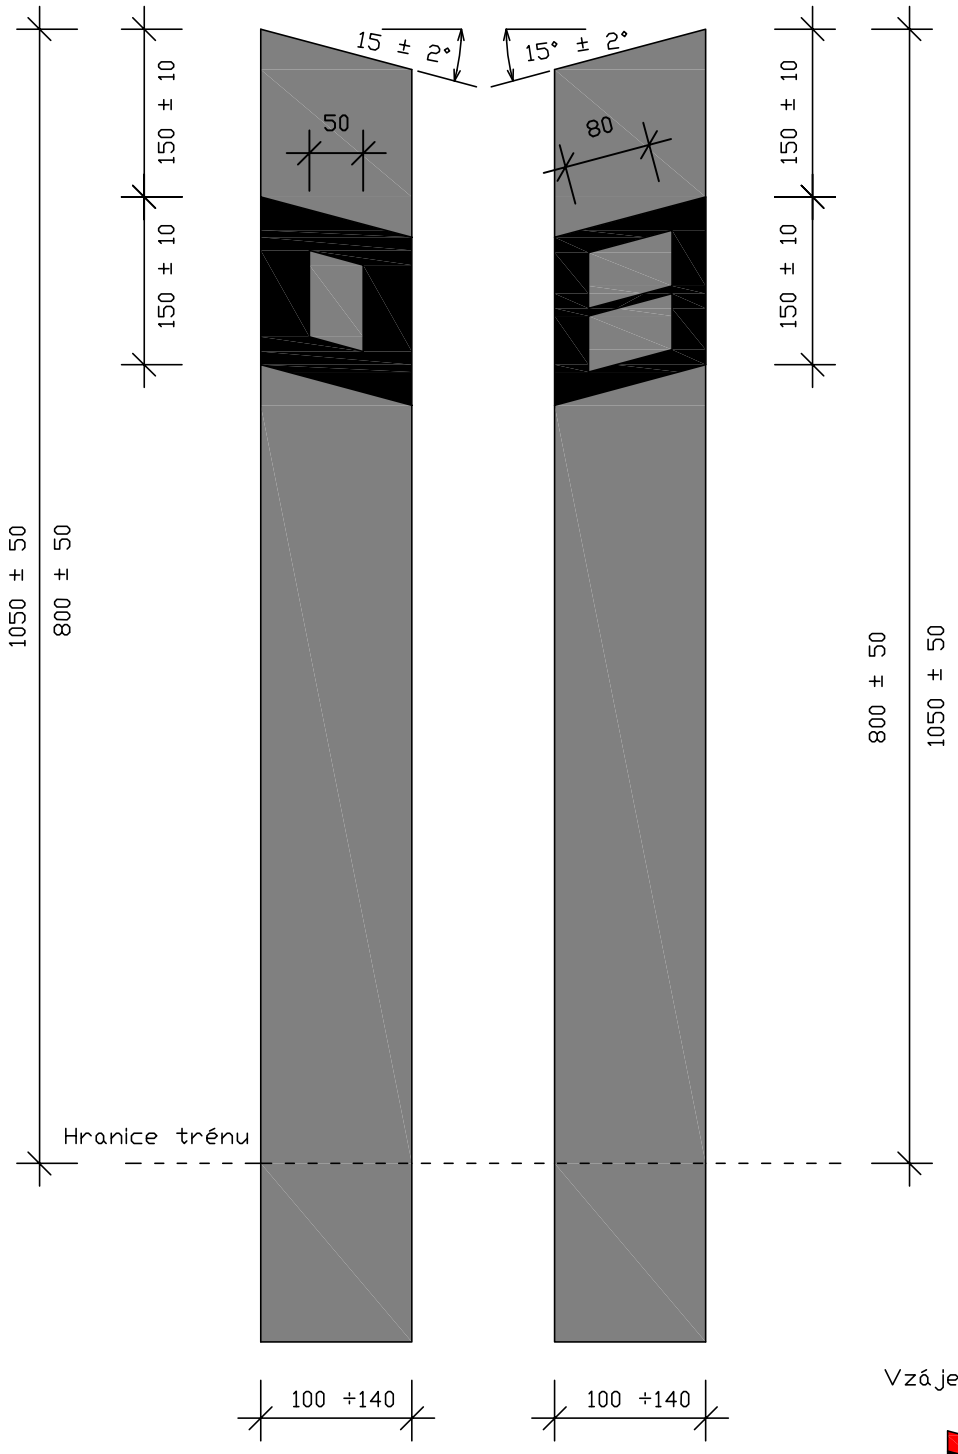

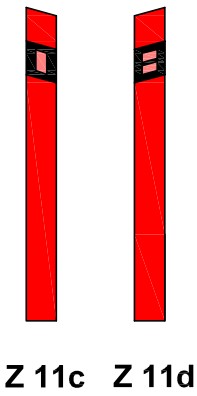


Z 11c Z 11d


Vzájemná poloha Z 11c – Z 11d

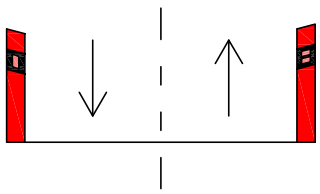

Pozn.: Další podrobnosti viz TP 58.


6 VYBAVENÍ POZEMNÍCH KOMUNIKACÍ **6.3 DOPRAVNÍ ZAŘÍZENÍ** **Z 11c,d Směrový sloupek červený**	**MINISTERSTVO DOPRAVY** **ODBOR POZEMNÍCH KOMUNIKACÍ** **VZOROVÉ LISTY**	**VL 6** **Z 11c,d** **02.17**

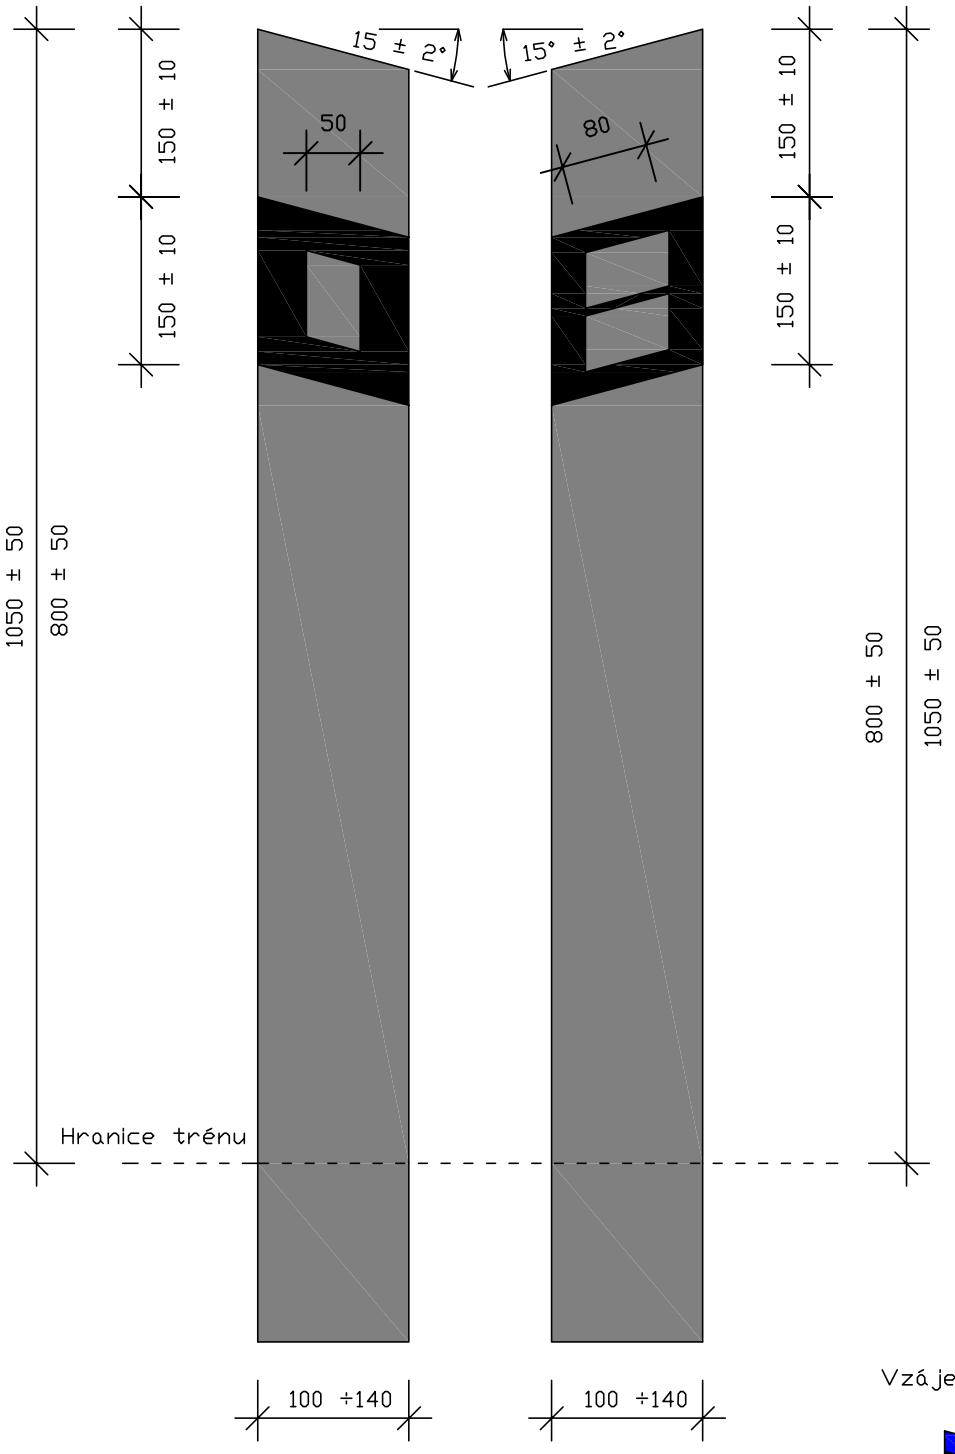

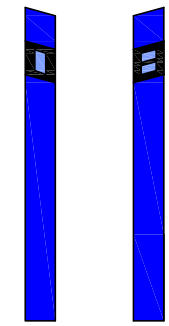


Z 11e Z 11f

Vzájemná poloha Z 11e – Z 11f

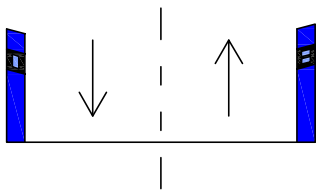


Pozn.: Další podrobnosti viz TP 58.


6 VYBAVENÍ POZEMNÍCH KOMUNIKACÍ **6.3 DOPRAVNÍ ZAŘÍZENÍ** **Z 11e,f Směrový sloupek modrý**	**MINISTERSTVO DOPRAVY** **ODBOR POZEMNÍCH KOMUNIKACÍ** **VZOROVÉ LISTY**	**VL 6** **Z 11e,f** **02.17**

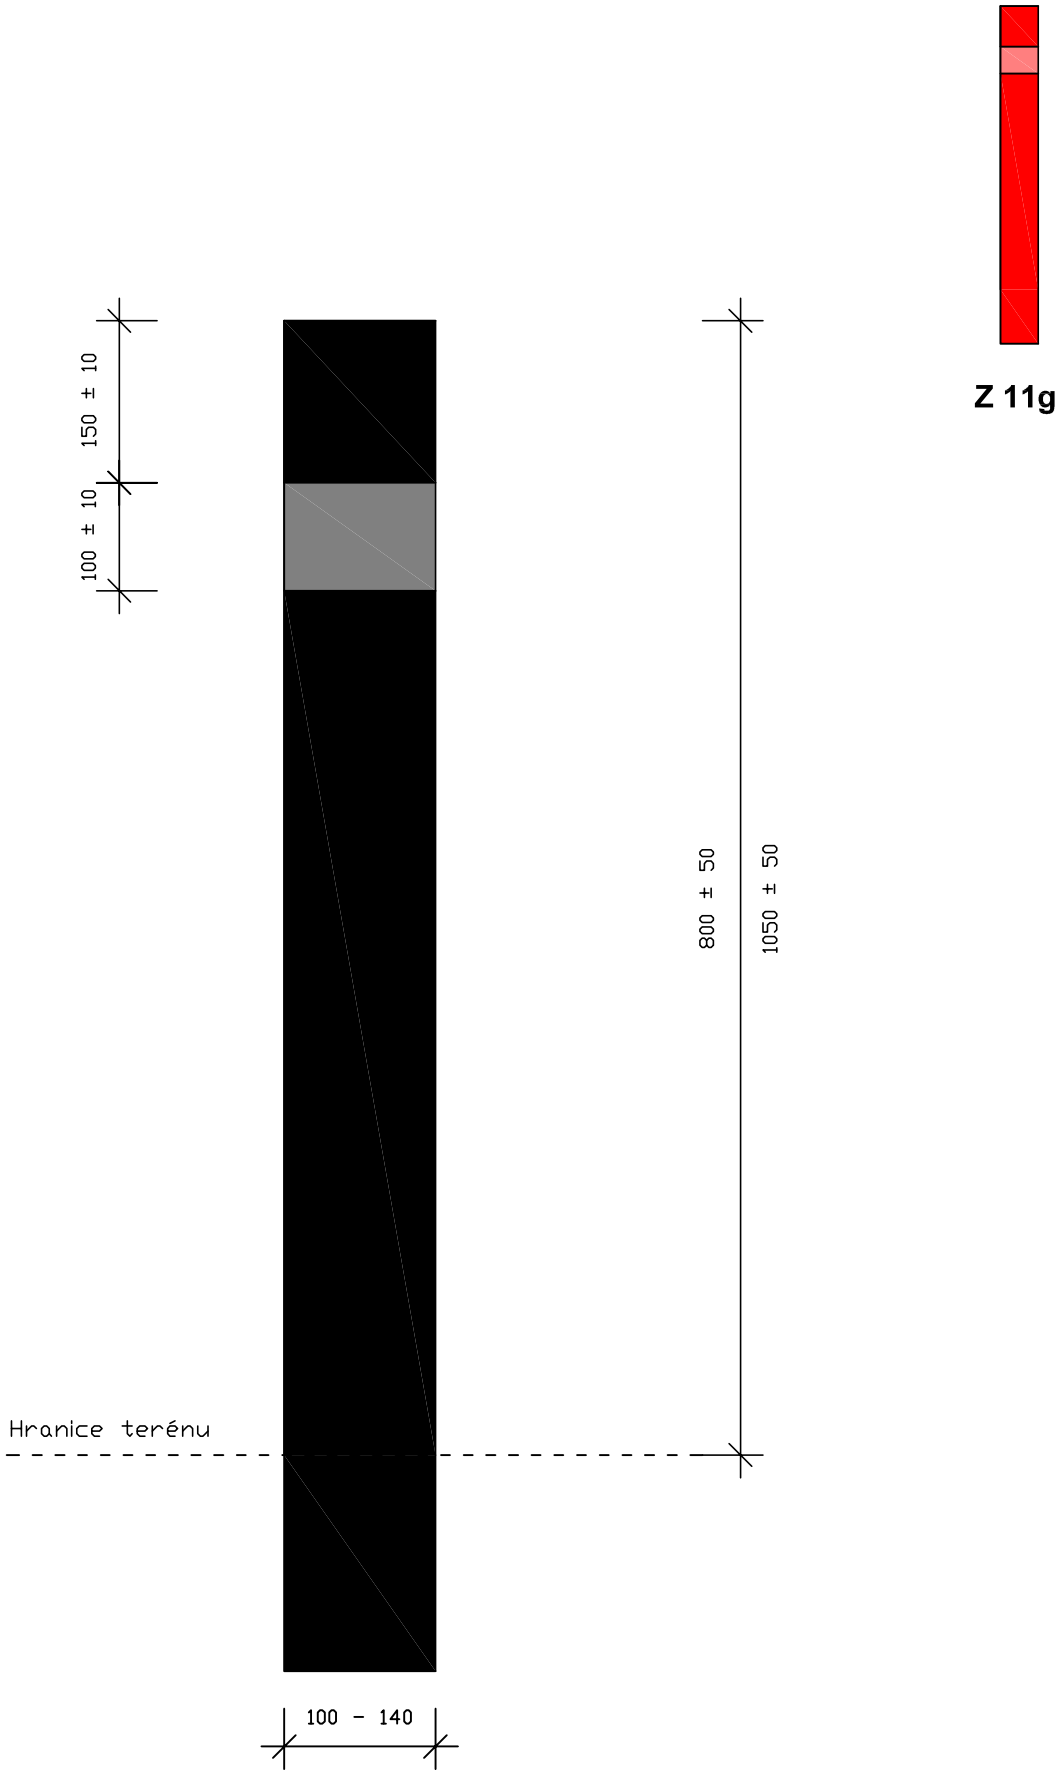

Pozn.: Další podrobnosti viz TP 58.

6 6.3	VYBAVENÍ POZEMNÍCH KOMUNIKACÍ DOPRAVNÍ ZAŘÍZENÍ Z 11g Směrový sloupek červený kulatý	MINISTERSTVO DOPRAVY ODBOR POZEMNÍCH KOMUNIKACÍ VZOROVÉ LISTY	VL 6 Z 11g 02.17

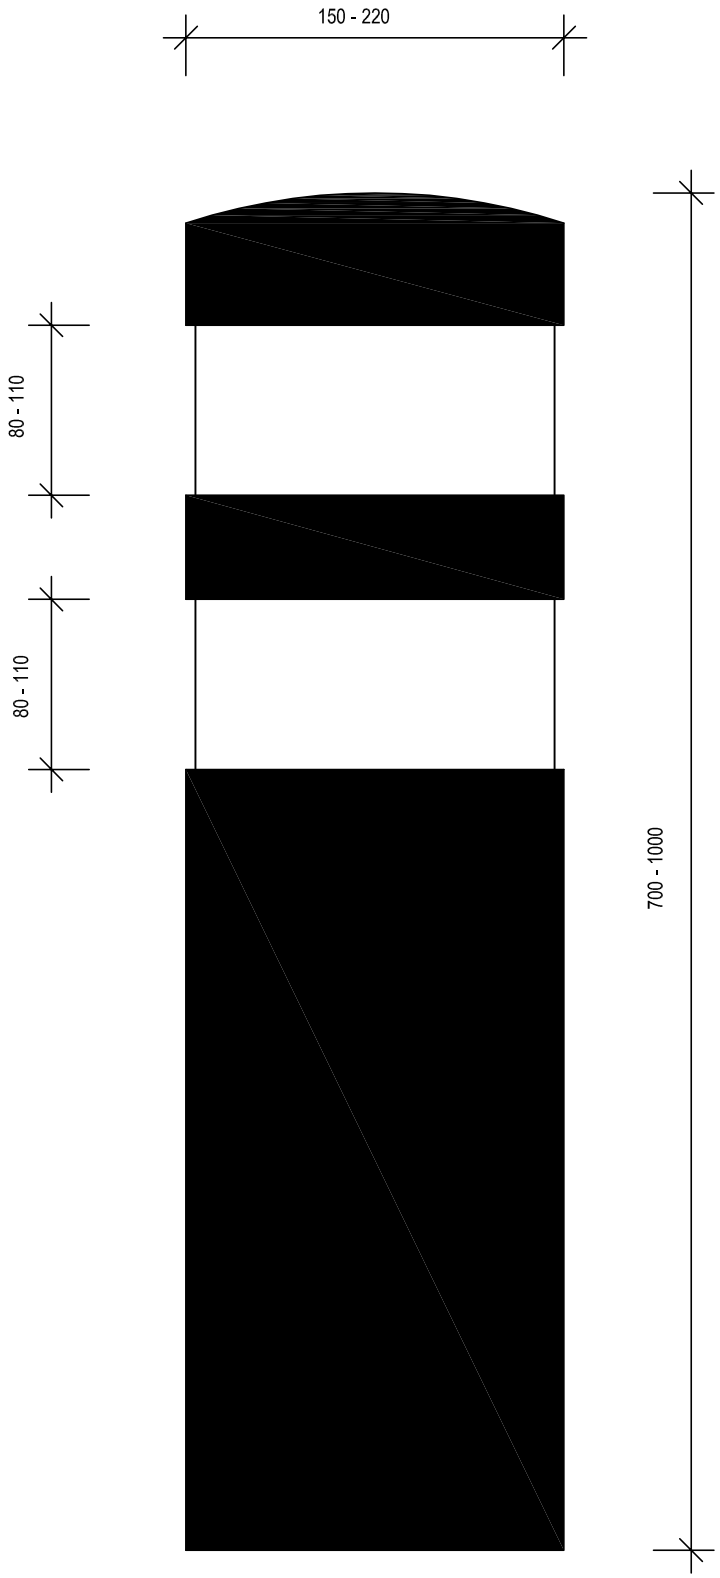

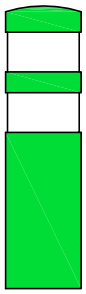

Z 11h

Pozn.: Další podrobnosti viz TP 58. Výška dána bez patky.

6 VYBAVENÍ POZEMNÍCH KOMUNIKACÍ 6.3 DOPRAVNÍ ZAŘÍZENÍ Z 11h Směrový sloupek zelený kulatý - baliseta	MINISTERSTVO DOPRAVY ODBOR POZEMNÍCH KOMUNIKACÍ VZOROVÉ LISTY	VL 6 Z 11h 02.17

VZOROVÉ LISTY STAVEB POZEMNÍCH KOMUNIKACÍ – VL 6.3 – DOPRAVNÍ ZAŘÍZENÍ

Vydalo:	Ministerstvo dopravy
Zpracovatel.:	Ing. Pavel Tučka (Centrum dopravního výzkumu, v.v.i.)
Tech. redakční rada:	JUDr. Ladislav Decarli (Ministerstvo dopravy)
	Ing. Alena Stupková (Ministerstvo dopravy)
	Ing. Mikuláš Bureš (Ministerstvo vnitra ČR)
	Ing. Michal Caudr (ŘSD ČR)
	Michal Prášil (ŘSD ČR)
	Pplk. JUDr. Sabina Burdová (Policie ČR)
	Ing. Jan Cvetler (ČMADZ)
	Ing. Karel Hofman (ČMADZ)
	Ing. Pavel Znamenáček (Pragoprojekt)
	Ing. Martin Tóth (Silniční vývoj - ZDZ)
	Ing. Antonín Seidl (D.I.A.S.)
Zástupce koordinátora:	Ing. Pavel Skládaný (Centrum dopravního výzkumu, v.v.i.)